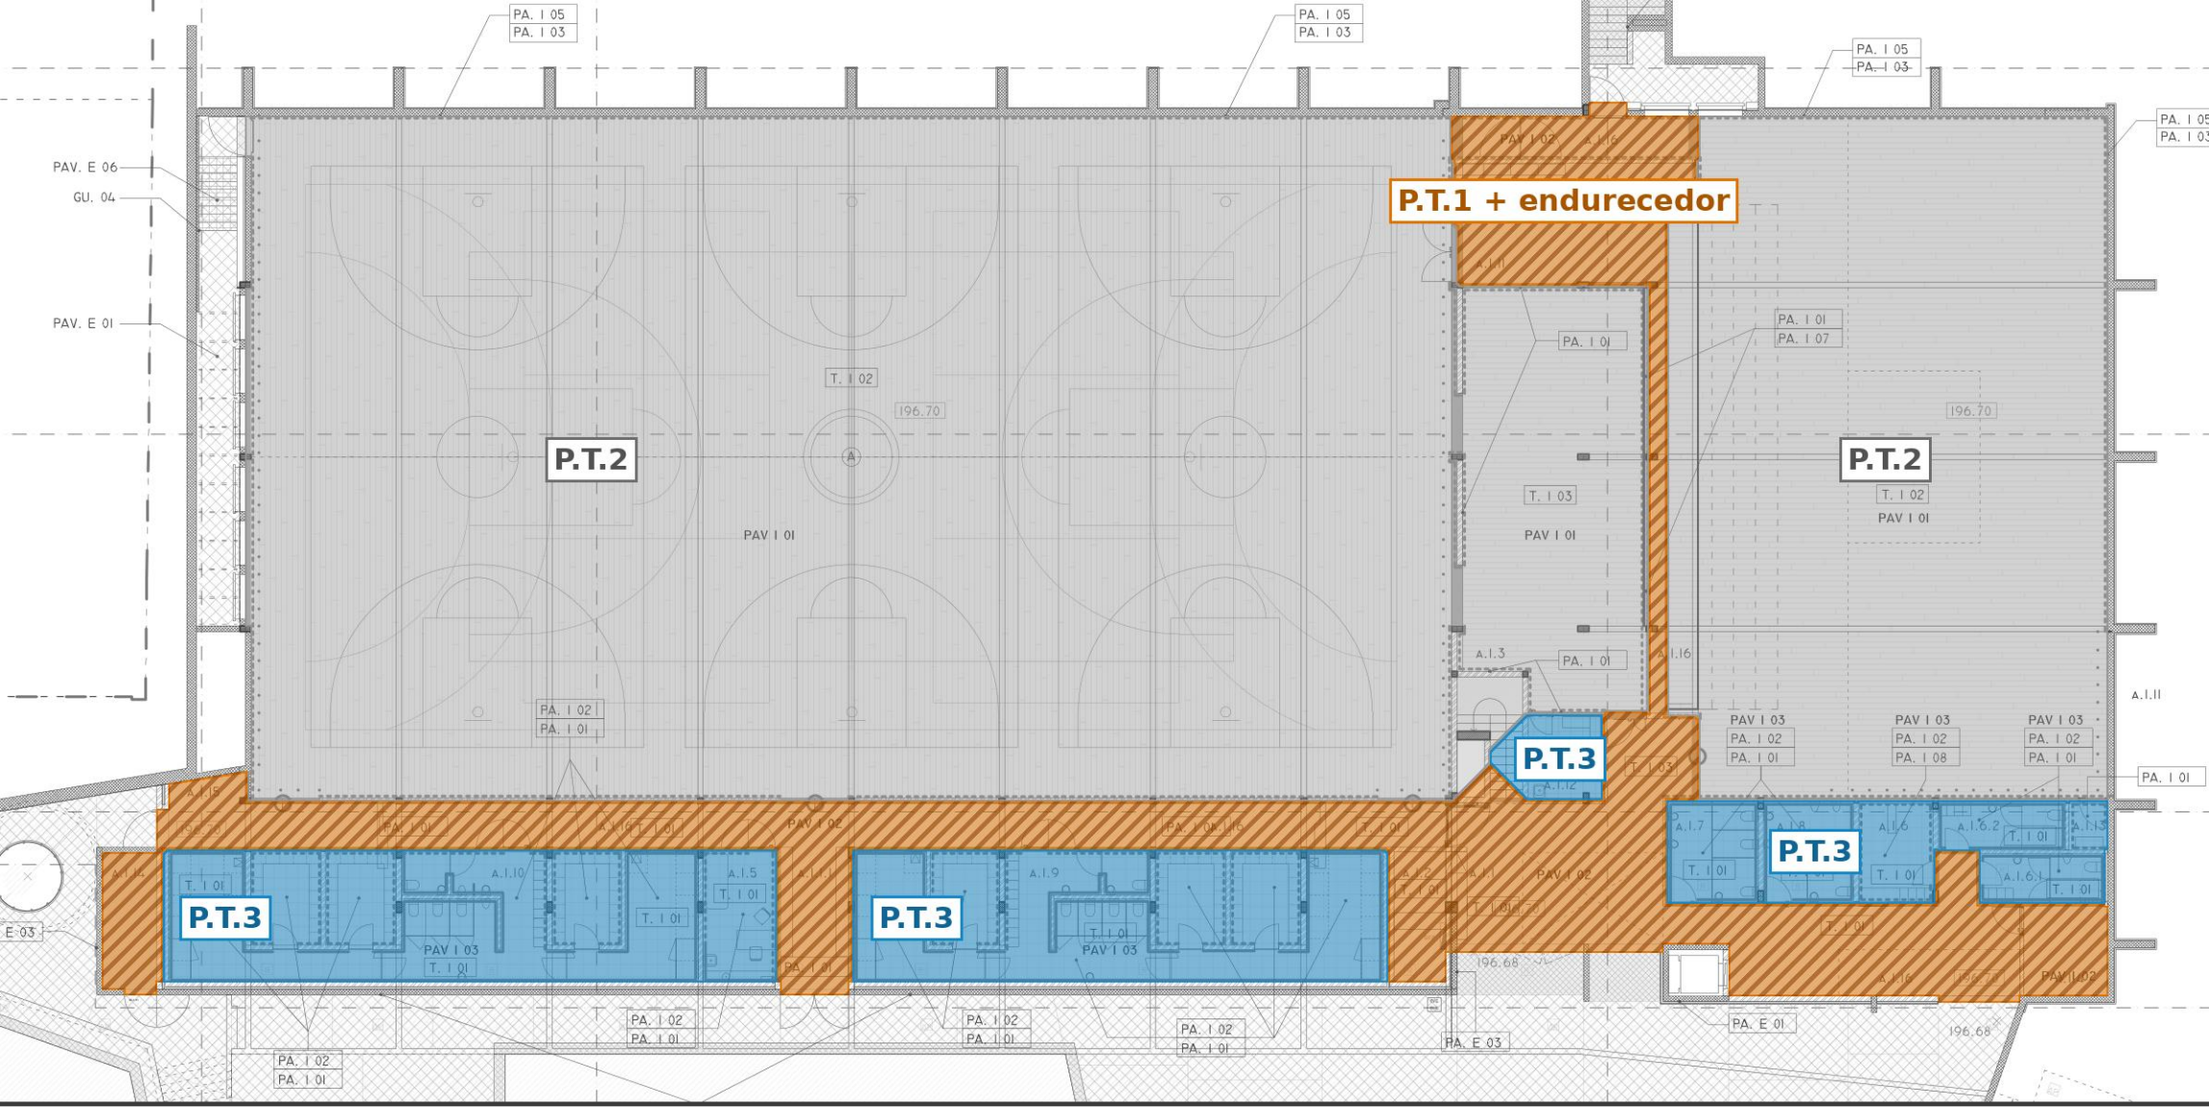


PAVIMENTO TÉRREO E ENDURECEDOR DE SUPERFÍCIE — PISO 01


Folha 3.2.2 Piso 01, esc. 1:200. Zonas pelo acabamento do pavimento; paredes interiores incluídas na zona contígua.

P.T.1 — Pavimento térreo com caixa de brita de 0,22 m — sob o pavimento PAV I 02 (betão armado com endurecedor de superfície) (art. 2.3.14.1)

ENDUR. — Endurecedor de superfície de quartzo 4 kg/m² — na mesma zona do P.T.1 (art. 2.6.3) — às riscas

P.T.3 — Pavimento térreo com caixa de brita de 0,17 m — sob o pavimento PAV I 03 (mosaico hidráulico: balneários, I.S., gabinete médico e arrumos) (art. 2.3.14.3)

P.T.2 — Pavimento térreo com caixa de brita de 0,15 m — sob o pavimento desportivo PAV I 01 (Polidesportivo, Ginásio e Sala de Ginástica) — referência (art. 2.3.14.2)

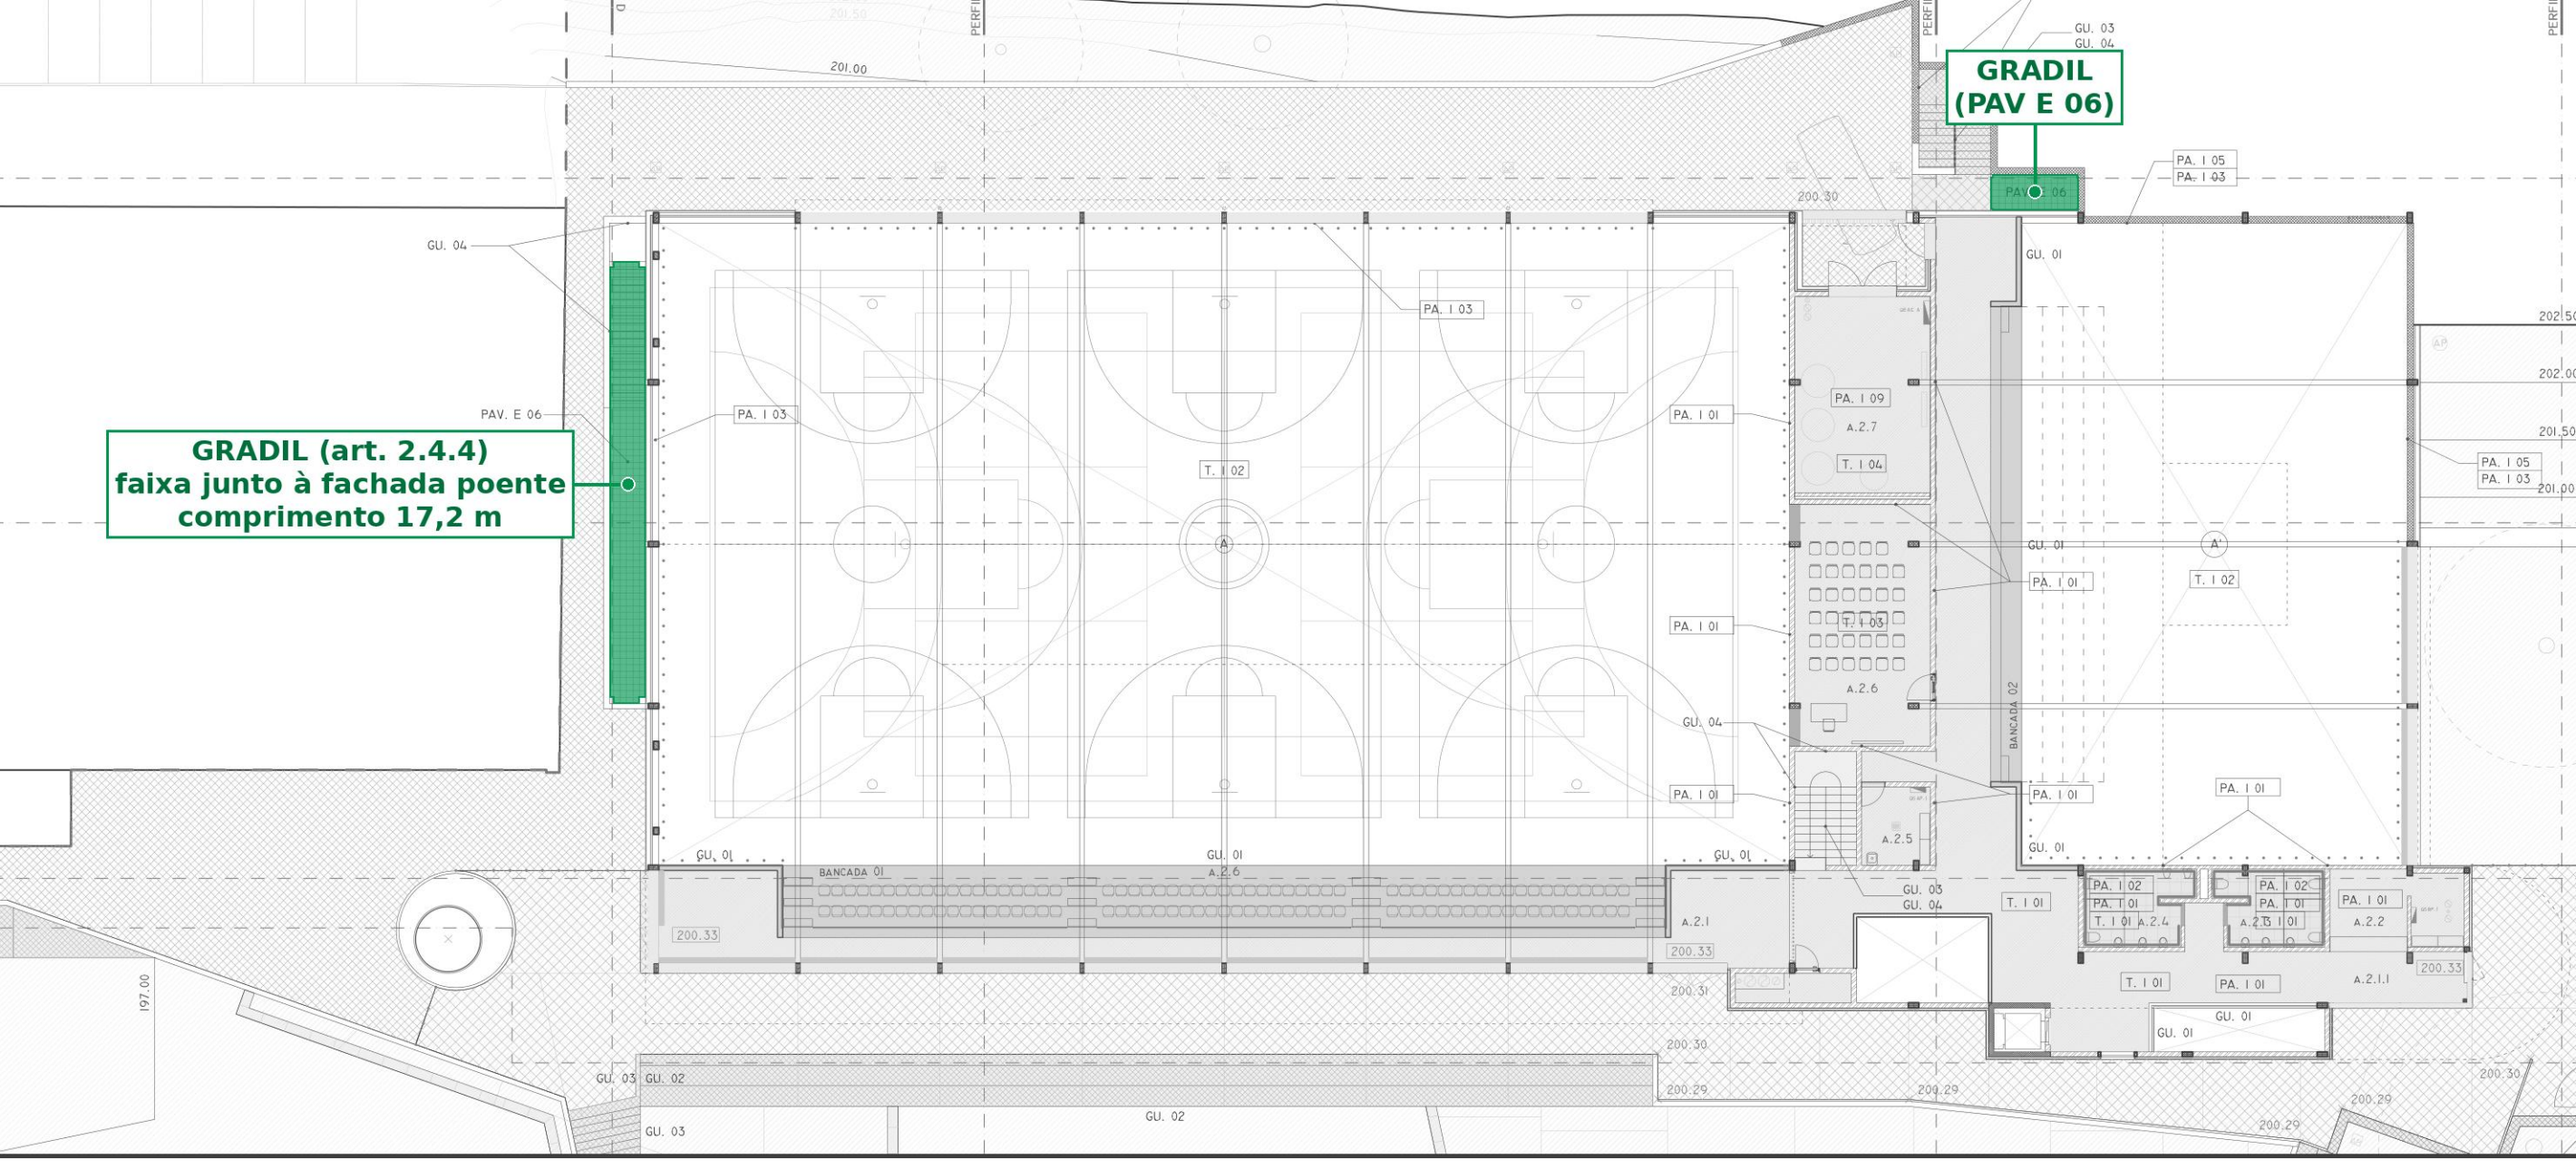

GRADIL — PISO 02

Planta de acabamentos 3.2 (folha 3.2.3 Piso 02, esc. 1:200). Zonas com a trama PAV E 06 (gradil de aço).

GRADIL Gradil para pavimento com 0,30 m de espessura, malha 0,030 x 0,030 m, 27 kg/m², aço ST 37.2 — zonas PAV E 06 (gradil de aço) da planta de acabamentos (art. 2.4.4)