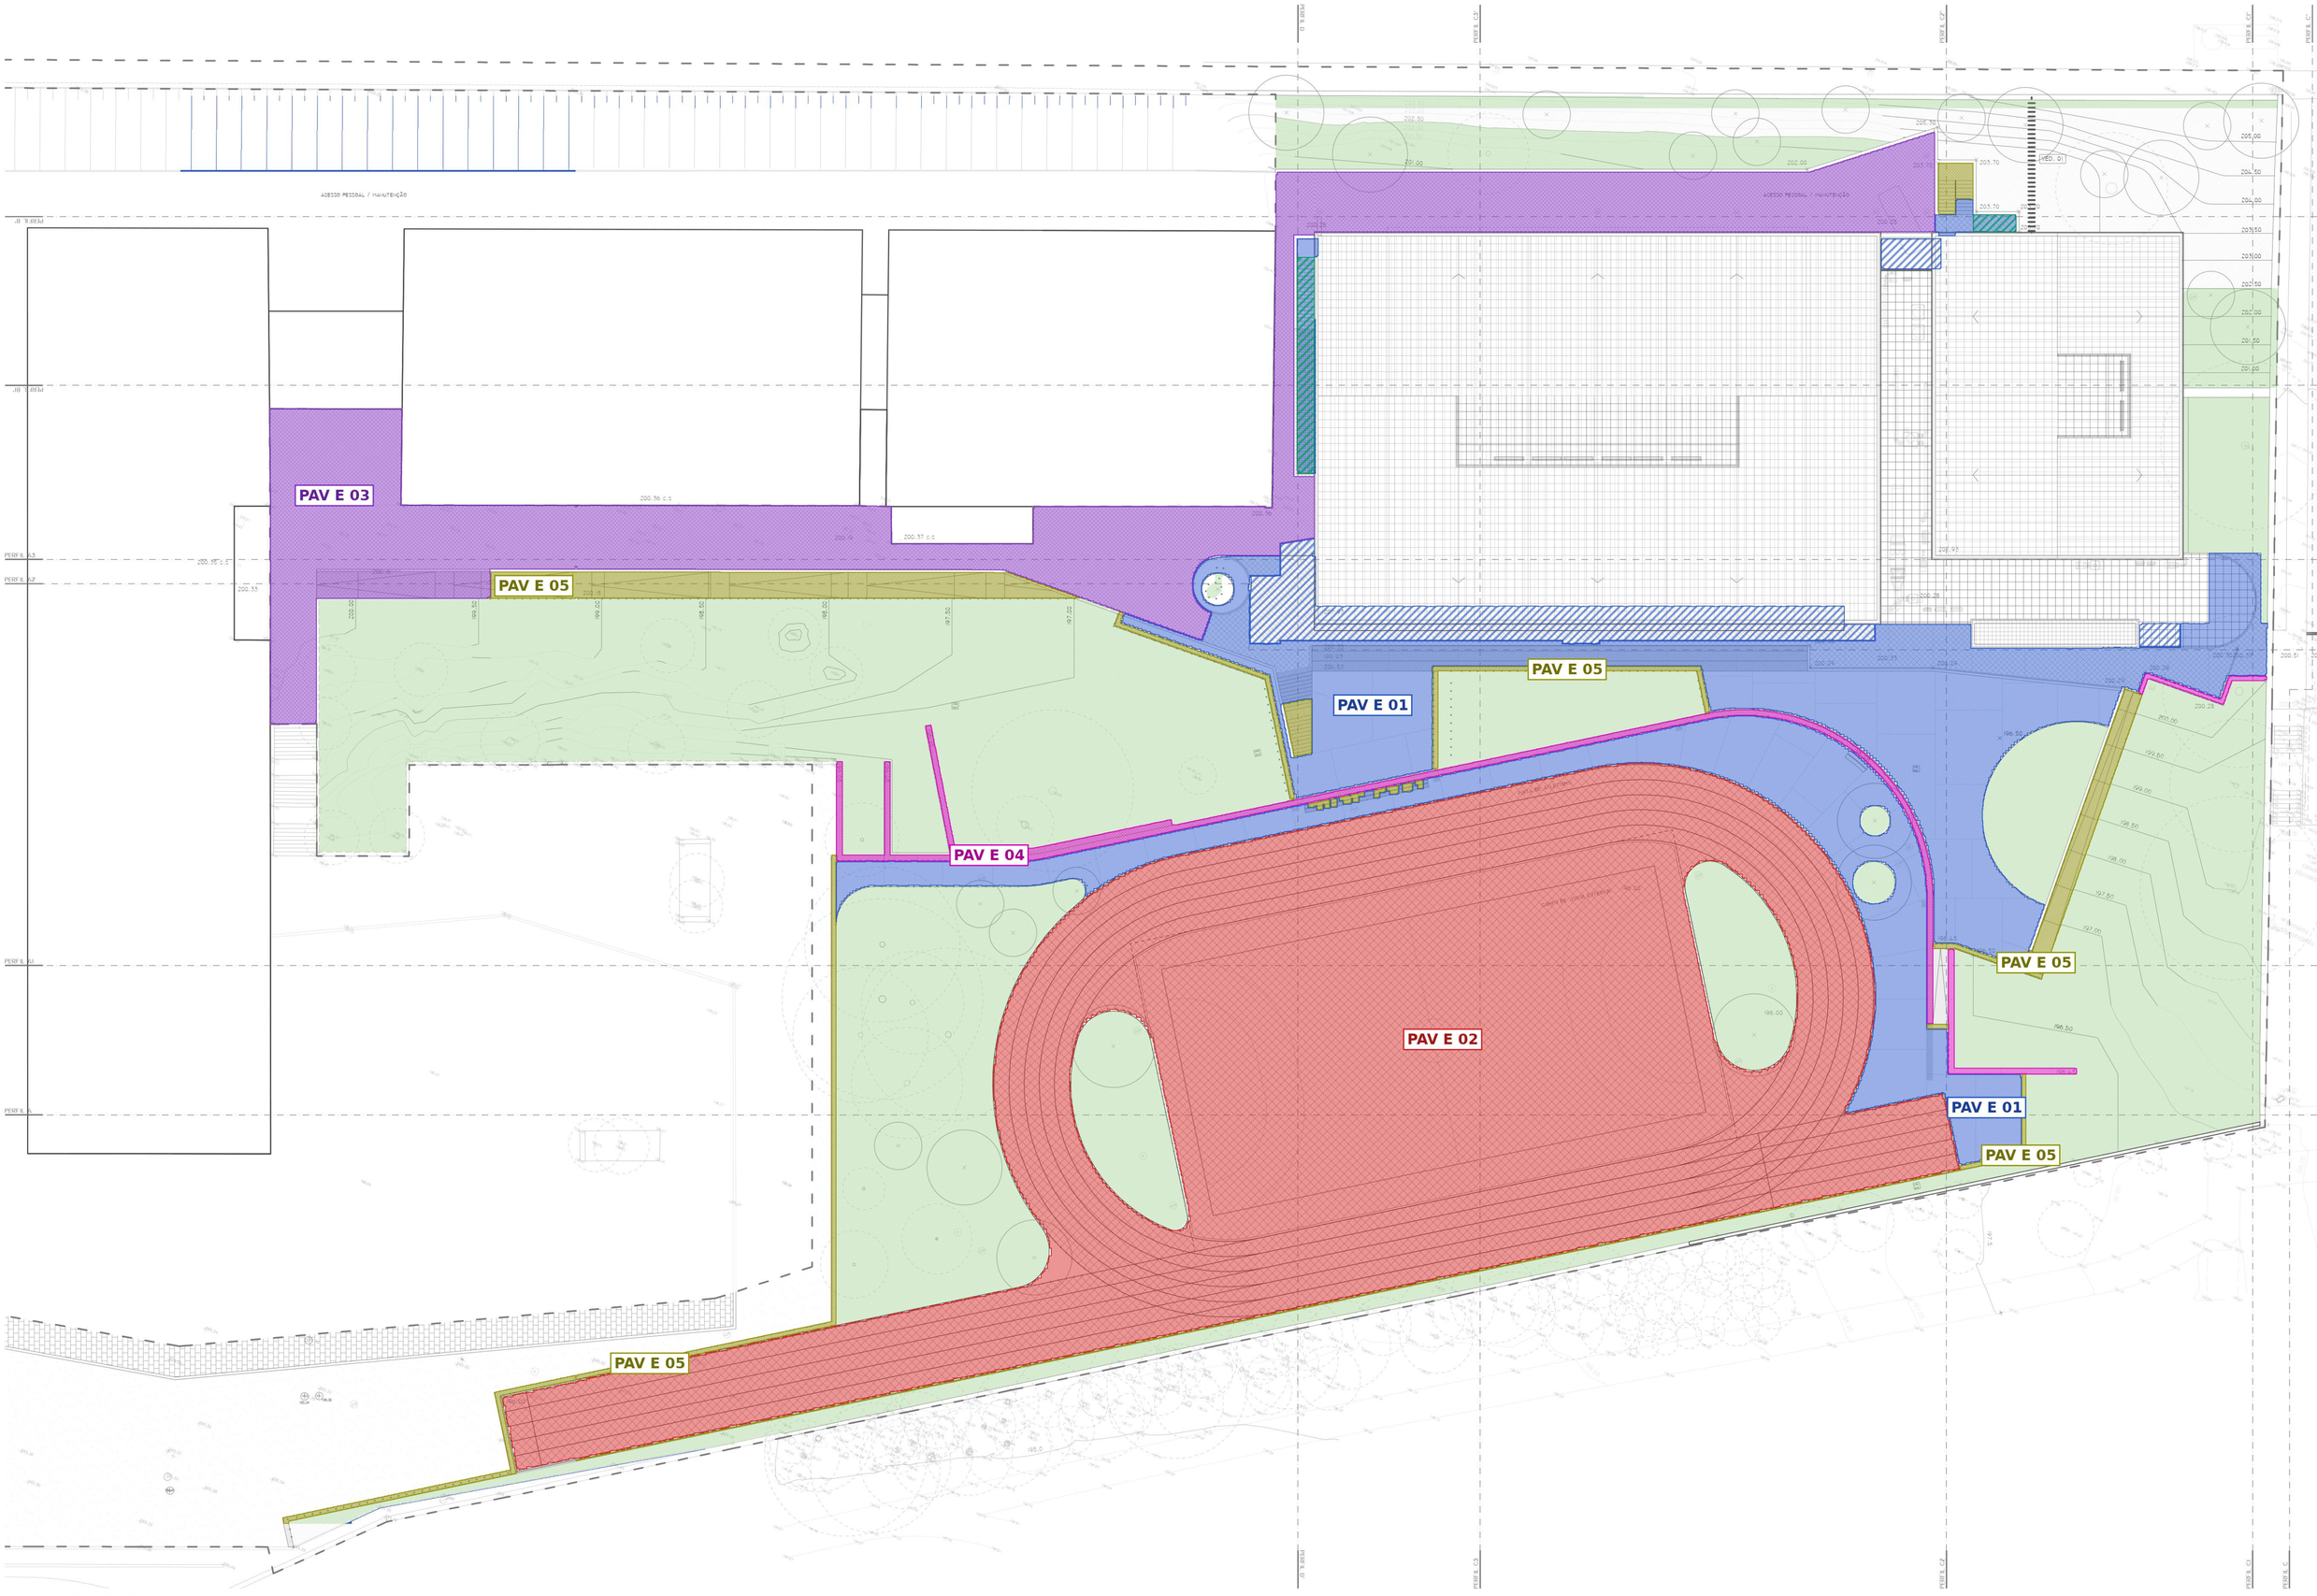


designação do projecto:
PAVILHÃO JOÃO DE MEIRA
fase:
PROJETO DE EXECUÇÃO
designação do desenho:
ACABAMENTOS - COBERTURA
localização:
GUIMARÃES


DEPARTAMENTO DE OBRAS MUNICIPAIS

arquitectura:
FILIPE SILVA ARQ.
data:
7/7/2026
escala:
1:250

PAVIMENTOS EXTERIORES — IMPLANTAÇÃO GERAL

Planta de acabamentos 3.2 (folha 3.2.1 Coberturas, esc. 1:250, com as zonas das folhas 3.2.2 Piso 01 e 3.2.3 Piso 02). Zonas de pavimento medidas.


- **PAV E 01** Pavimento tipo Secil Unipiso ou equiv. (mín. 10 cm de espessura) (art. 3.9.2.5)
- **PAV E 02** Piso desportivo: base betuminosa com acabamento em resina tipo Sika Colorsport (art. 3.9.2.8)
- **PAV E 03** Pavimento betuminoso (art. 3.9.2.9)
- **PAV E 04** Banco pré-fabricado conforme desenhos de pormenor (art. 3.9.2.1)
- **PAV E 05** Pré-fabricados de betão tipo ACL ou equiv. (art. 3.9.2.11)
- **PAV E 01** Pavimento tipo Secil Unipiso ou equiv. (mín. 10 cm de espessura) (art. 3.9.2.5) — às riscas: no terraço do Piso 02, sobre os balneários
- **PAV E 06** Gradil de aço (art. 2.4.4) — às riscas: no Piso 02, junto à fachada poente do pavilhão
- **VERDE** Zonas verdes (não pavimentadas — referência)

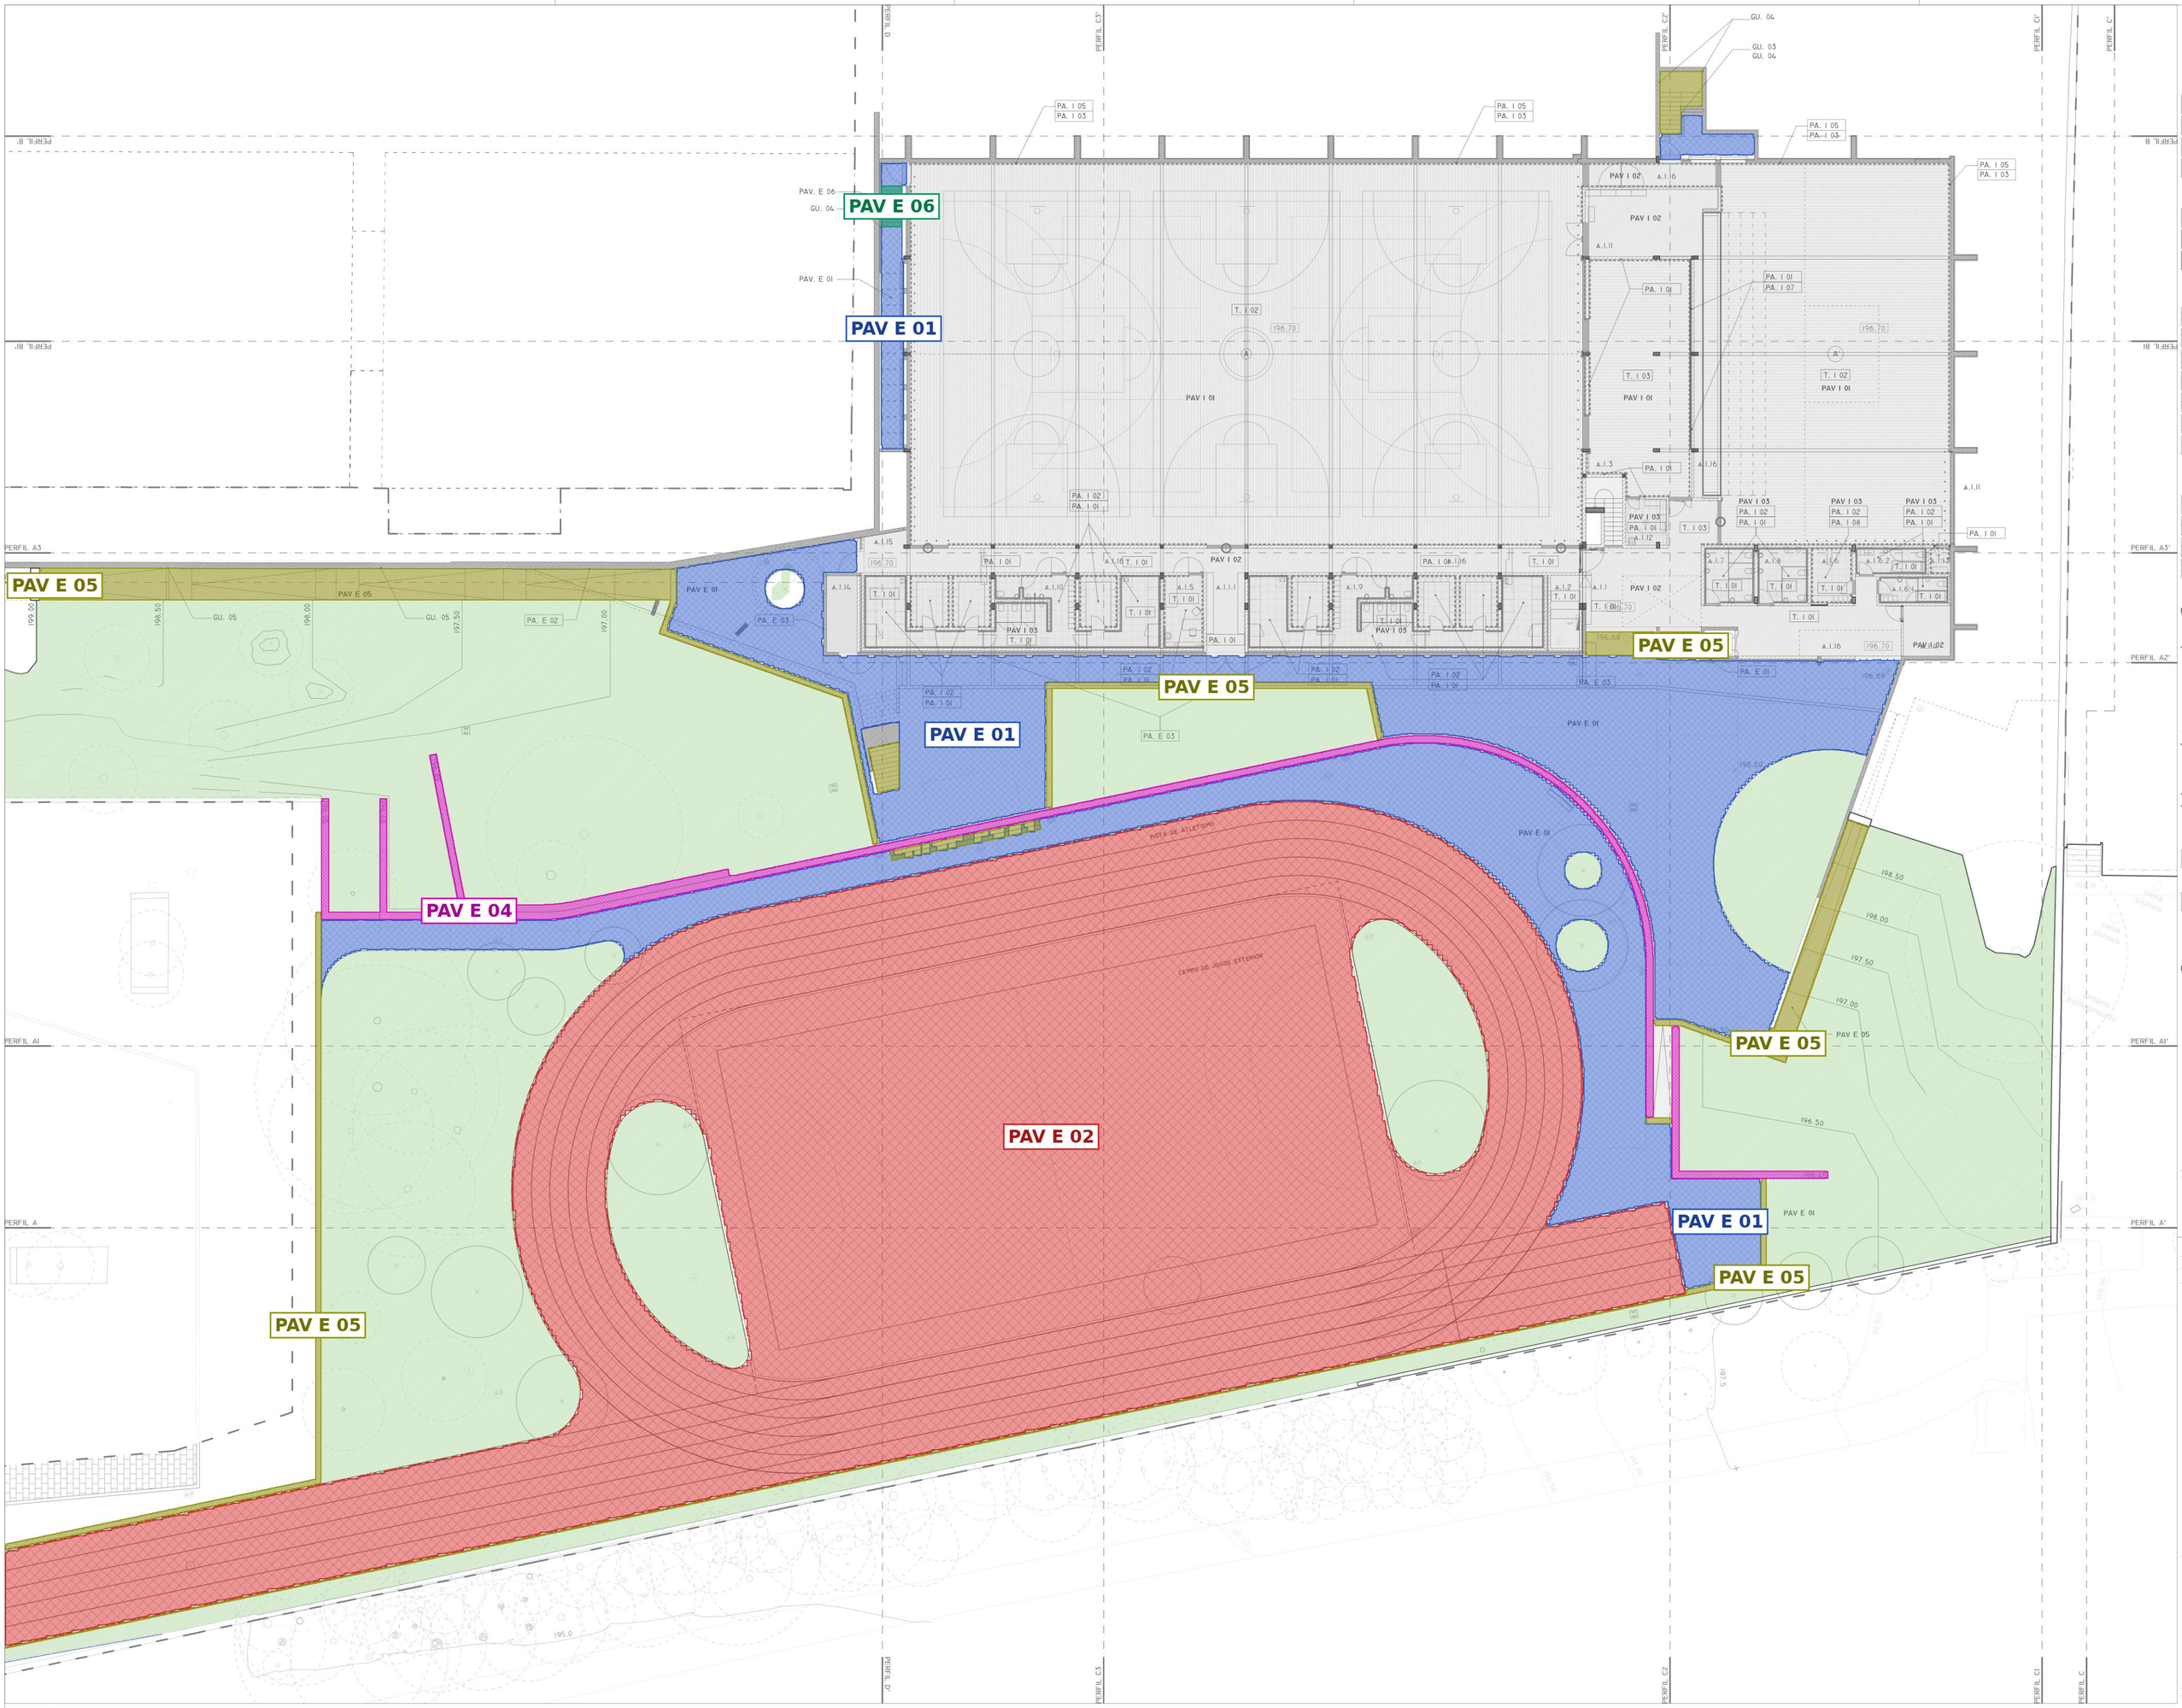

PAVIMENTOS EXTERIORES — PISO 01

Planta de acabamentos 3.2 (folha 3.2.2 Piso 01, esc. 1:200). Zonas de pavimento exterior medidas.


PAV E 01	Pavimento tipo Secil Unipiso ou equiv. (mín. 10 cm de espessura) (art. 3.9.2.5)
PAV E 02	Piso desportivo: base betuminosa com acabamento em resina tipo Sika Colorsport (art. 3.9.2.8)
PAV E 04	Banco pré-fabricado conforme desenhos de pormenor (art. 3.9.2.1)
PAV E 05	Pré-fabricados de betão tipo ACL ou equiv. (art. 3.9.2.11)
PAV E 06	Gradil de aço (art. 2.4.4)
VERDE	Zonas verdes (não pavimentadas — referência)

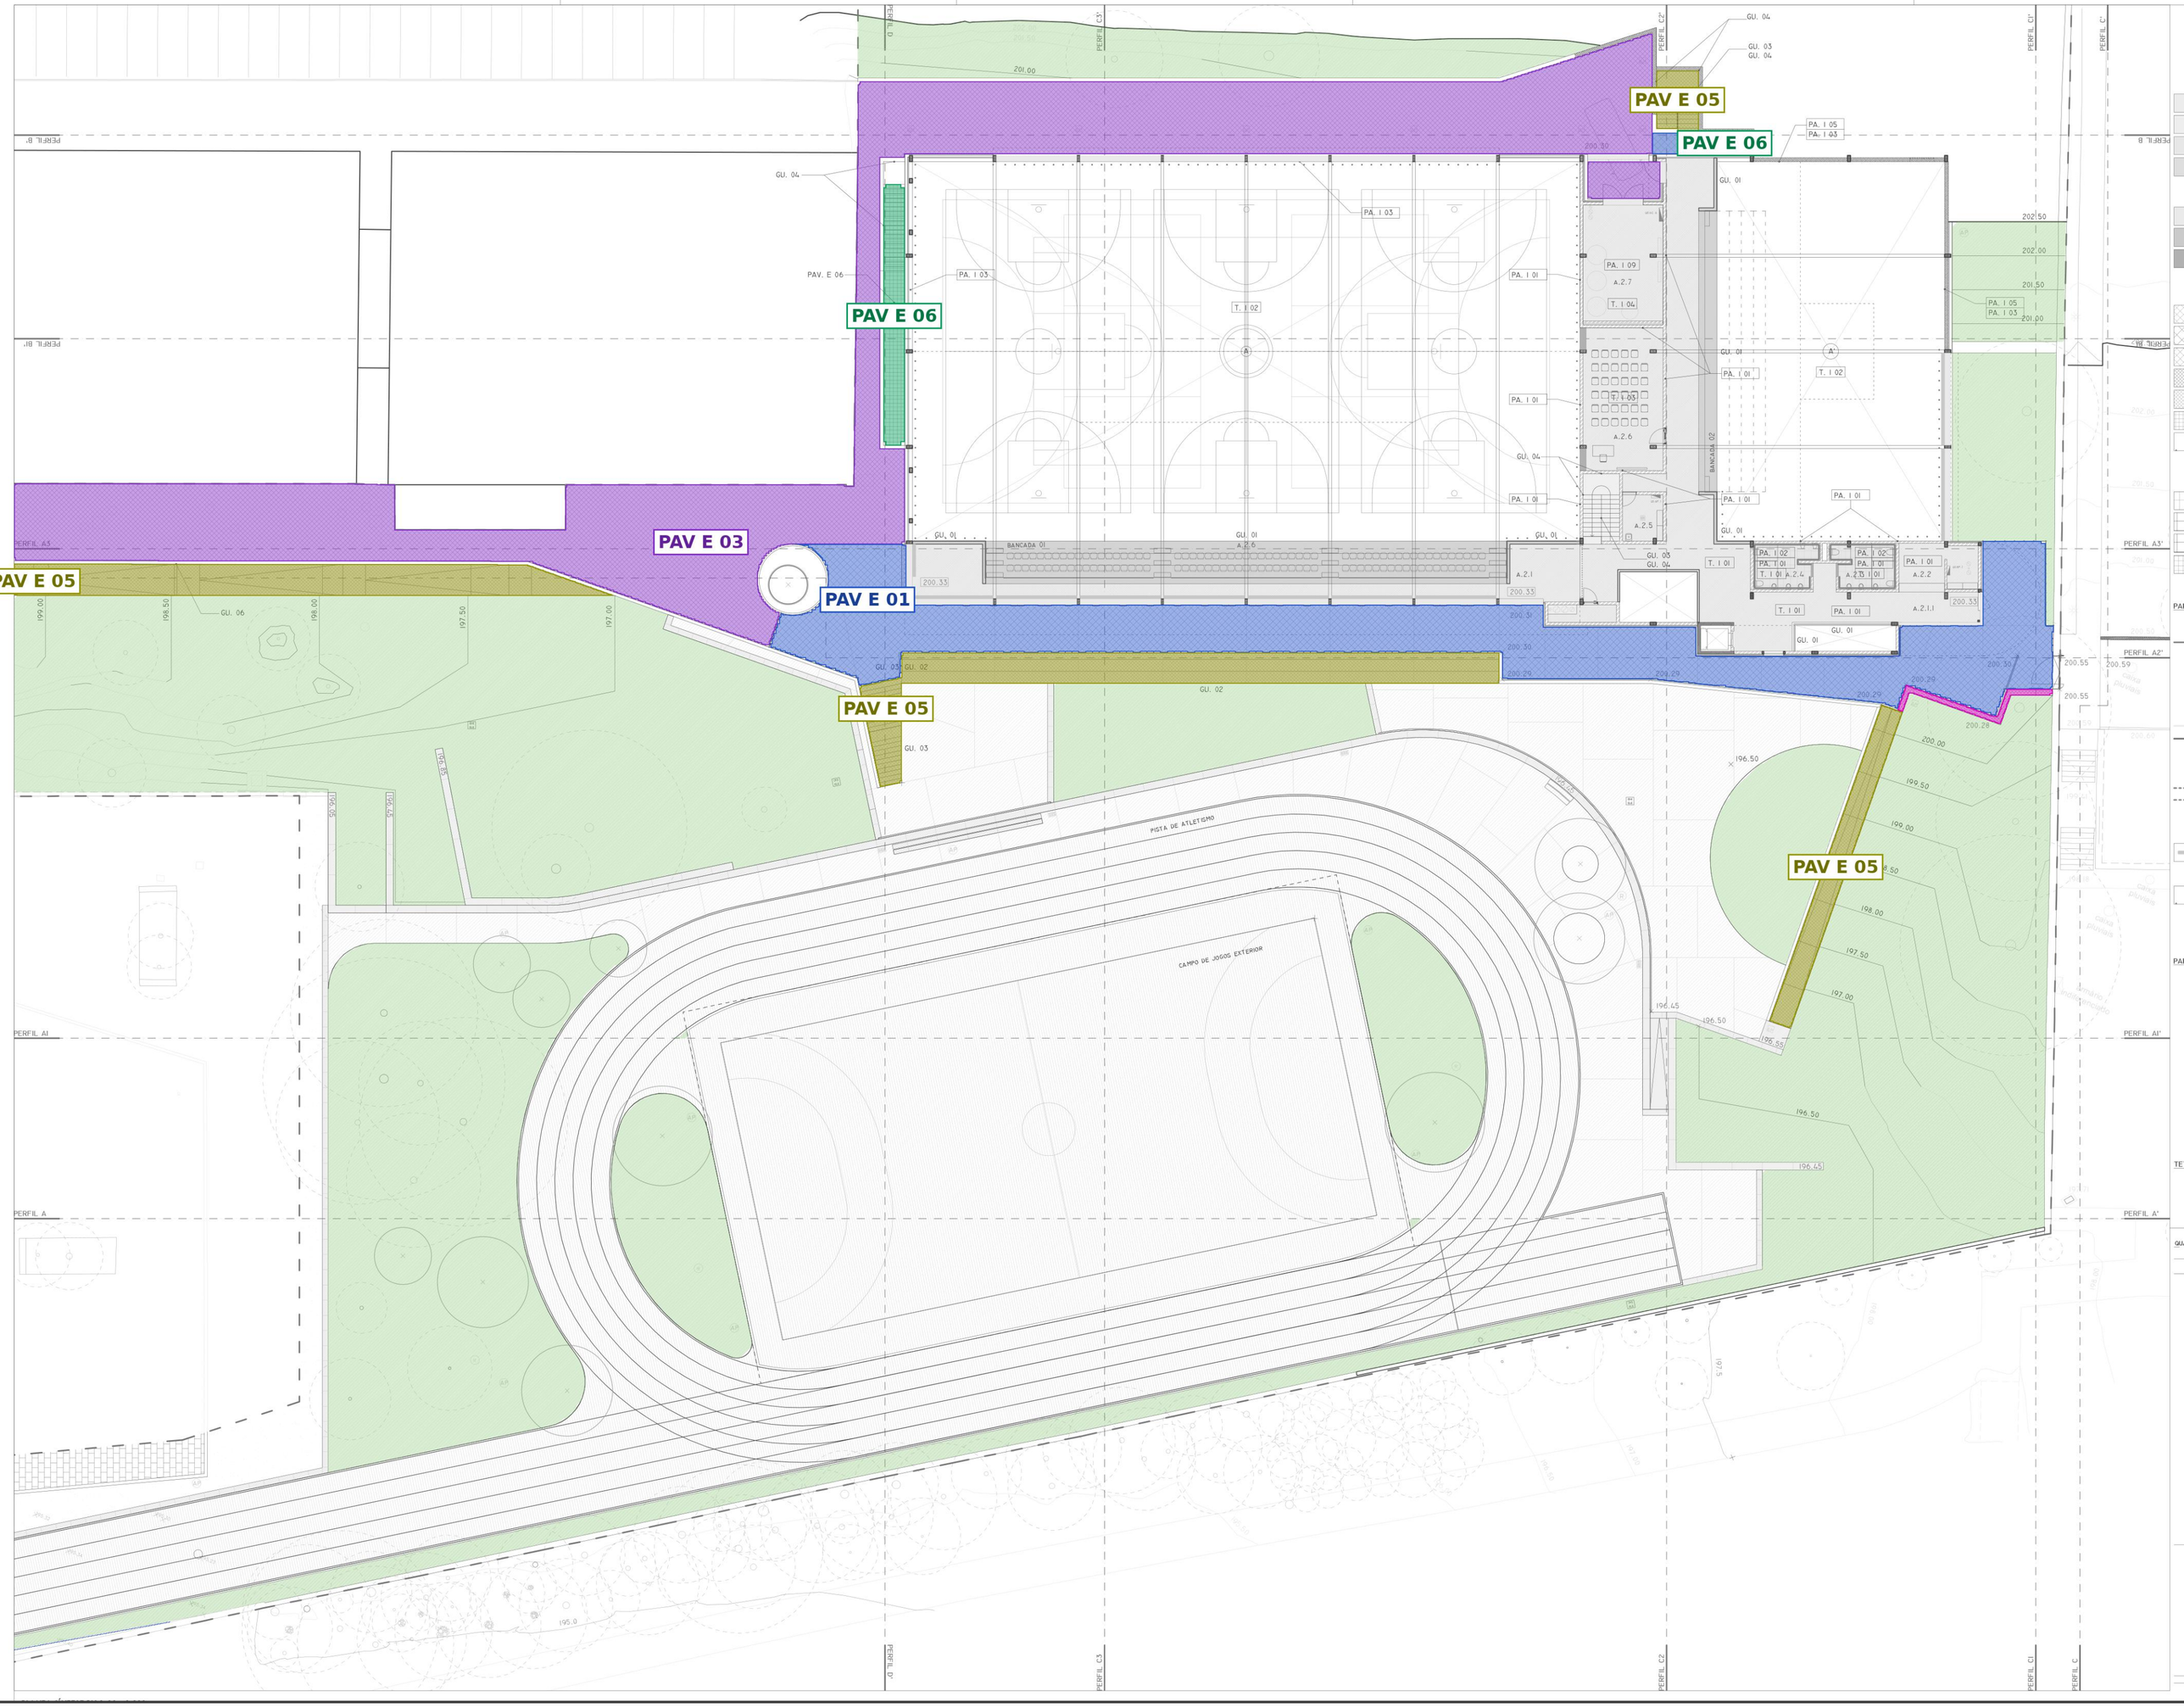

PAVIMENTOS EXTERIORES — PISO 02

Planta de acabamentos 3.2 (folha 3.2.3 Piso 02, esc. 1:200). Zonas de pavimento exterior medidas.


- **PAV E 01** Pavimento tipo Secil Unipiso ou equiv. (mín. 10 cm de espessura) (art. 3.9.2.5)
- **PAV E 03** Pavimento betuminoso (art. 3.9.2.9)
- **PAV E 04** Banco pré-fabricado conforme desenhos de pormenor (art. 3.9.2.1)
- **PAV E 05** Pré-fabricados de betão tipo ACL ou equiv. (art. 3.9.2.11)
- **PAV E 06** Gradil de aço (art. 2.4.4)
- **VERDE** Zonas verdes (não pavimentadas — referência)

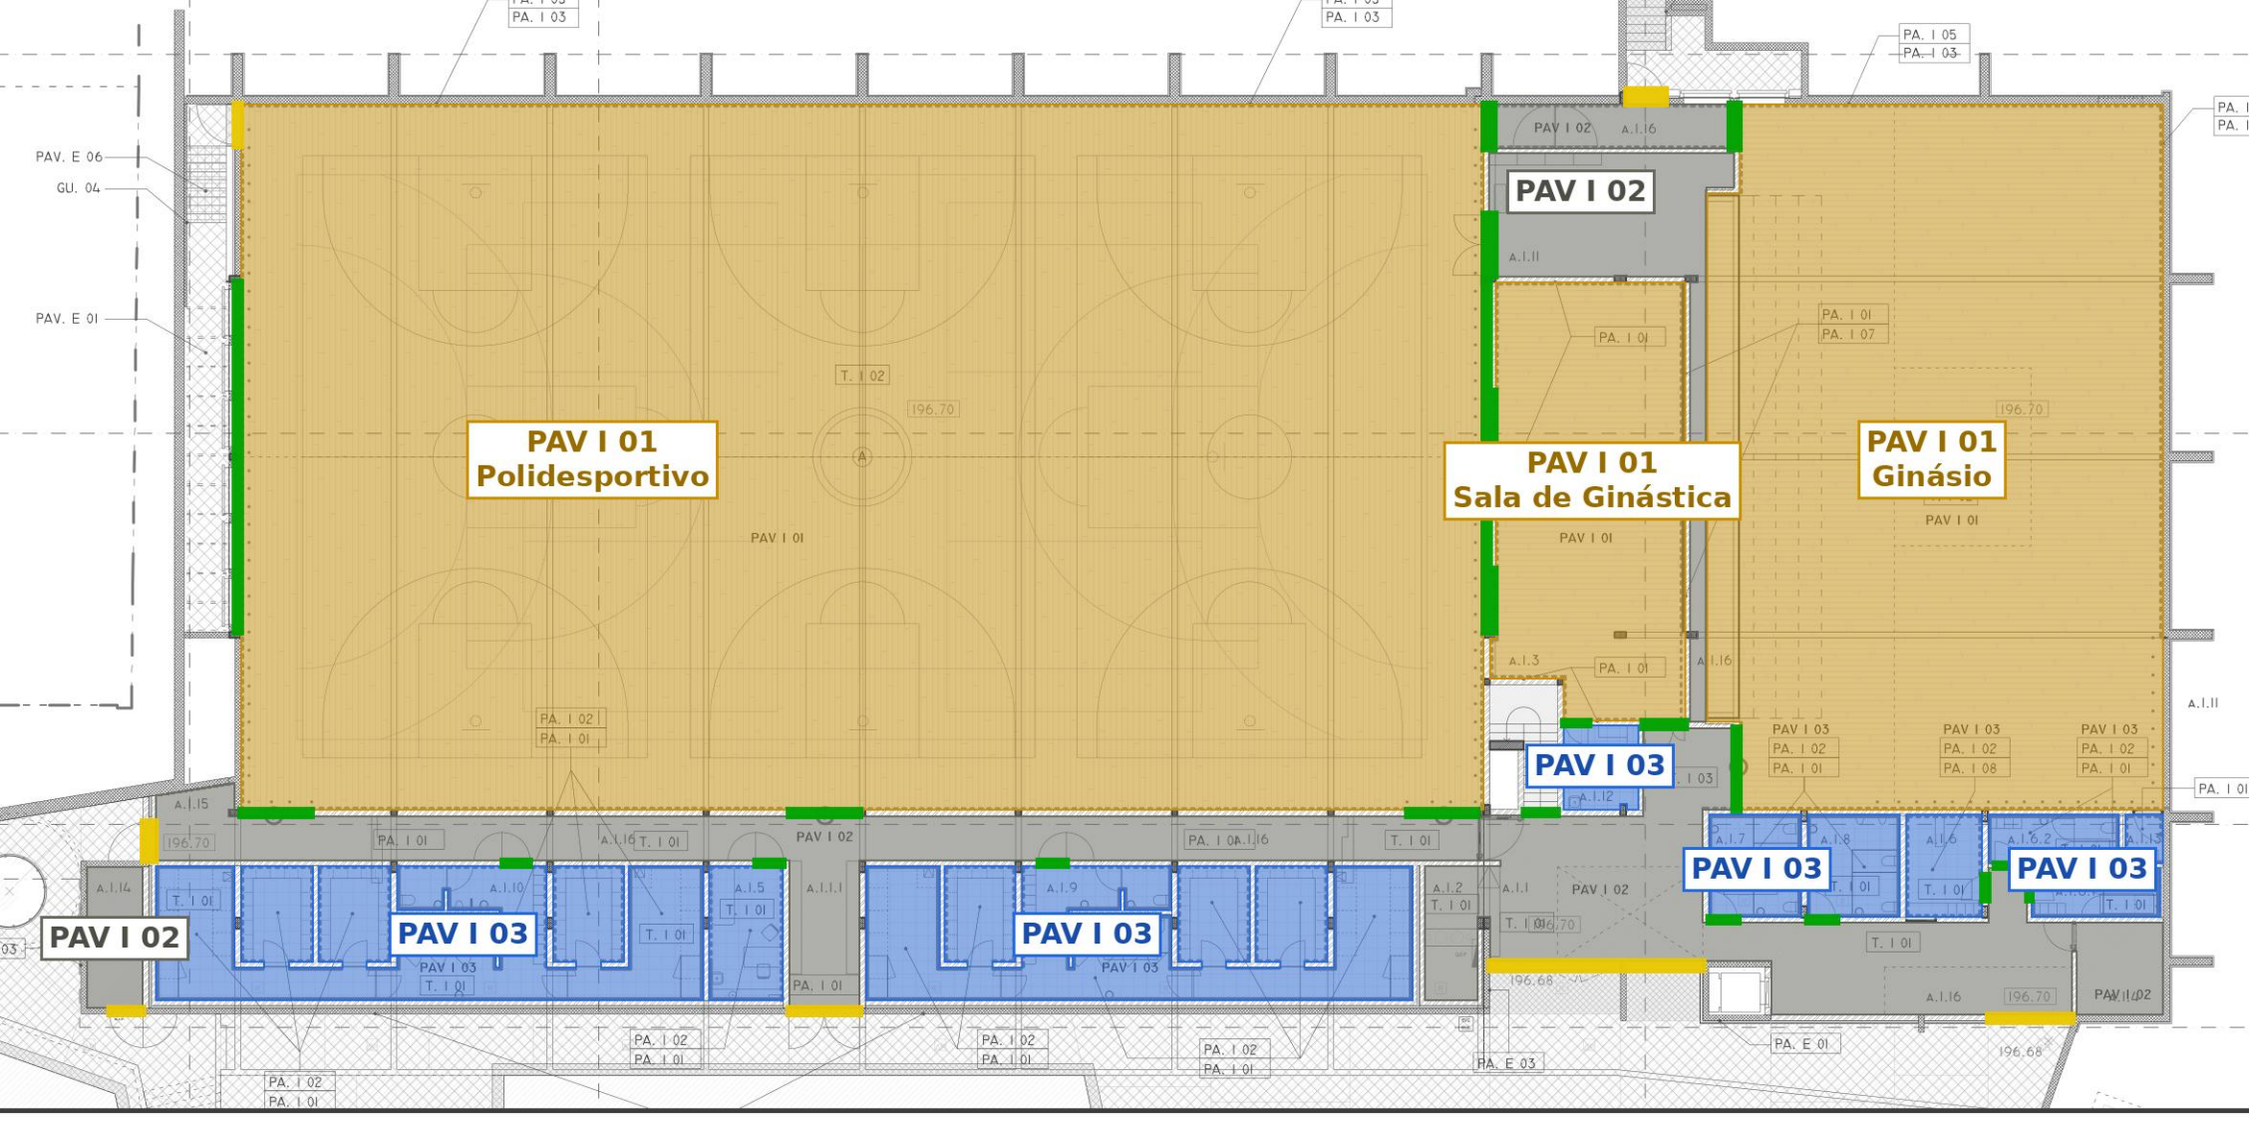

PAVIMENTOS INTERIORES — PISO 01

Planta de acabamentos 3.2 (folha 3.2.2 Piso 01, esc. 1:200). Zonas de pavimento interior e soleiras.

	PAV I 01	Pavimento desportivo multicamada em madeira maciça (art. 3.9.1.1)
	PAV I 02	Betão armado com endurecedor de superfície (art. 3.9.1.2)
	PAV I 03	Mosaico hidráulico tipo ACL Marmocim ou equiv. (art. 3.9.1.3)
	SOL 01	Soleira pré-fabricada em betão polimérico tipo Tubani ou equiv. — vão exterior (art. 3.9.2.3)
	SOL 03	Soleira pré-fabricada em betão polimérico tipo Tubani ou equiv. — separação interior (art. 3.9.1.6)

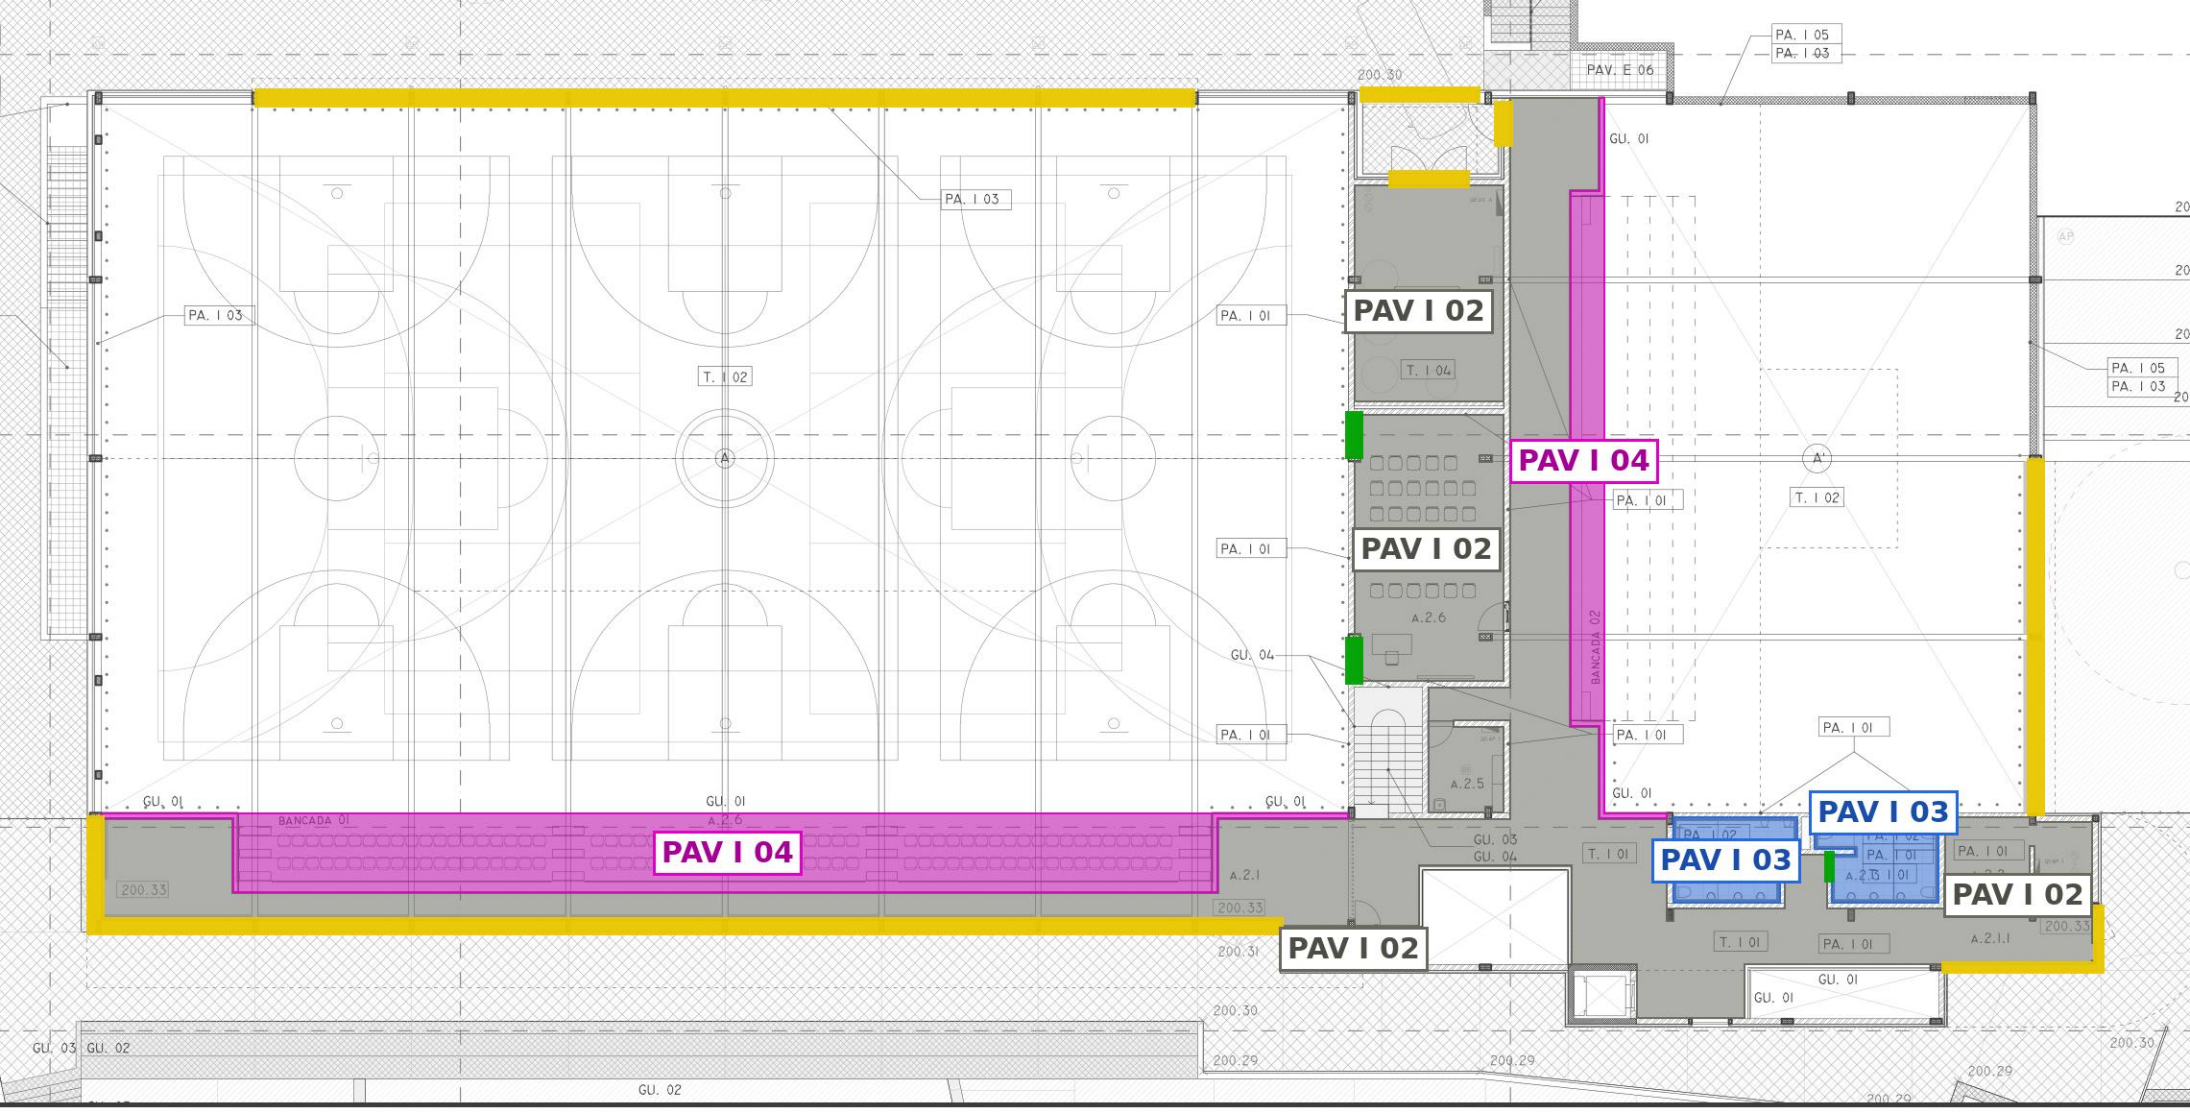

PAVIMENTOS INTERIORES — PISO 02

Planta de acabamentos 3.2 (folha 3.2.3 Piso 02, esc. 1:200). Zonas de pavimento interior e soleiras.

	PAV I 02	Betão armado com endurecedor de superfície (art. 3.9.1.2)
	PAV I 03	Mosaico hidráulico tipo ACL Marmocim ou equiv. (art. 3.9.1.3)
	PAV I 04	Pré-fabricados de betão tipo ACL ou equiv. (art. 3.9.1.4)
	SOL 01	Soleira pré-fabricada em betão polimérico tipo Tubani ou equiv. — vão exterior (art. 3.9.2.3)
	SOL 03	Soleira pré-fabricada em betão polimérico tipo Tubani ou equiv. — separação interior (art. 3.9.1.6)