
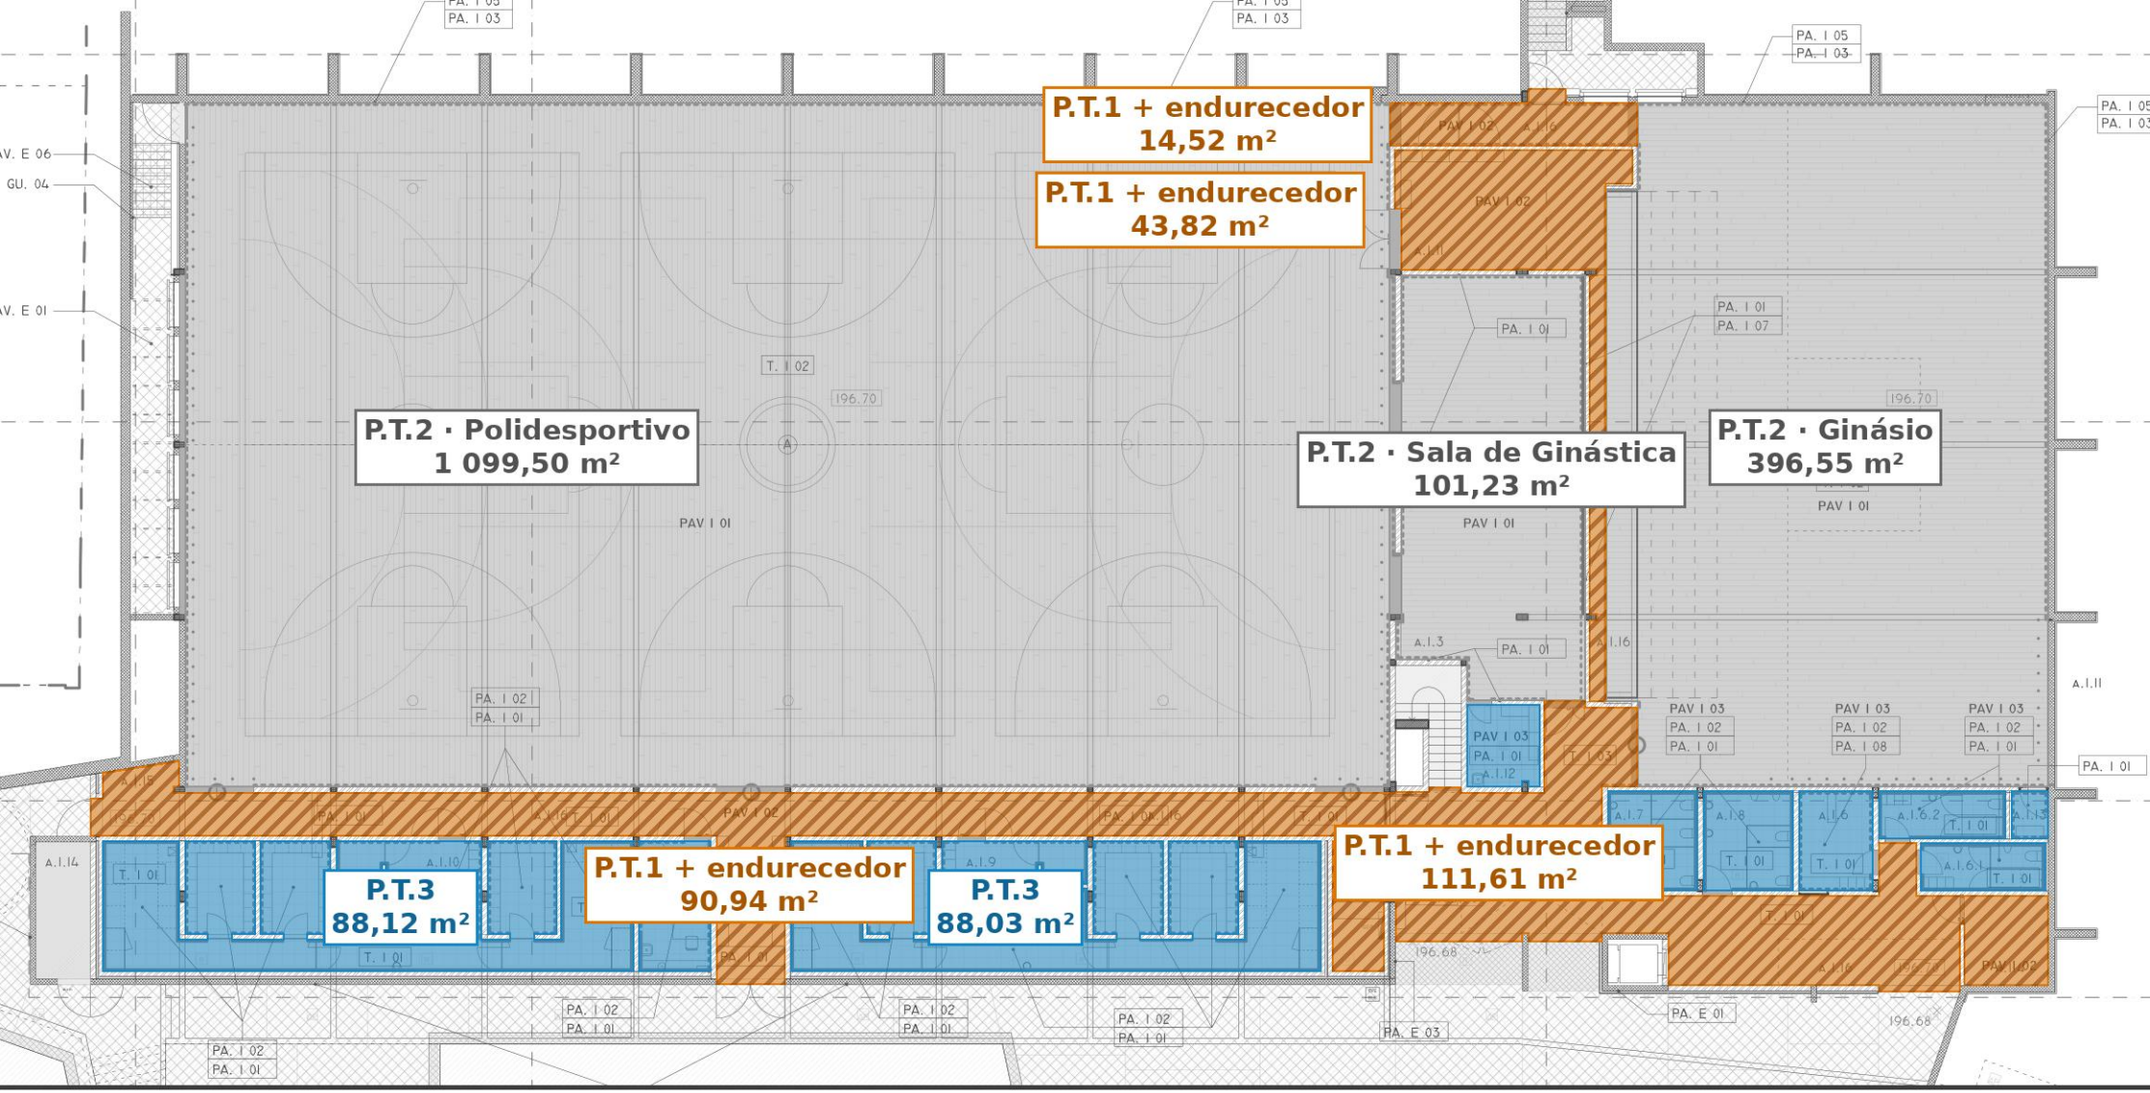


PAVIMENTO TÉRREO E ENDURECEDOR DE SUPERFÍCIE — PISO 01

Projeto de acabamentos 3.2 — folha 3.2.2 Piso 01, esc. 1:200. Áreas dos polígonos desenhados.


P.T.1	Pavimento térreo com caixa de brita de 0,22 m — zonas com pavimento PAV I 02 (betão armado com endurecedor): 260,89 m² + soleiras dentro destas zonas 4,96 m² = 265,84 m² (art. 2.3.14.1)
ENDUR.	Endurecedor de superfície de quartzo 4 kg/m² — mesma zona do P.T.1: 265,84 m² (art. 2.6.3) — às riscas
P.T.3	Pavimento térreo com caixa de brita de 0,17 m — zonas com pavimento PAV I 03 (balneários, I.S., gabinete médico, arrumos): 249,38 m² (art. 2.3.14.3)
P.T.2	Pavimento térreo com caixa de brita de 0,15 m — zonas com pavimento desportivo PAV I 01: 1 597,28 m² (art. 2.3.14.2)
TOTAL	P.T.1 e endurecedor, Piso 01 + Piso 02 = 265,84 + 347,07 = 612,92 m²

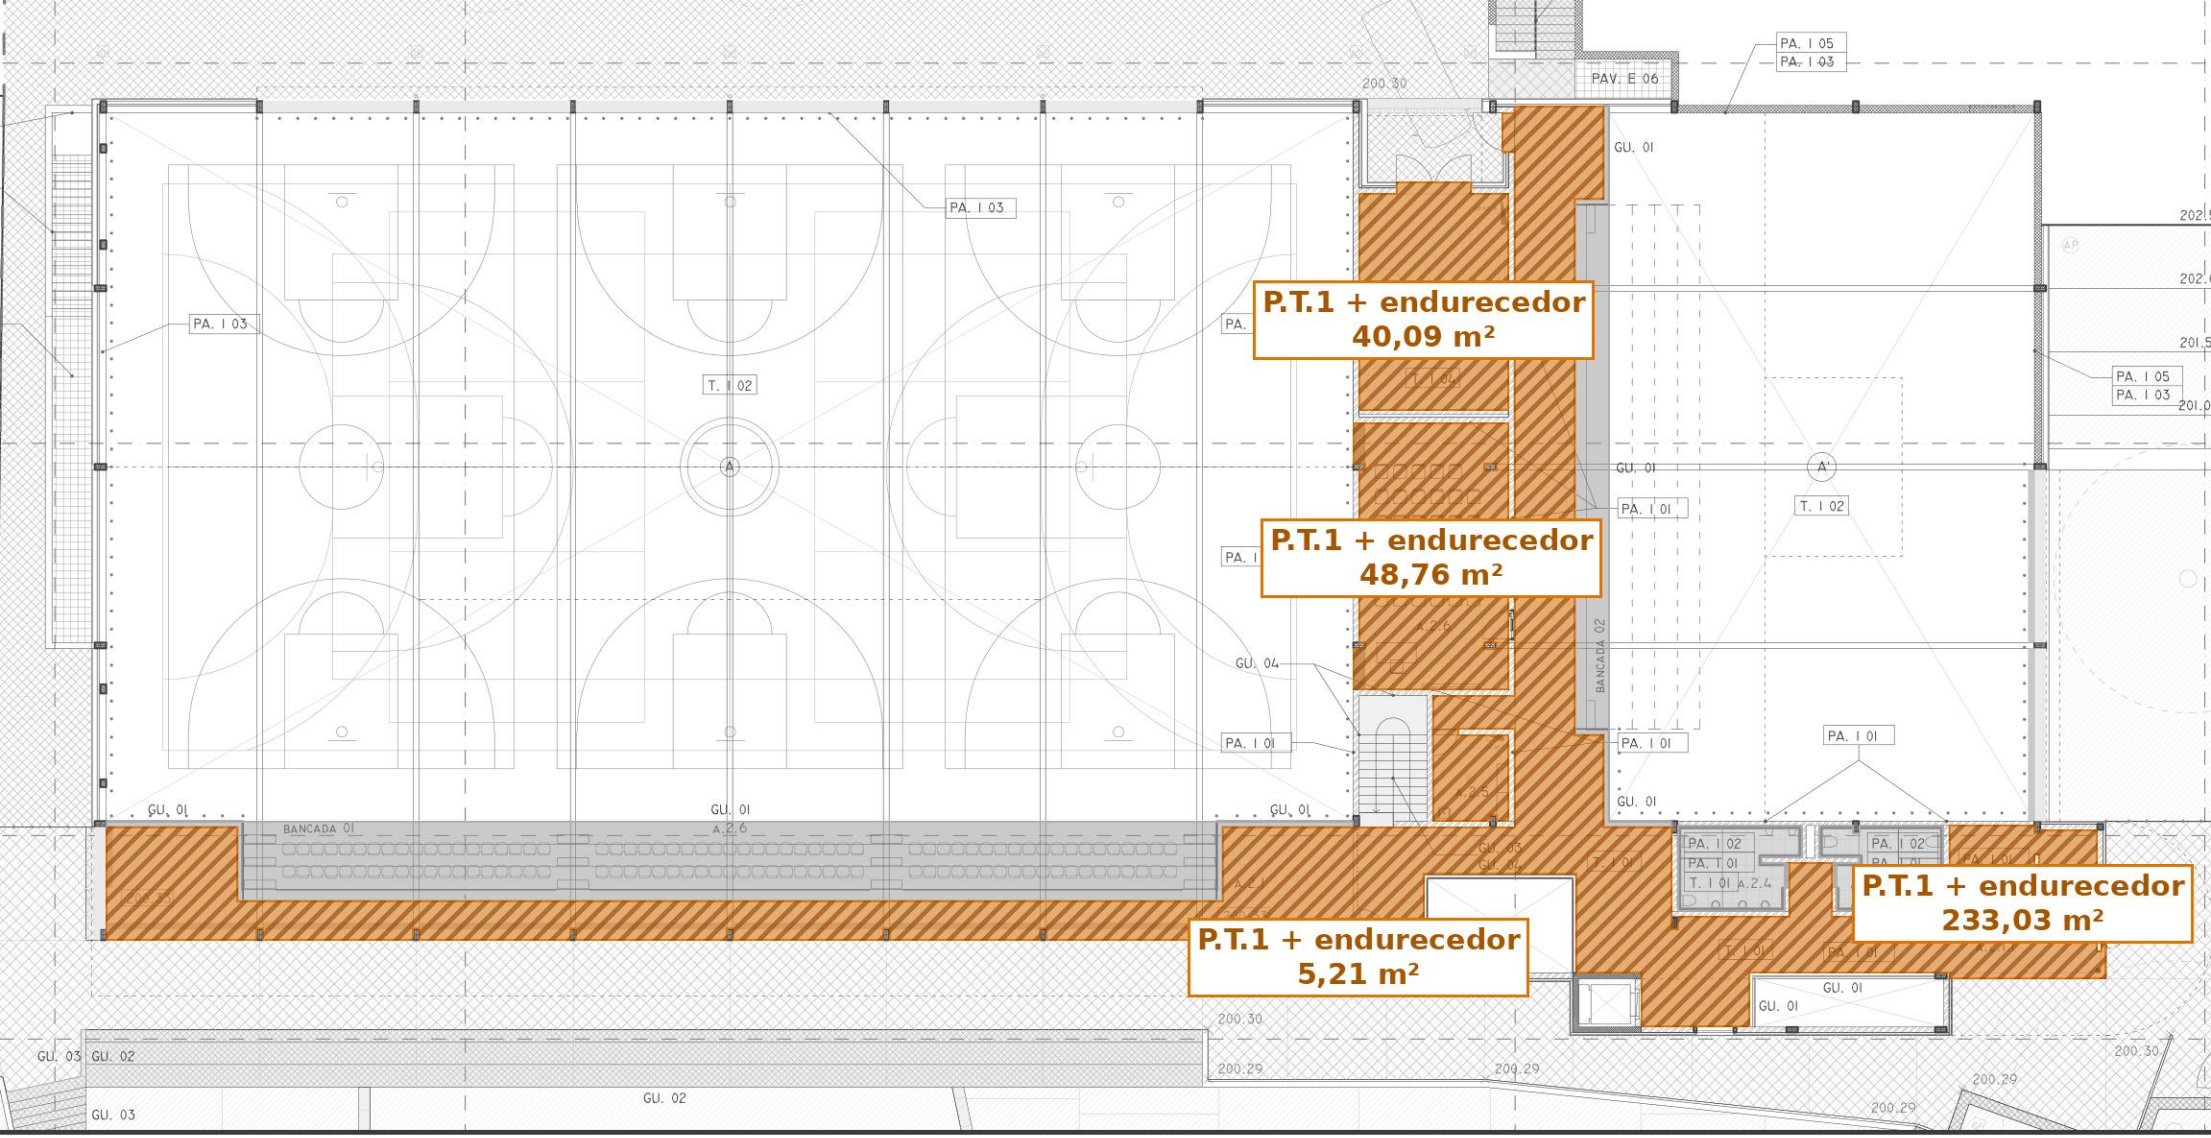

P.T.1 E ENDURECEDOR DE SUPERFÍCIE — PISO 02

Projeto de acabamentos 3.2 — folha 3.2.3 Piso 02, esc. 1:200. Áreas dos polígonos desenhados.

▭	**P.T.1**	Pavimento térreo com caixa de brita de 0,22 m — zonas com pavimento PAV I 02 (betão armado com endurecedor): 327,09 m² + soleiras dentro destas zonas 19,98 m² = 347,07 m² (art. 2.3.14.1)
▨	**ENDUR.**	Endurecedor de superfície de quartzo 4 kg/m² — mesma zona do P.T.1: 347,07 m² (art. 2.6.3) — às riscas
▭	**TOTAL**	P.T.1 e endurecedor, Piso 01 + Piso 02 = 265,84 + 347,07 = 612,92 m²
▭	**OUTROS**	Restantes pavimentos interiores do Piso 02 (PAV I 03 e PAV I 04) — não contam

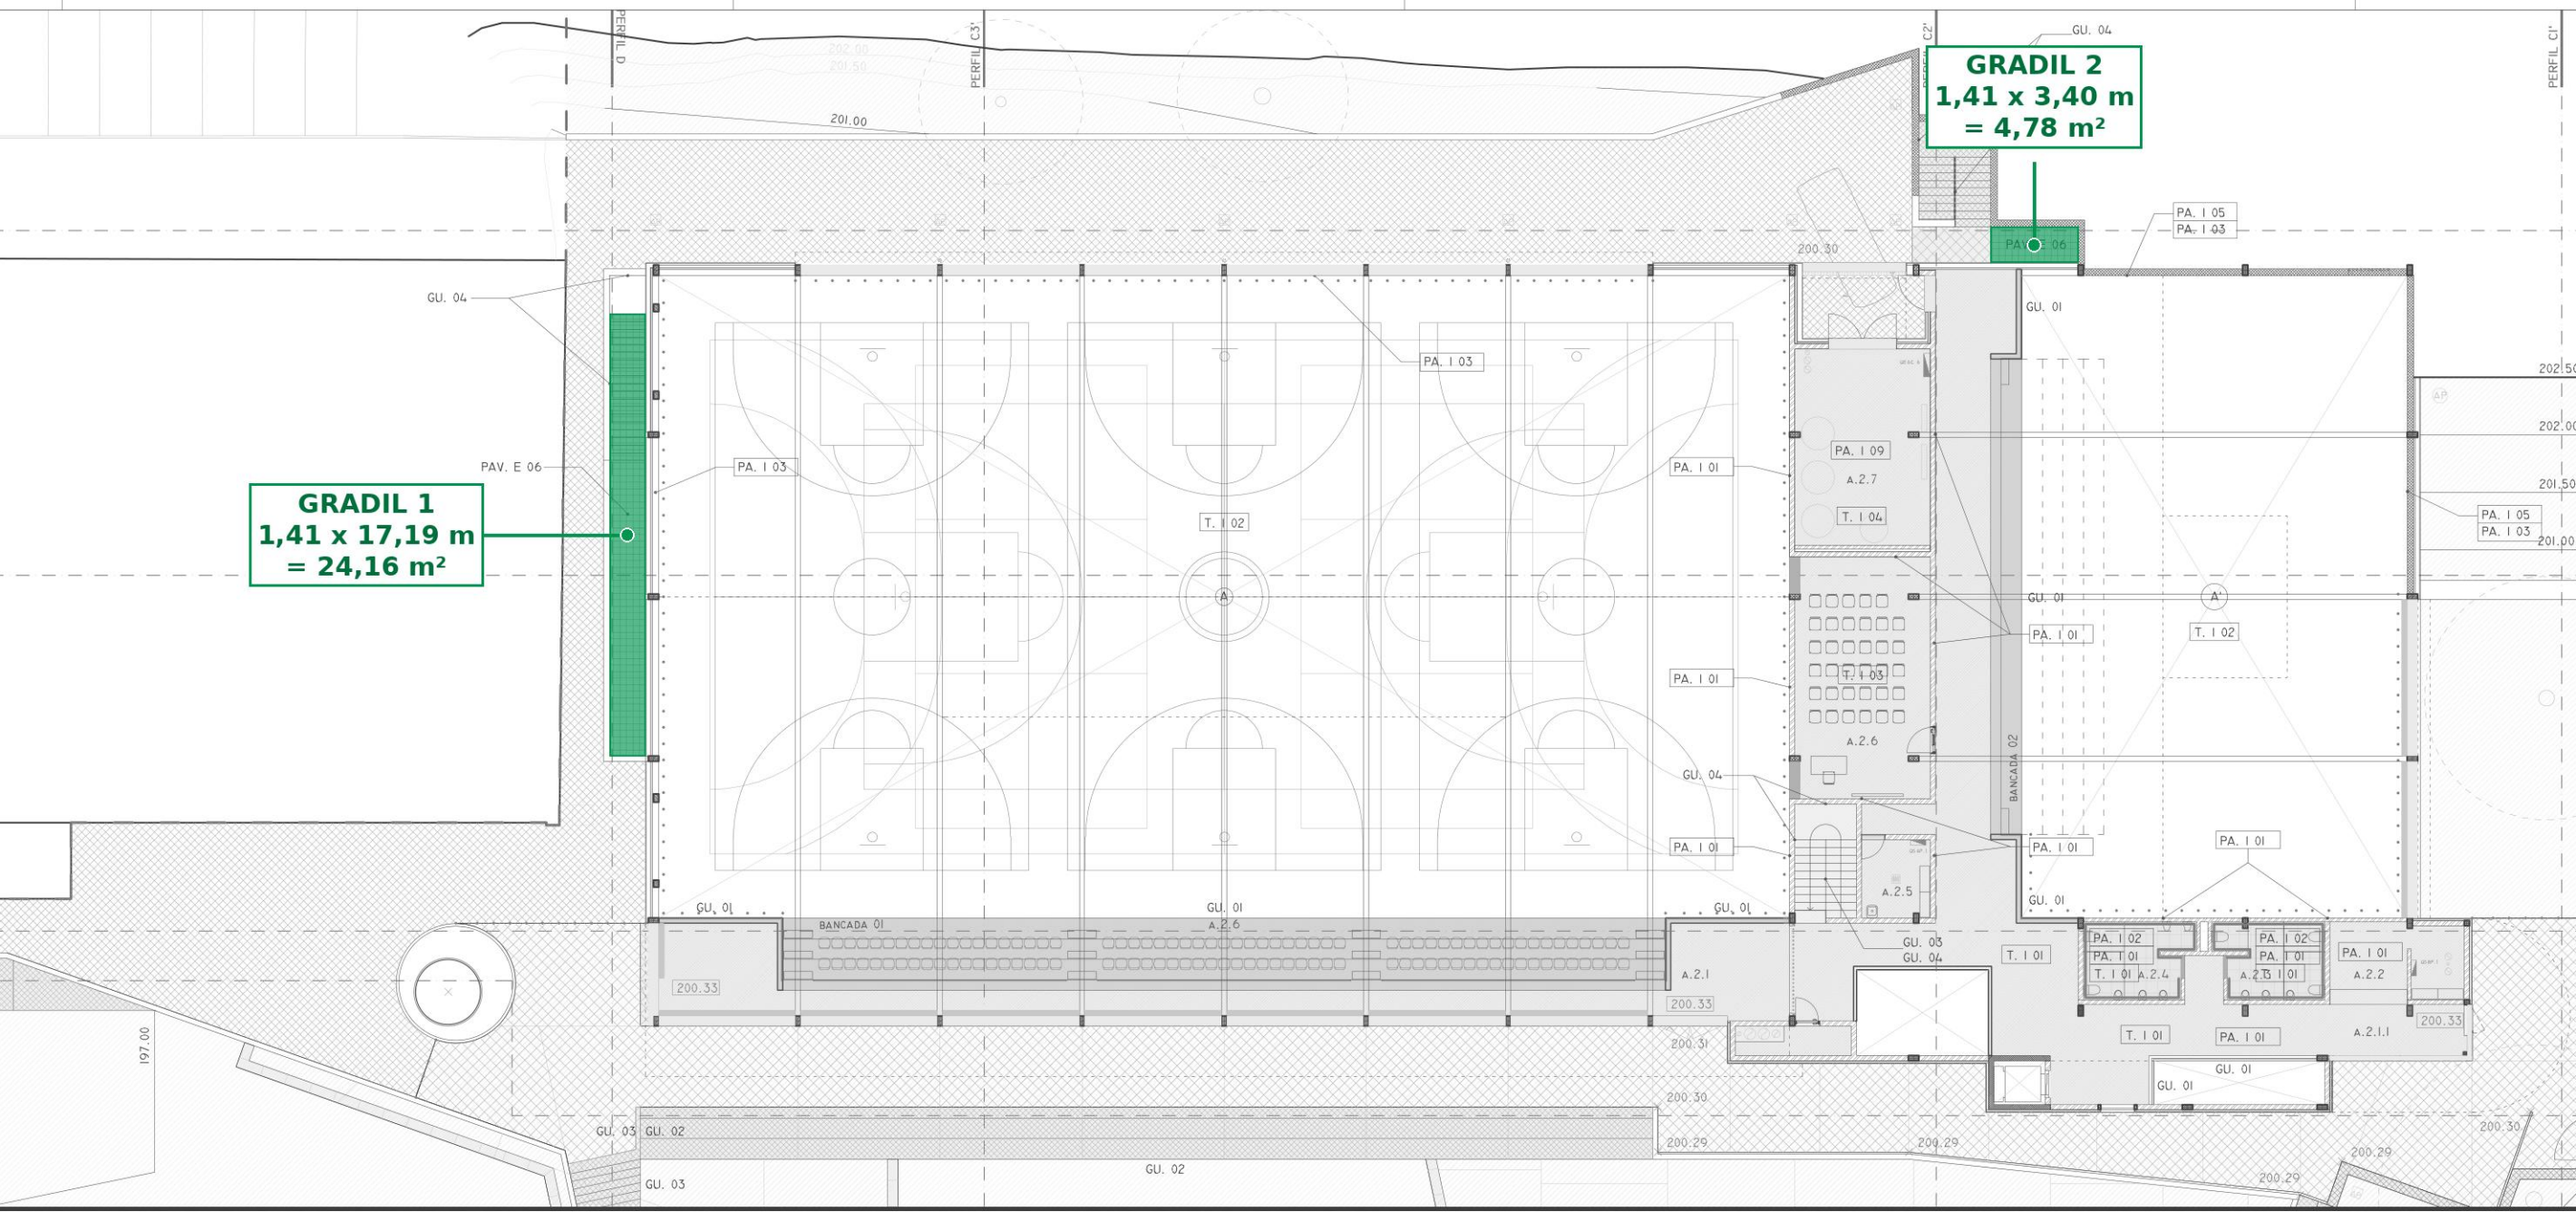

GRADIL — PISO 02

Projeto de acabamentos 3.2 — folha 3.2.3 Piso 02, esc. 1:200. Zonas com a trama PAV E 06 (gradil de aço).

GRADIL — Gradil para pavimento (0,30 m de espessura, malha 0,030 x 0,030 m, 27 kg/m², aço ST 37.2) — zonas PAV E 06 da planta de acabamentos: 24,16 + 4,78 = 28,94 m² (art. 2.4.4)