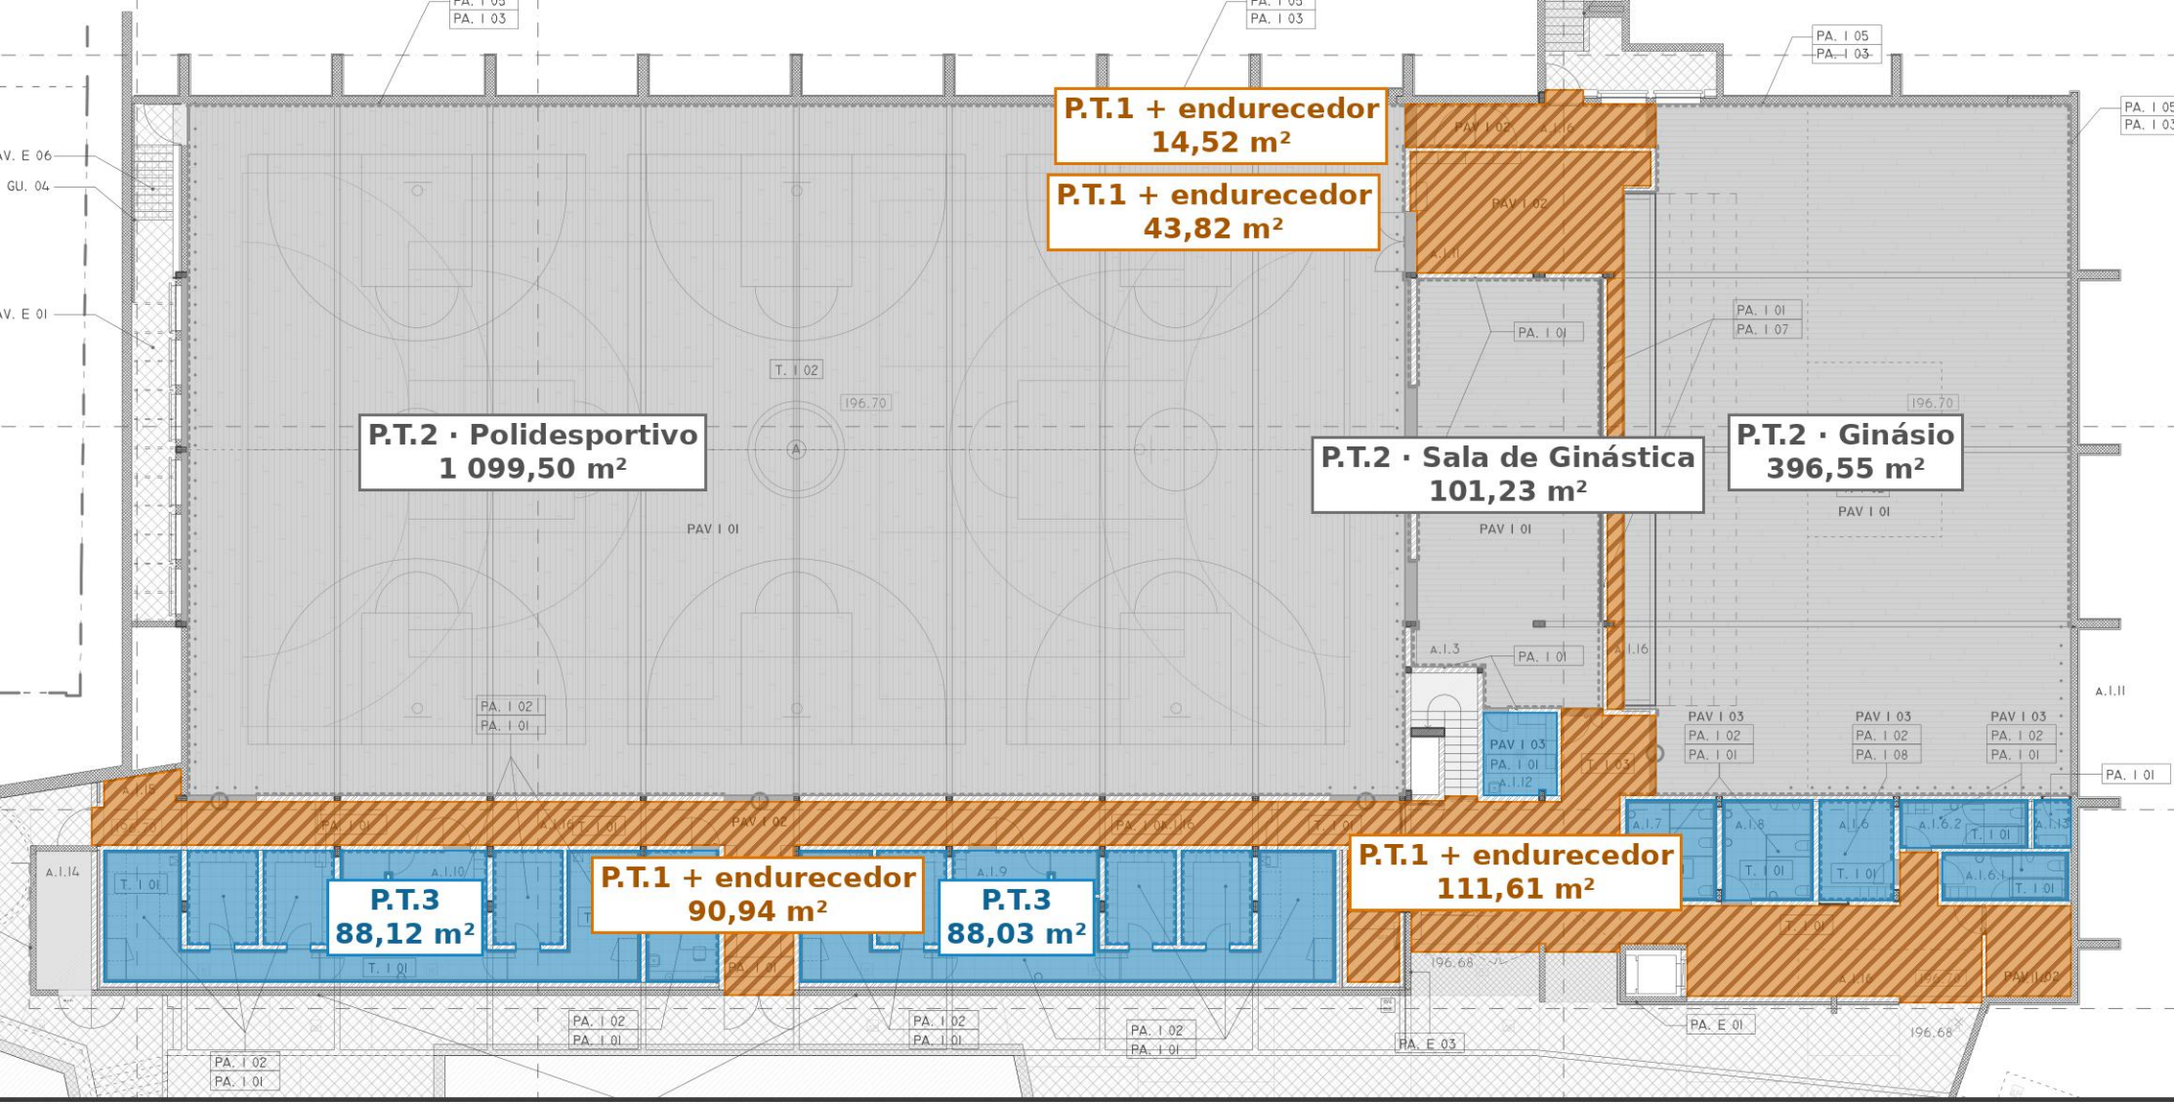


PAVIMENTO TÉRREO E ENDURECEDOR DE SUPERFÍCIE — PISO 01


Projeto de acabamentos 3.2 — folha 3.2.2 Piso 01, esc. 1:200. Áreas dos polígonos desenhados.

P.T.1 — Pavimento térreo com caixa de brita de 0,22 m — zonas com pavimento PAV I 02 (betão armado com endurecedor): 260,89 m² + soleiras dentro destas zonas 4,96 m² = 265,84 m² (art. 2.3.14.1)

ENDUR. — Endurecedor de superfície de quartzo 4 kg/m² — mesma zona do P.T.1: 265,84 m² (art. 2.6.3) — às riscas

P.T.3 — Pavimento térreo com caixa de brita de 0,17 m — zonas com pavimento PAV I 03 (balneários, I.S., gabinete médico, arrumos): 249,38 m² (art. 2.3.14.3)

P.T.2 — Pavimento térreo com caixa de brita de 0,15 m — zonas com pavimento desportivo PAV I 01: 1 597,28 m² (art. 2.3.14.2)

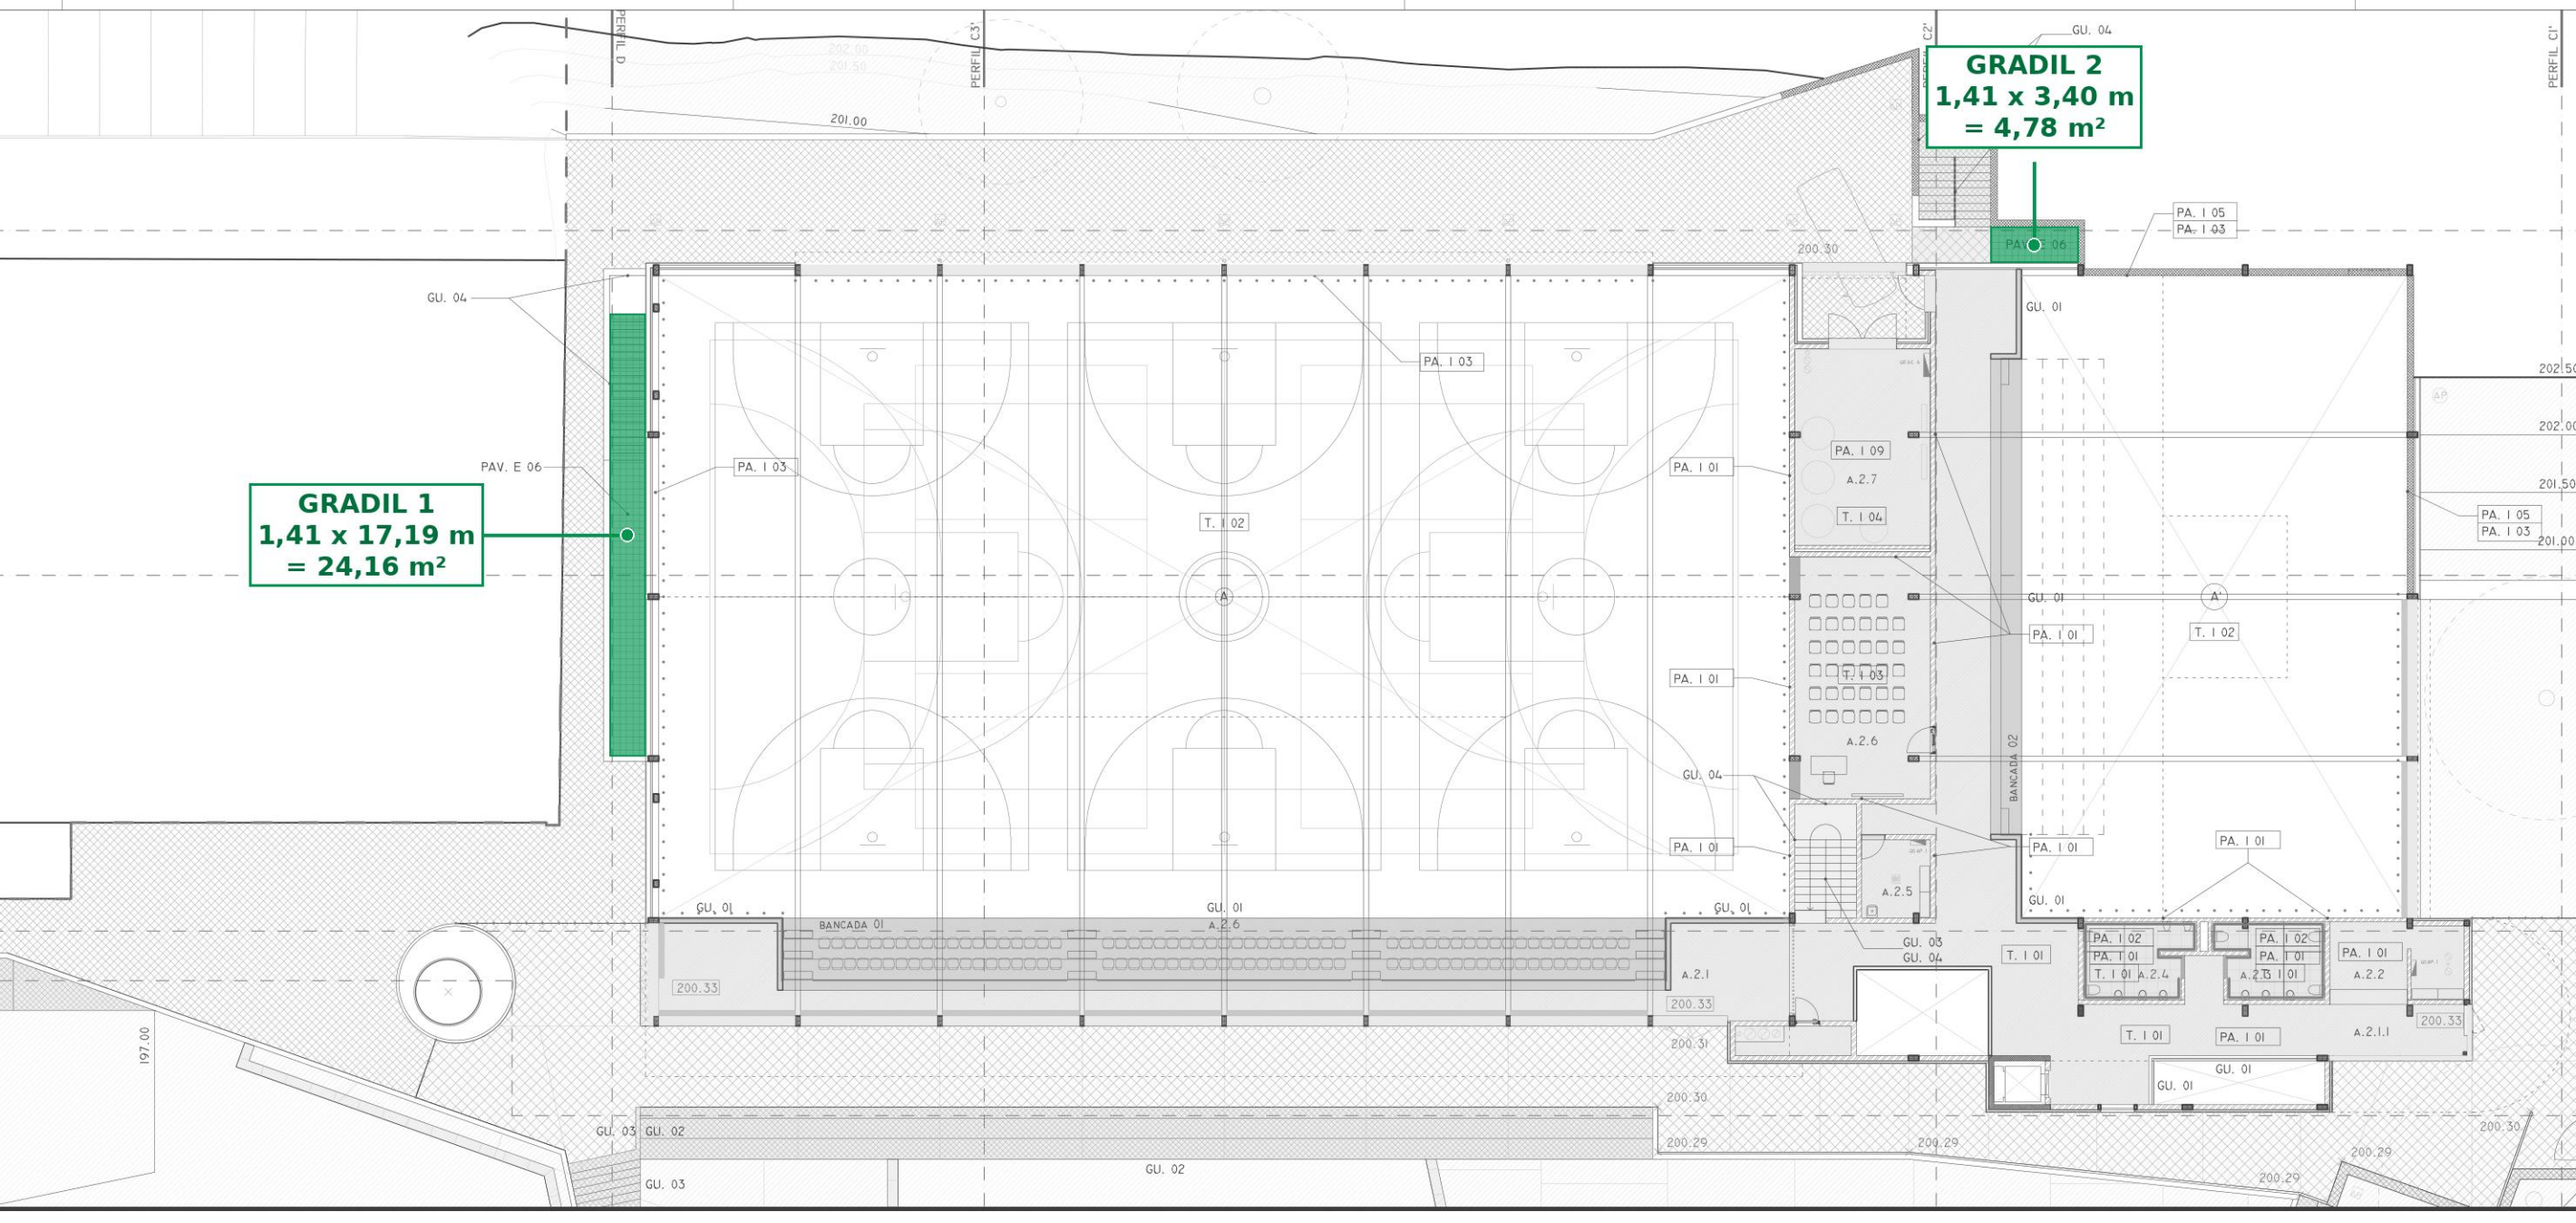

GRADIL — PISO 02

Projeto de acabamentos 3.2 — folha 3.2.3 Piso 02, esc. 1:200. Zonas com a trama PAV E 06 (gradil de aço).

GRADIL — Gradil para pavimento (0,30 m de espessura, malha 0,030 x 0,030 m, 27 kg/m², aço ST 37.2) — zonas PAV E 06 da planta de acabamentos: 24,16 + 4,78 = 28,94 m² (art. 2.4.4)