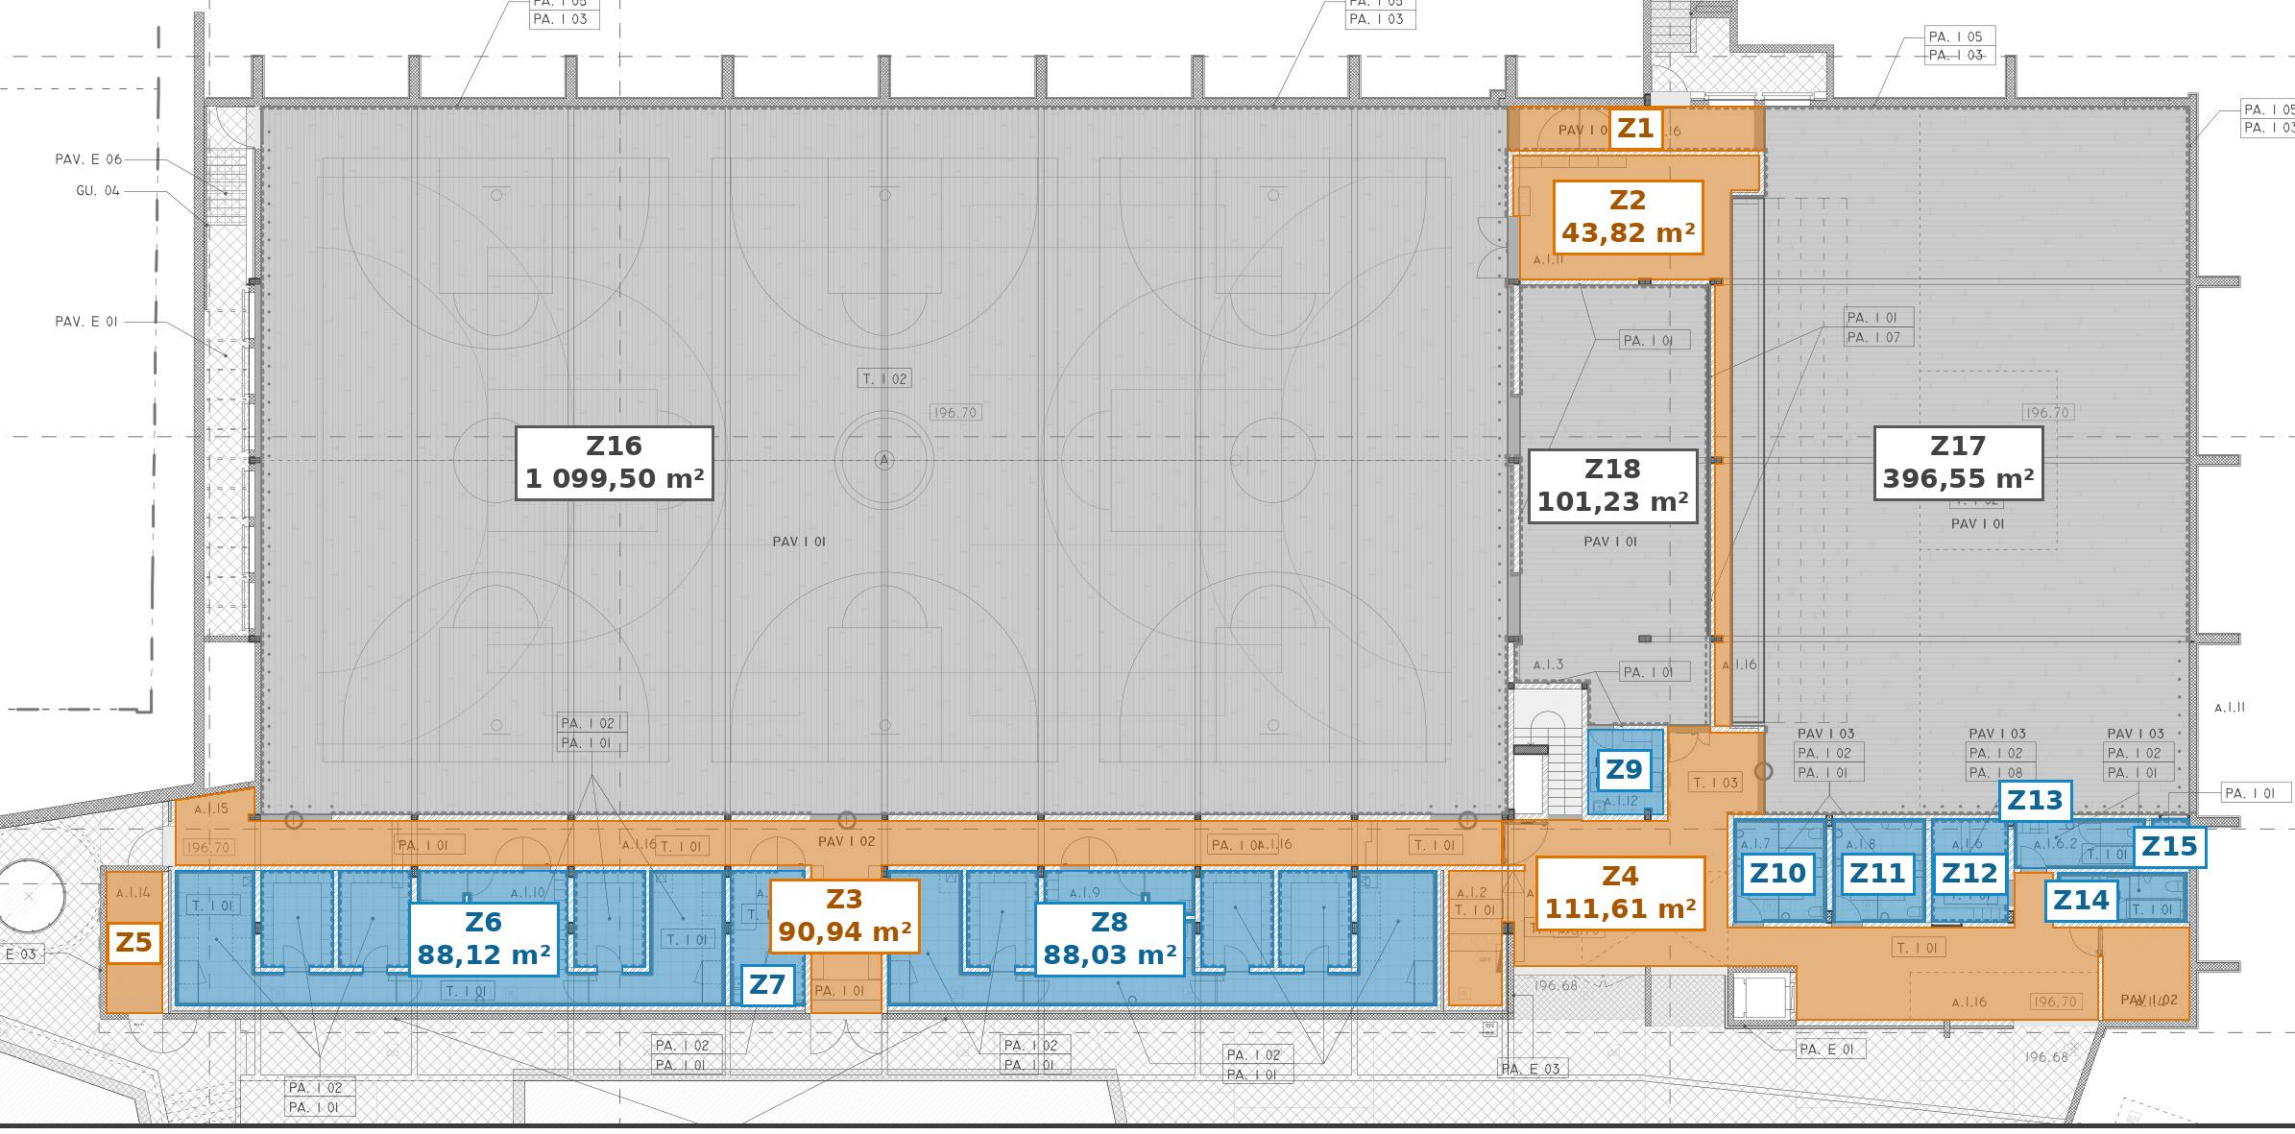



## PAVIMENTO TÉRREO (art. 2.3.14) — ZONAS DO PISO 01


Laje assente sobre o terreno natural: só no Piso 01 (cota 196,70). Projeto de acabamentos 3.2, folha 3.2.2 (esc. 1:200) e Quadro de áreas.

| Zona | Espaços (código e designação do Quadro de áreas) | Área desenhada | Quadro de áreas |
|---|---|---|---|
| **P.T.1 — caixa de brita 0,22 m (art. 2.3.14.1) — pavimento PAV I 02** | | | |
| **Z1** | A.1.16 Circulação — entrada norte (entre Polidesportivo e Ginásio) | 14,52 m² | circ. |
| **Z2** | A.1.11 Arrumos Educação Física (Gimnod.) + A.1.16 corredor entre a Sala de Ginástica e o Ginásio | 43,82 m² | 58,00 + circ. |
| **Z3** | A.1.16 Circulação sul (corredor dos balneários) + A.1.15 Ecoponto + A.1.1.1 Átrio secundário | 90,94 m² | 2,50 + 13,50 + circ. |
| **Z4** | A.1.1 Átrio / entrada + A.1.2 Receção + A.1.4 Arrumo geral 01 + A.1.16 circulação nascente | 111,61 m² | 50,00 + 9,50 + 10,00 + circ. |
| **Z5** | A.1.14 Arrumos campo exterior (trama cinzenta mais escura) | 9,98 m² | 10,00 |
| | **Total P.T.1** | **270,87 m²** | **281,50 *** |
| **P.T.3 — caixa de brita 0,17 m (art. 2.3.14.3) — pavimento PAV I 03** | | | |
| **Z6** | A.1.10 Bloco balneário masculino | 88,12 m² | 89,00 |
| **Z7** | A.1.5 Gabinete médico | 12,66 m² | 13,00 |
| **Z8** | A.1.9 Bloco balneário feminino | 88,03 m² | 89,00 |
| **Z9** | A.1.12 Arrumo geral 02 | 8,03 m² | 8,00 |
| **Z10** | A.1.7 I.S. alunos masculino | 12,01 m² | 12,00 |
| **Z11** | A.1.8 I.S. alunos feminino | 12,01 m² | 12,00 |
| **Z12** | A.1.6 Sala de professores | 9,91 m² | 10,00 |
| **Z13** | A.1.6.2 Balneário professores feminino | 8,20 m² | 8,00 |
| **Z14** | A.1.6.1 Balneário professores masculino | 8,02 m² | 8,00 |
| **Z15** | A.1.13 Arrumos limpeza | 2,39 m² | 2,50 |
| | **Total P.T.3** | **249,38 m²** | **251,50** |
| **P.T.2 — caixa de brita 0,15 m (art. 2.3.14.2) — pavimento PAV I 01** | | | |
| **Z16** | A Polidesportivo | 1 099,50 m² | 1 100,00 |
| **Z17** | A' Ginásio | 396,55 m² | 375,00 |
| **Z18** | A.1.3 Sala de Ginástica | 101,23 m² | 107,00 |
| | **Total P.T.2** | **1 597,28 m²** | **1 582,00** |

* P.T.1 no Quadro de áreas: espaços A.1.1, A.1.1.1, A.1.2, A.1.4, A.1.11 (gimnod.), A.1.14, A.1.15 e Área de circulação (128,00). "circ." = parte da Área de circulação.

Áreas desenhadas = área dos polígonos de pavimento da planta (sem paredes nem soleiras). A zona P.T.1 é também a zona do endurecedor de superfície (art. 2.6.3) no Piso 01.


A.1.11 Arrumos Ed. Física (ginásio), 25,00 m² no Quadro: a etiqueta está fora da parede nascente do Ginásio e não há espaço desenhado; a diferença da Z17 (396,55 contra 375,00) deve corresponder a

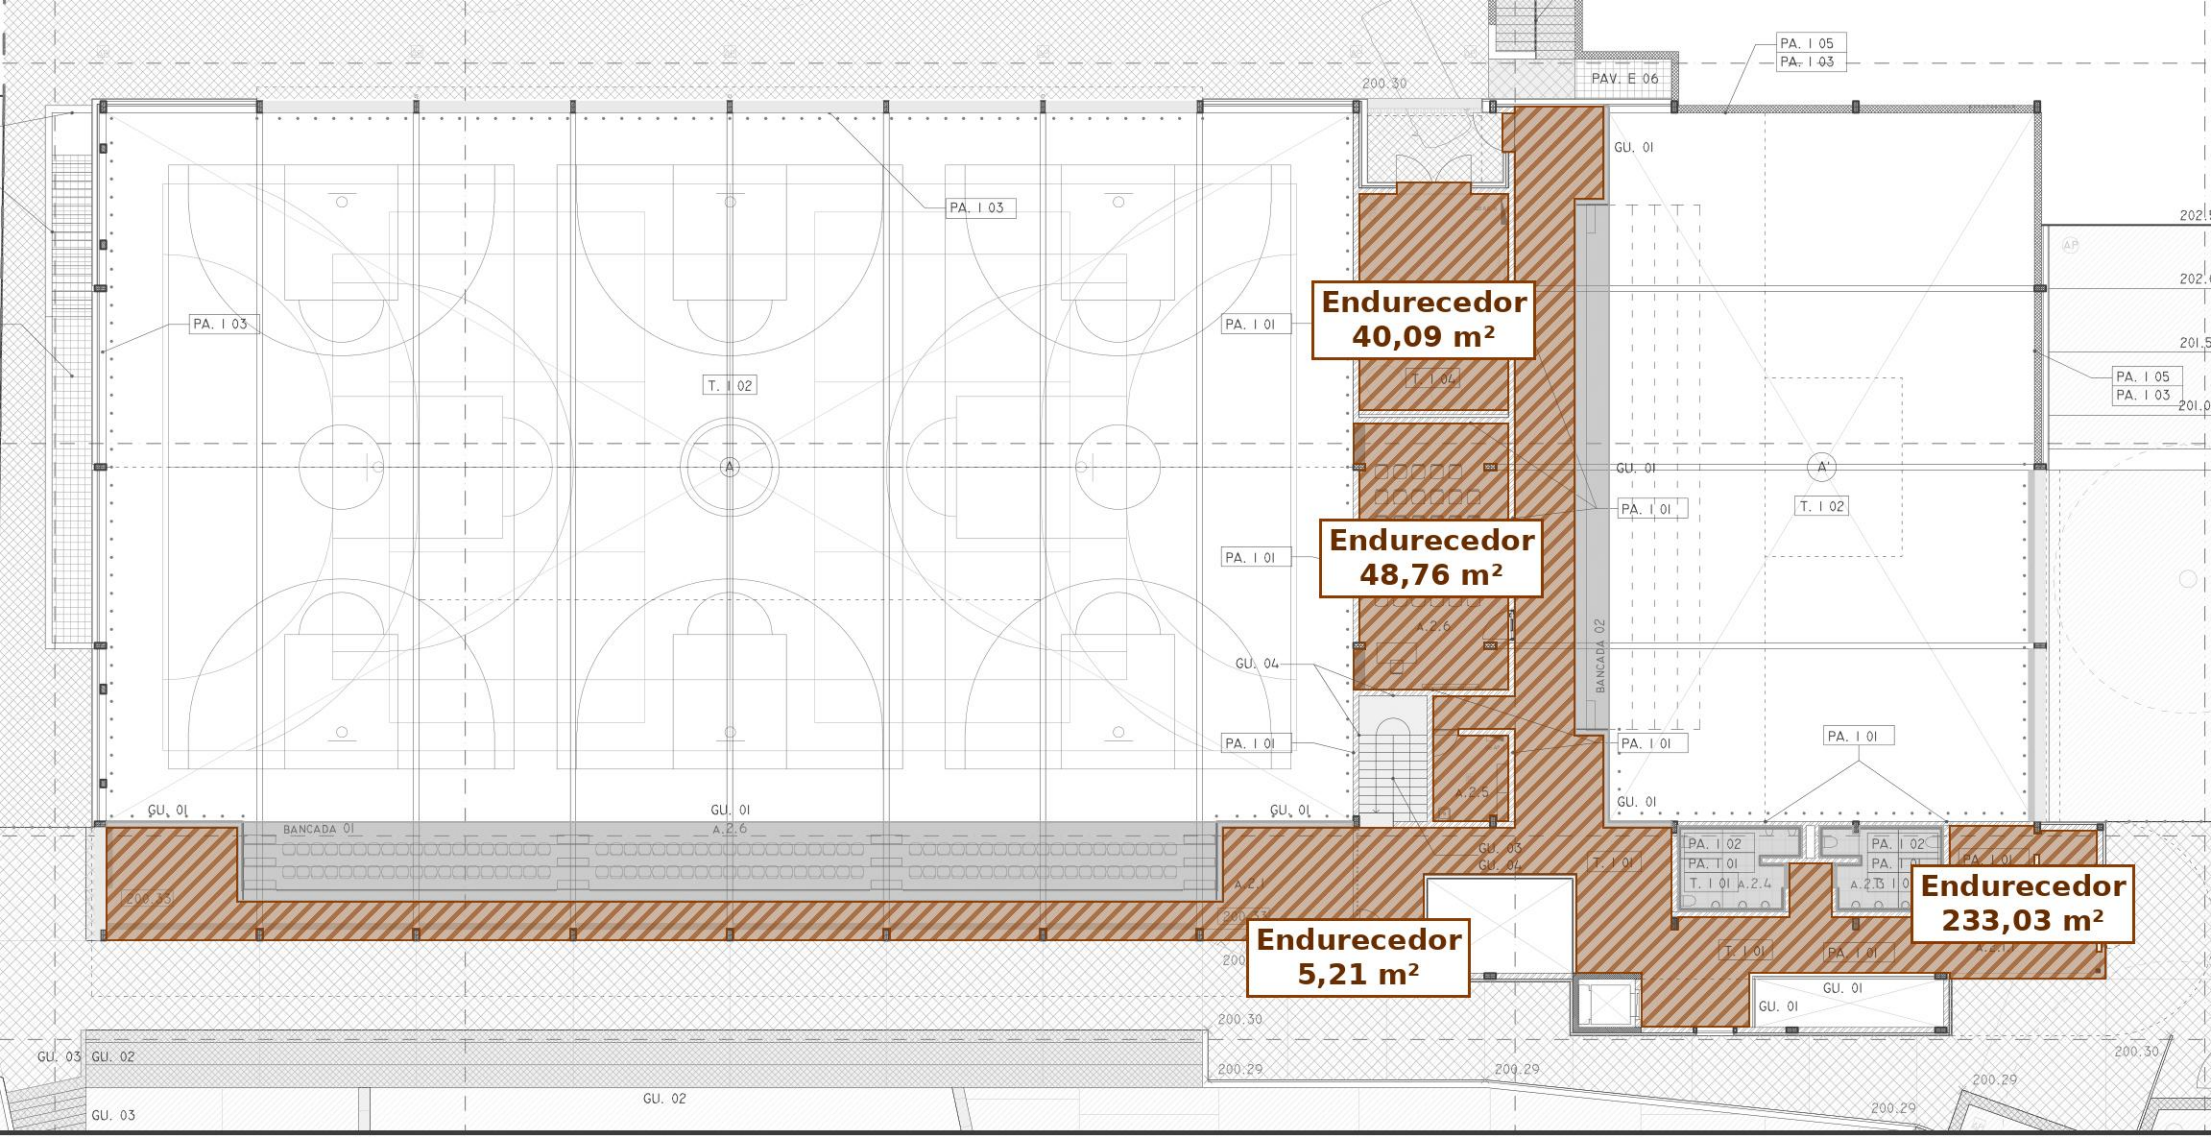


# ENDURECEDOR DE SUPERFÍCIE — PISO 02

Projeto de acabamentos 3.2 — folha 3.2.3 Piso 02, esc. 1:200. Áreas dos polígonos desenhados.

| | | |
|---|---|---|
| ▨ | **ENDUR.** | Endurecedor de superfície de quartzo 4 kg/m² — zonas com pavimento PAV I 02 (betão armado com endurecedor): 327,09 m² + soleiras dentro destas zonas 19,98 m² = 347,07 m² (art. 2.6.3) — às riscas |
| ▭ | **NOTA** | Sem pavimento térreo (P.T.): estas zonas ficam por cima de espaços do Piso 01 (laje), não assentam sobre o terreno natural |
| ▭ | **OUTROS** | Restantes pavimentos interiores do Piso 02 (PAV I 03 e PAV I 04) — não contam |

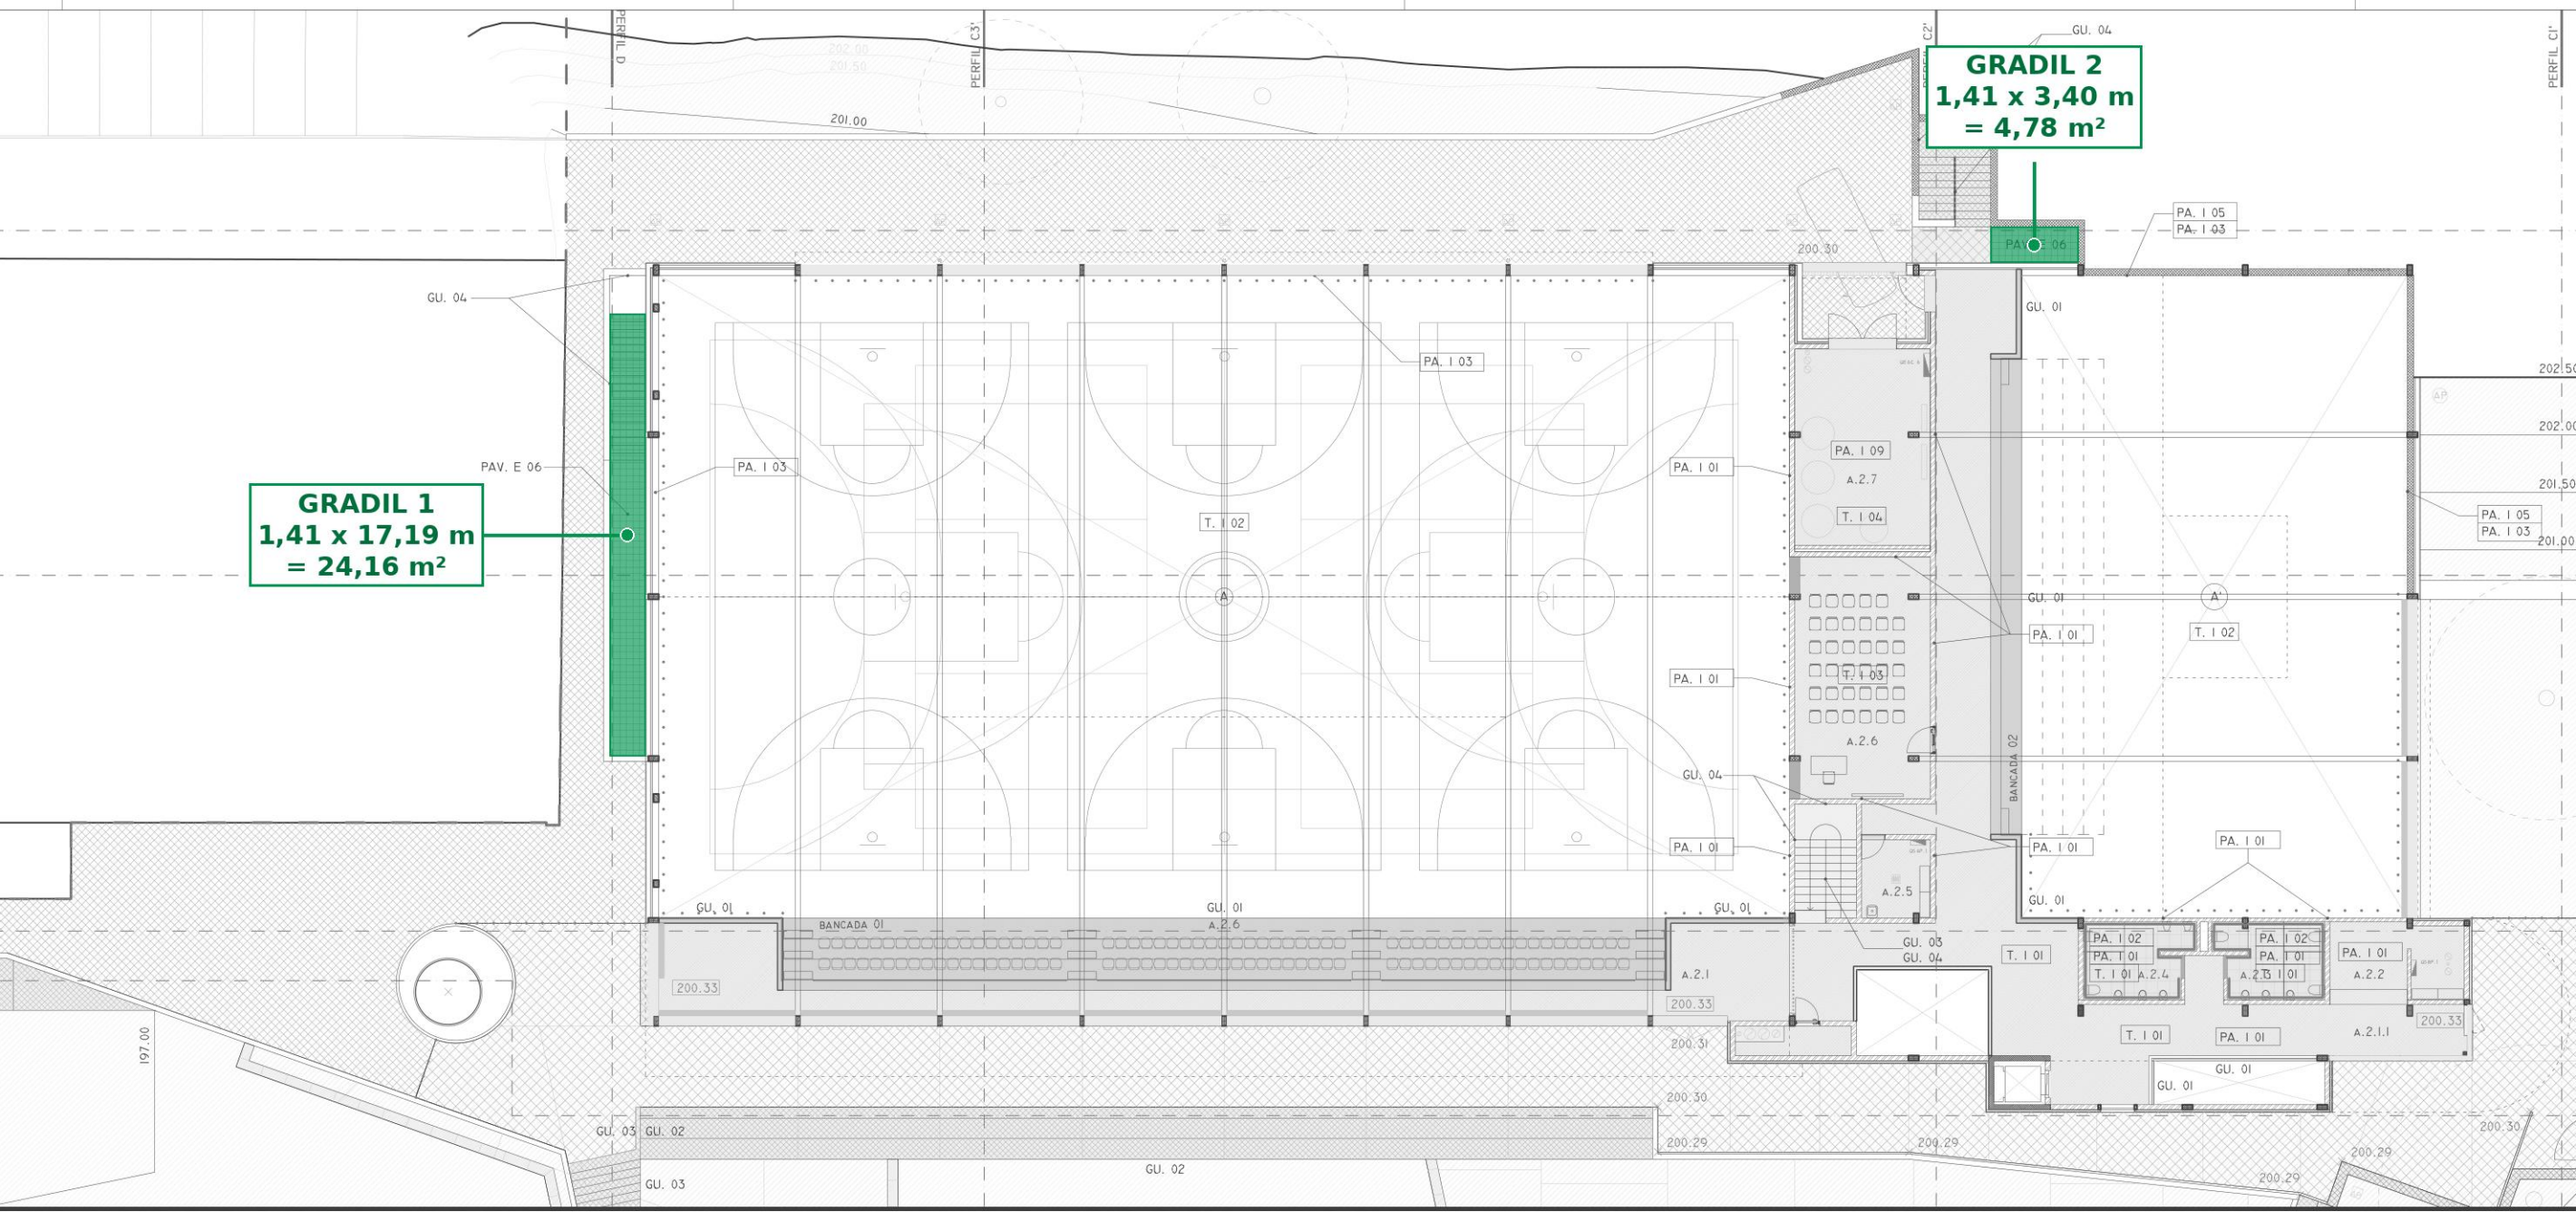


# GRADIL — PISO 02

Projeto de acabamentos 3.2 — folha 3.2.3 Piso 02, esc. 1:200. Zonas com a trama PAV E 06 (gradil de aço).

**GRADIL** — Gradil para pavimento (0,30 m de espessura, malha 0,030 x 0,030 m, 27 kg/m², aço ST 37.2) — zonas PAV E 06 da planta de acabamentos: 24,16 + 4,78 = 28,94 m² (art. 2.4.4)