
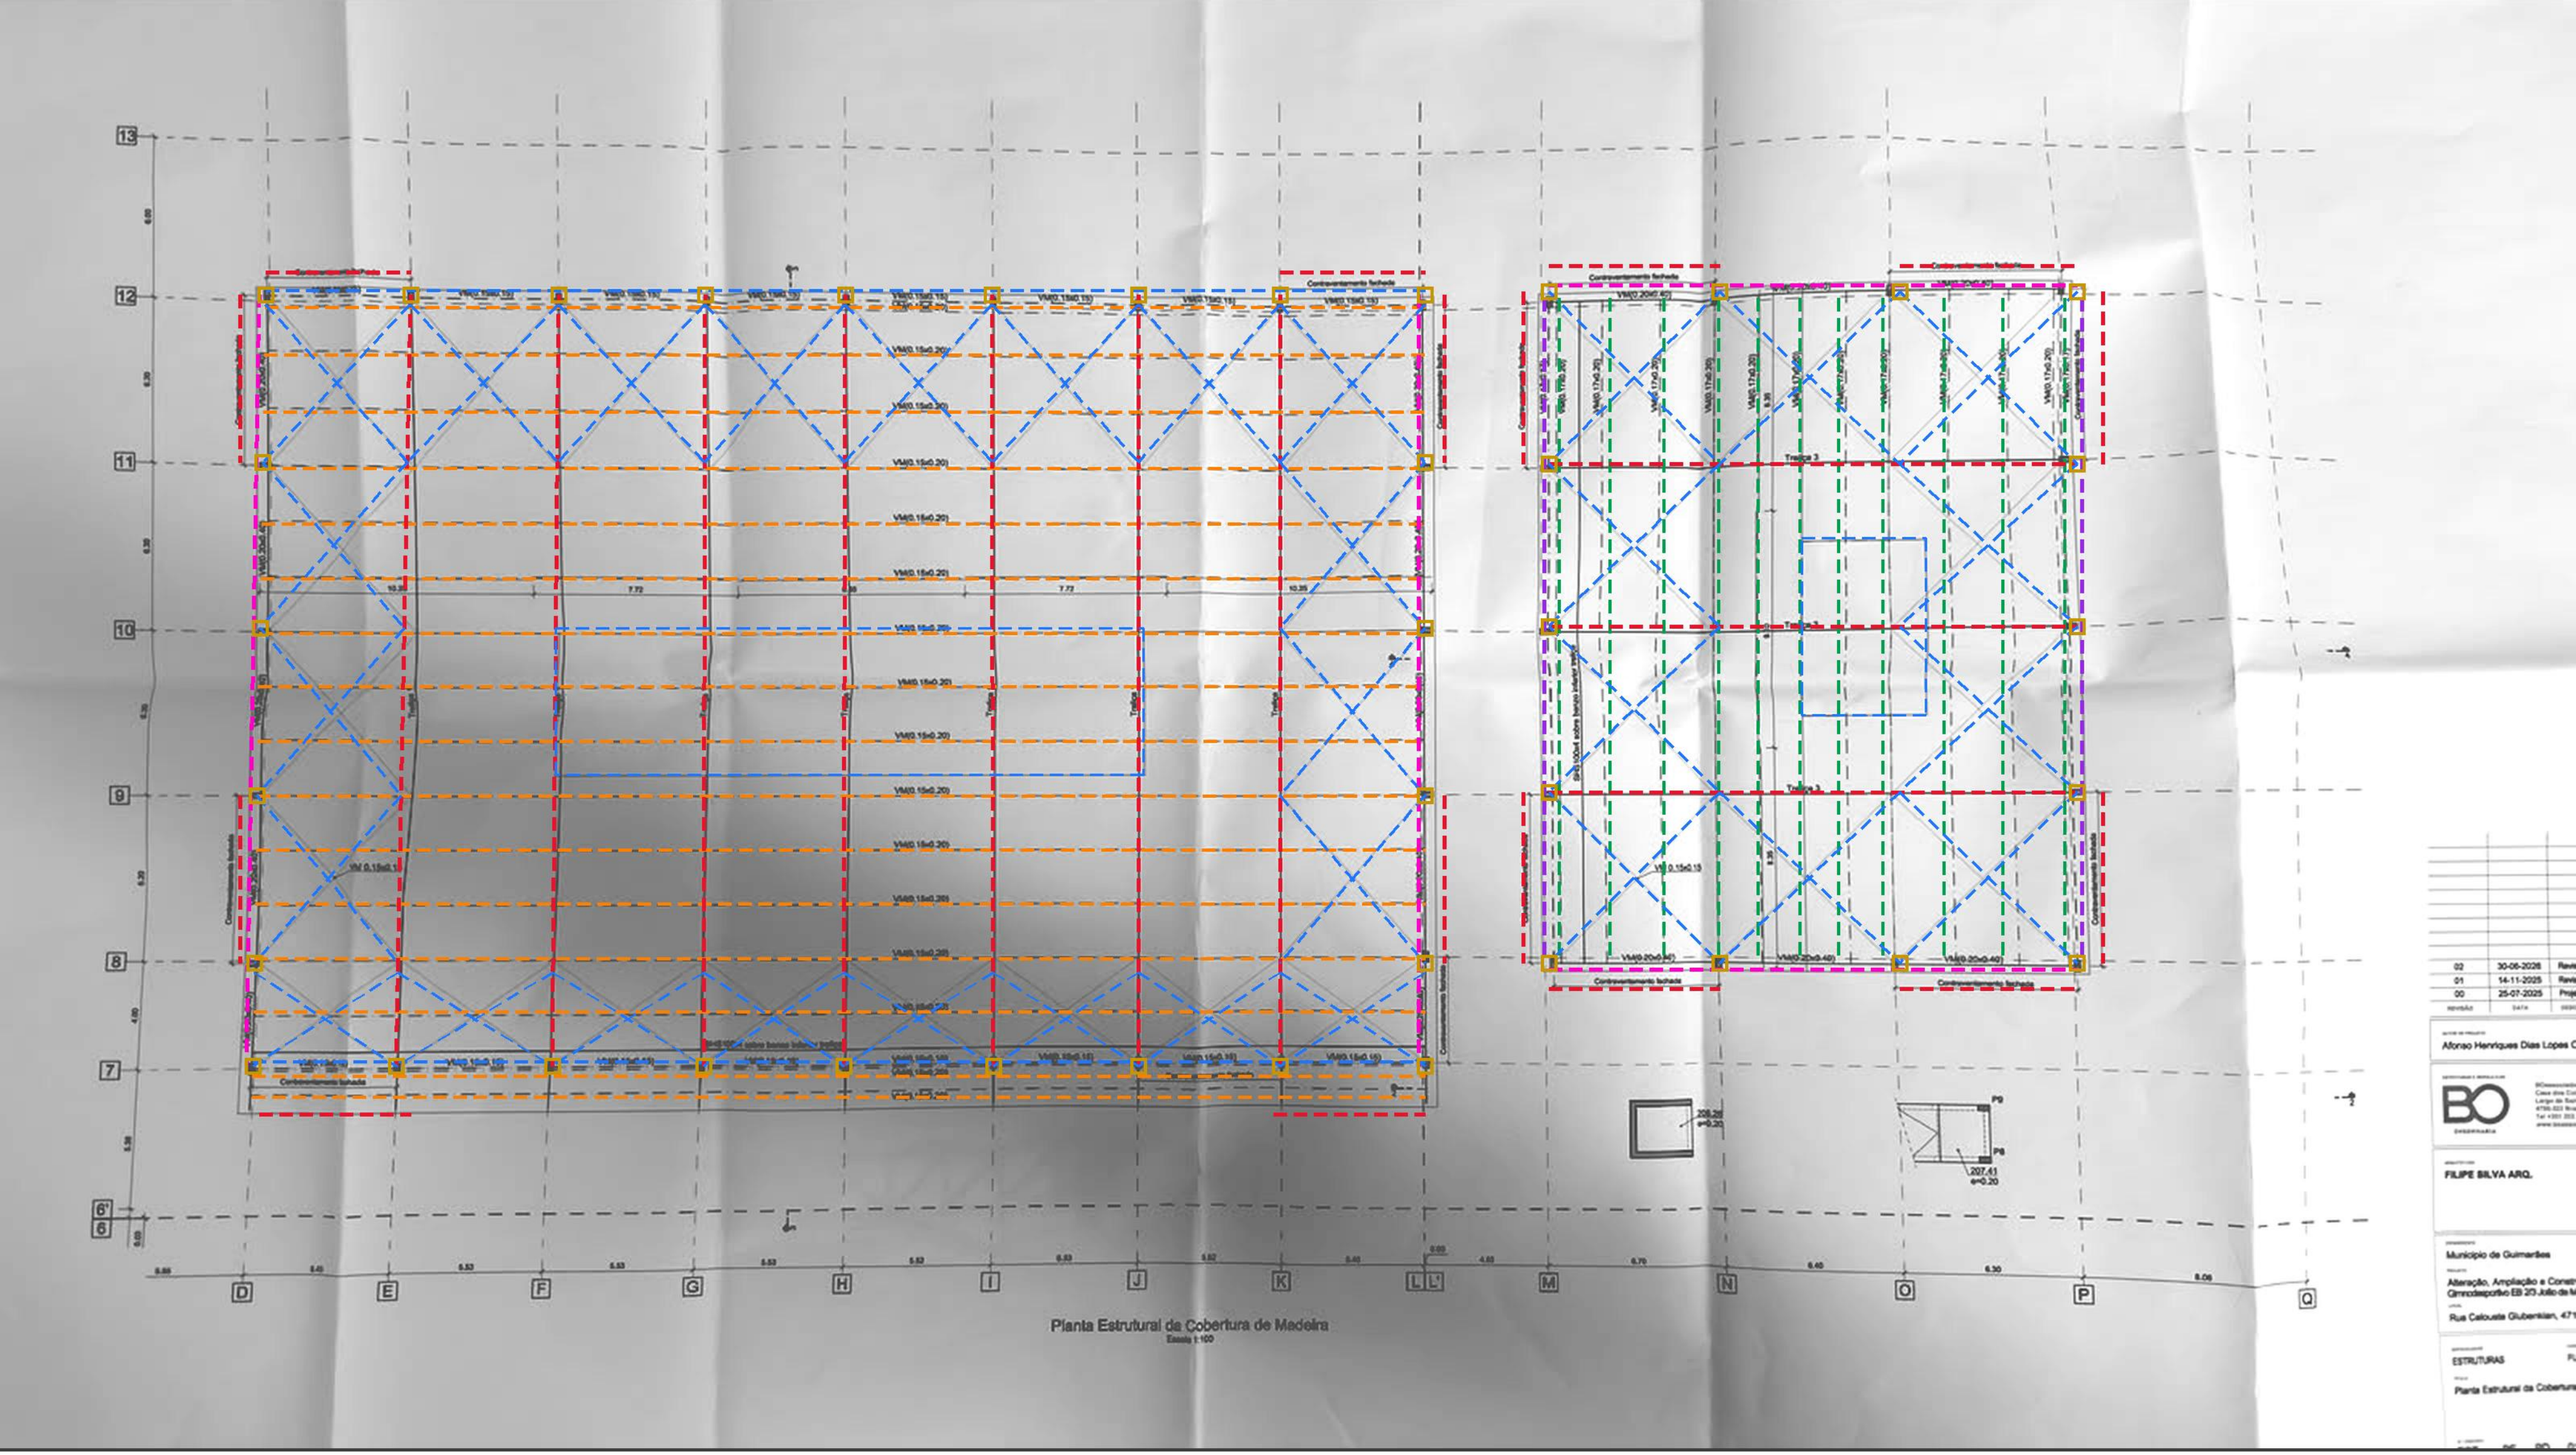


Planta Estrutural da Cobertura de Madeira


- VM 0.15x0.15
- VM 0.15x0.20
- VM 0.17x0.17
- VM 0.17x0.20
- VM 0.20x0.20
- VM 0.20x0.40
- PM 0.20x0.40

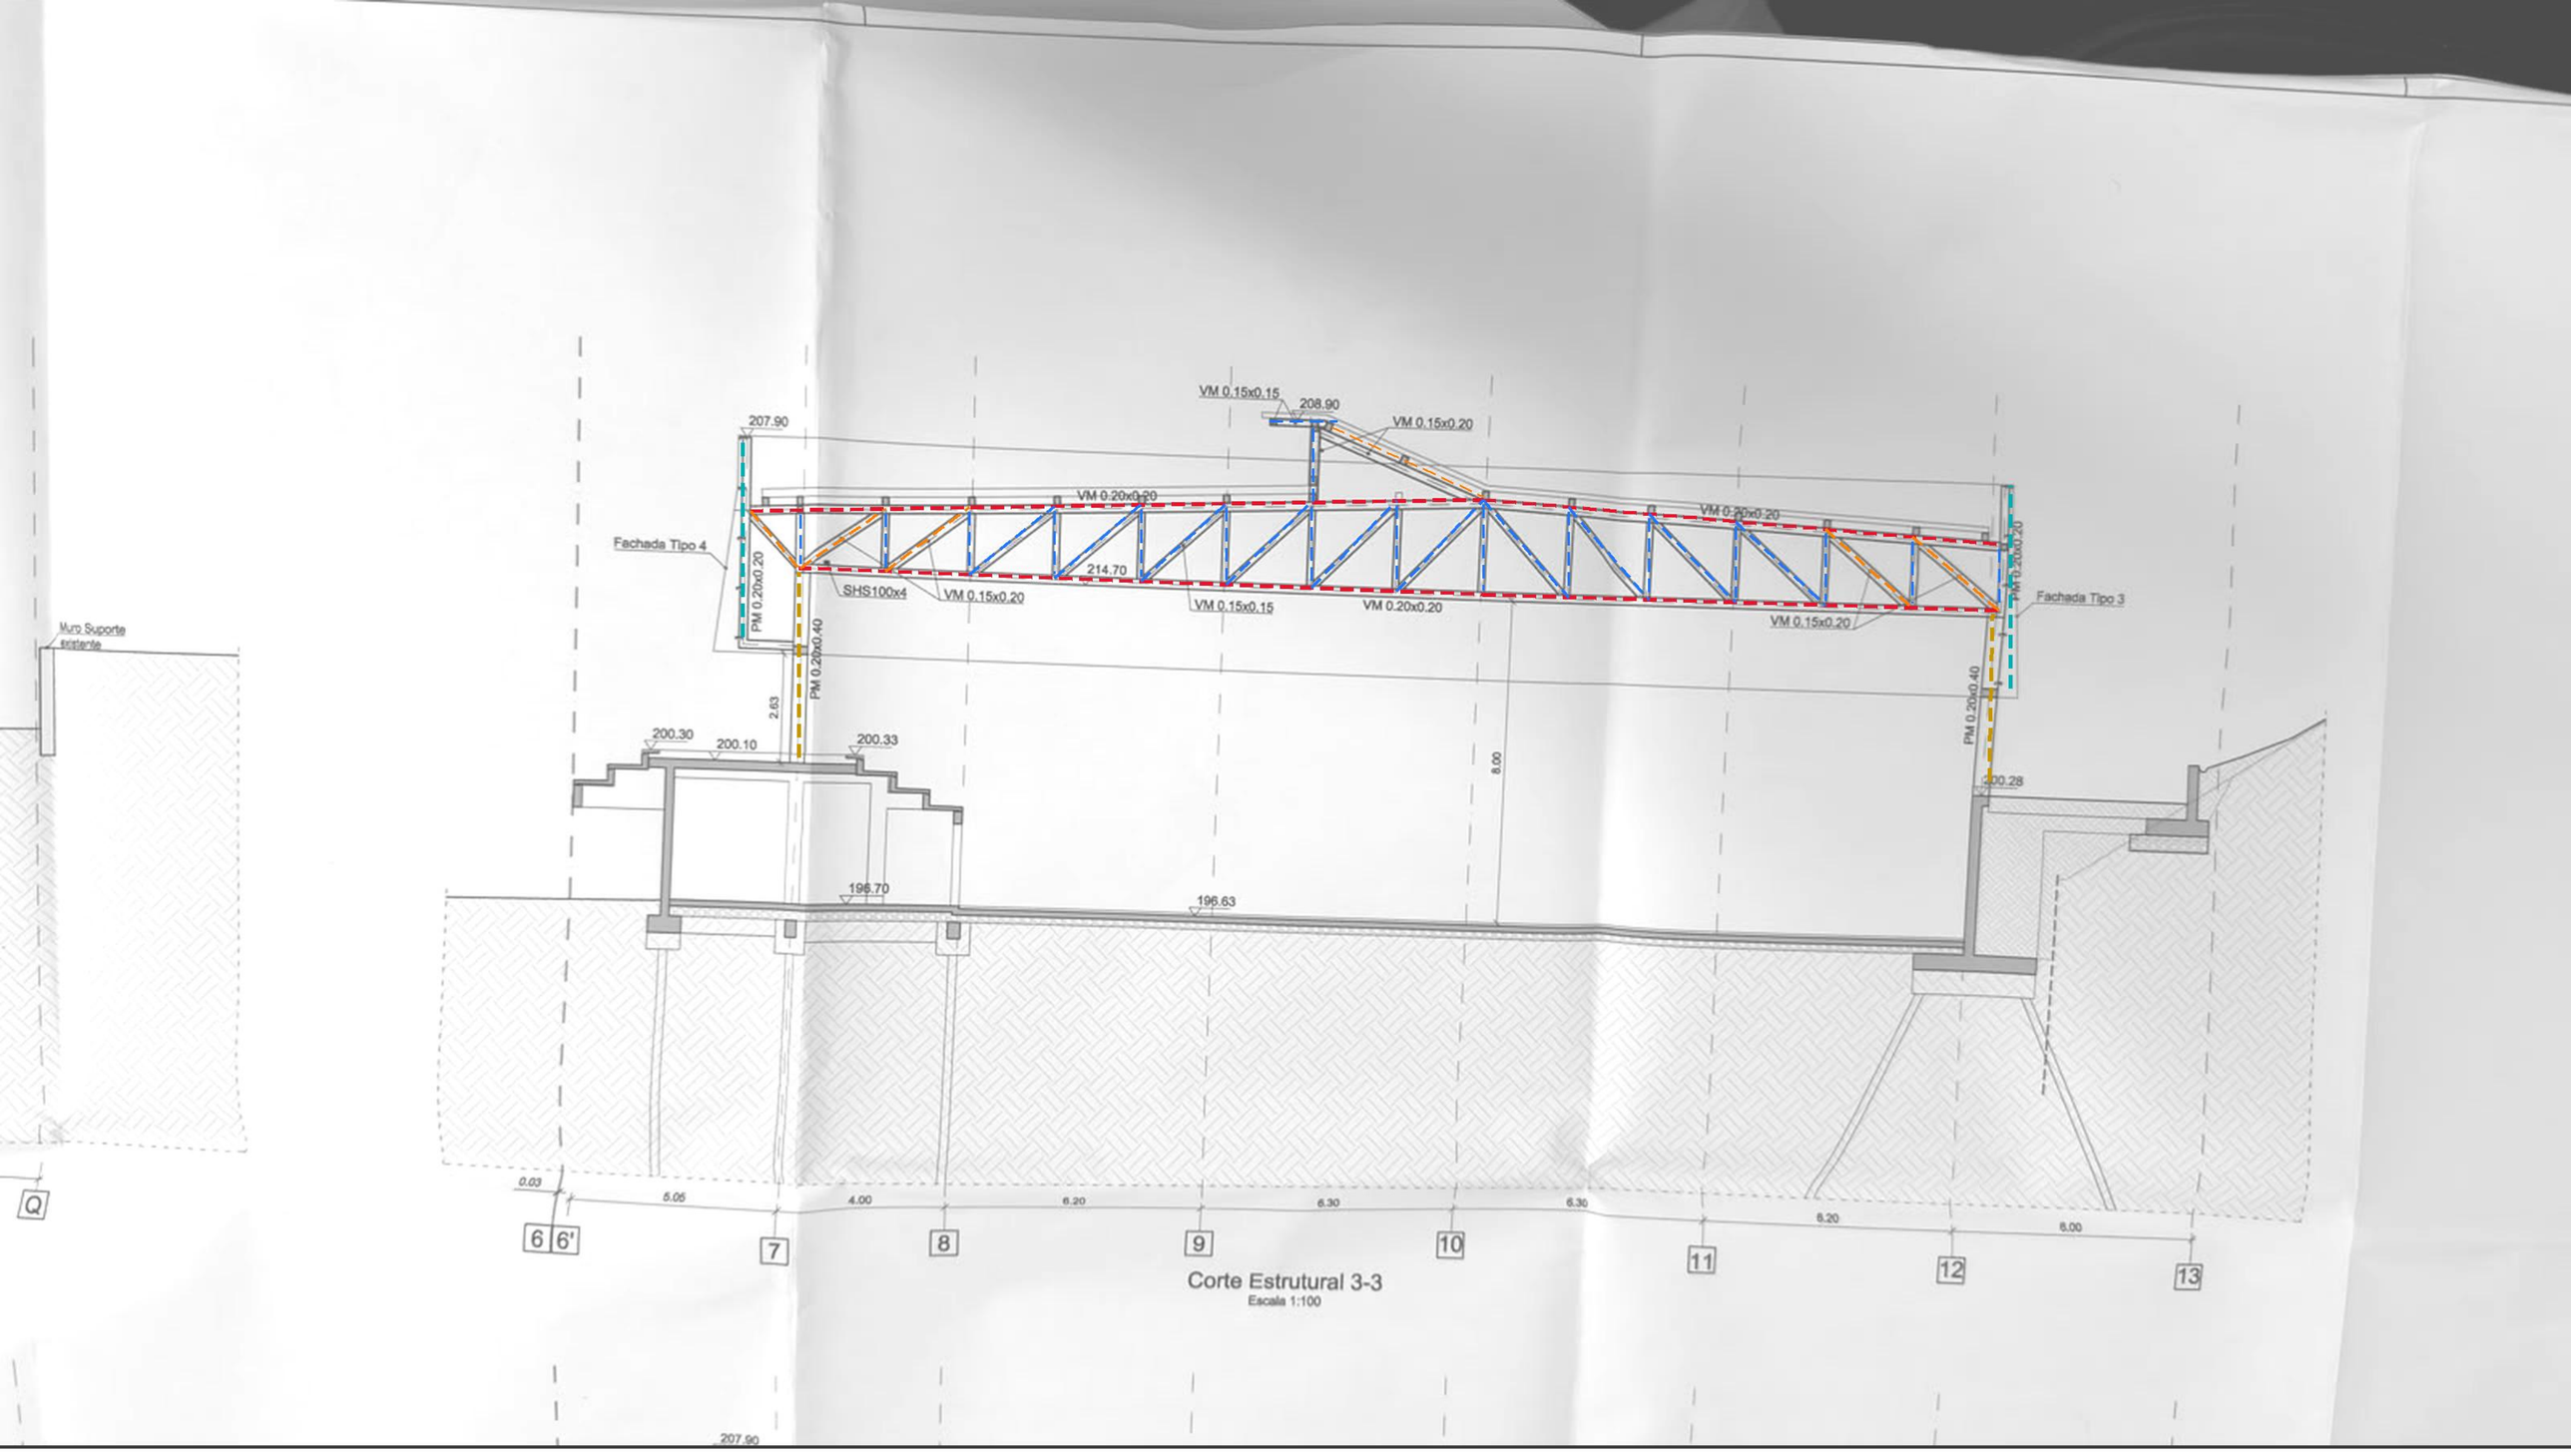

Corte Estrutural 3-3
Escala 1:100

Corte Estrutural 3-3 — Treliça 1

VM 0.15x0.15 VM 0.15x0.20 VM 0.20x0.20 PM 0.20x0.20 PM 0.20x0.40

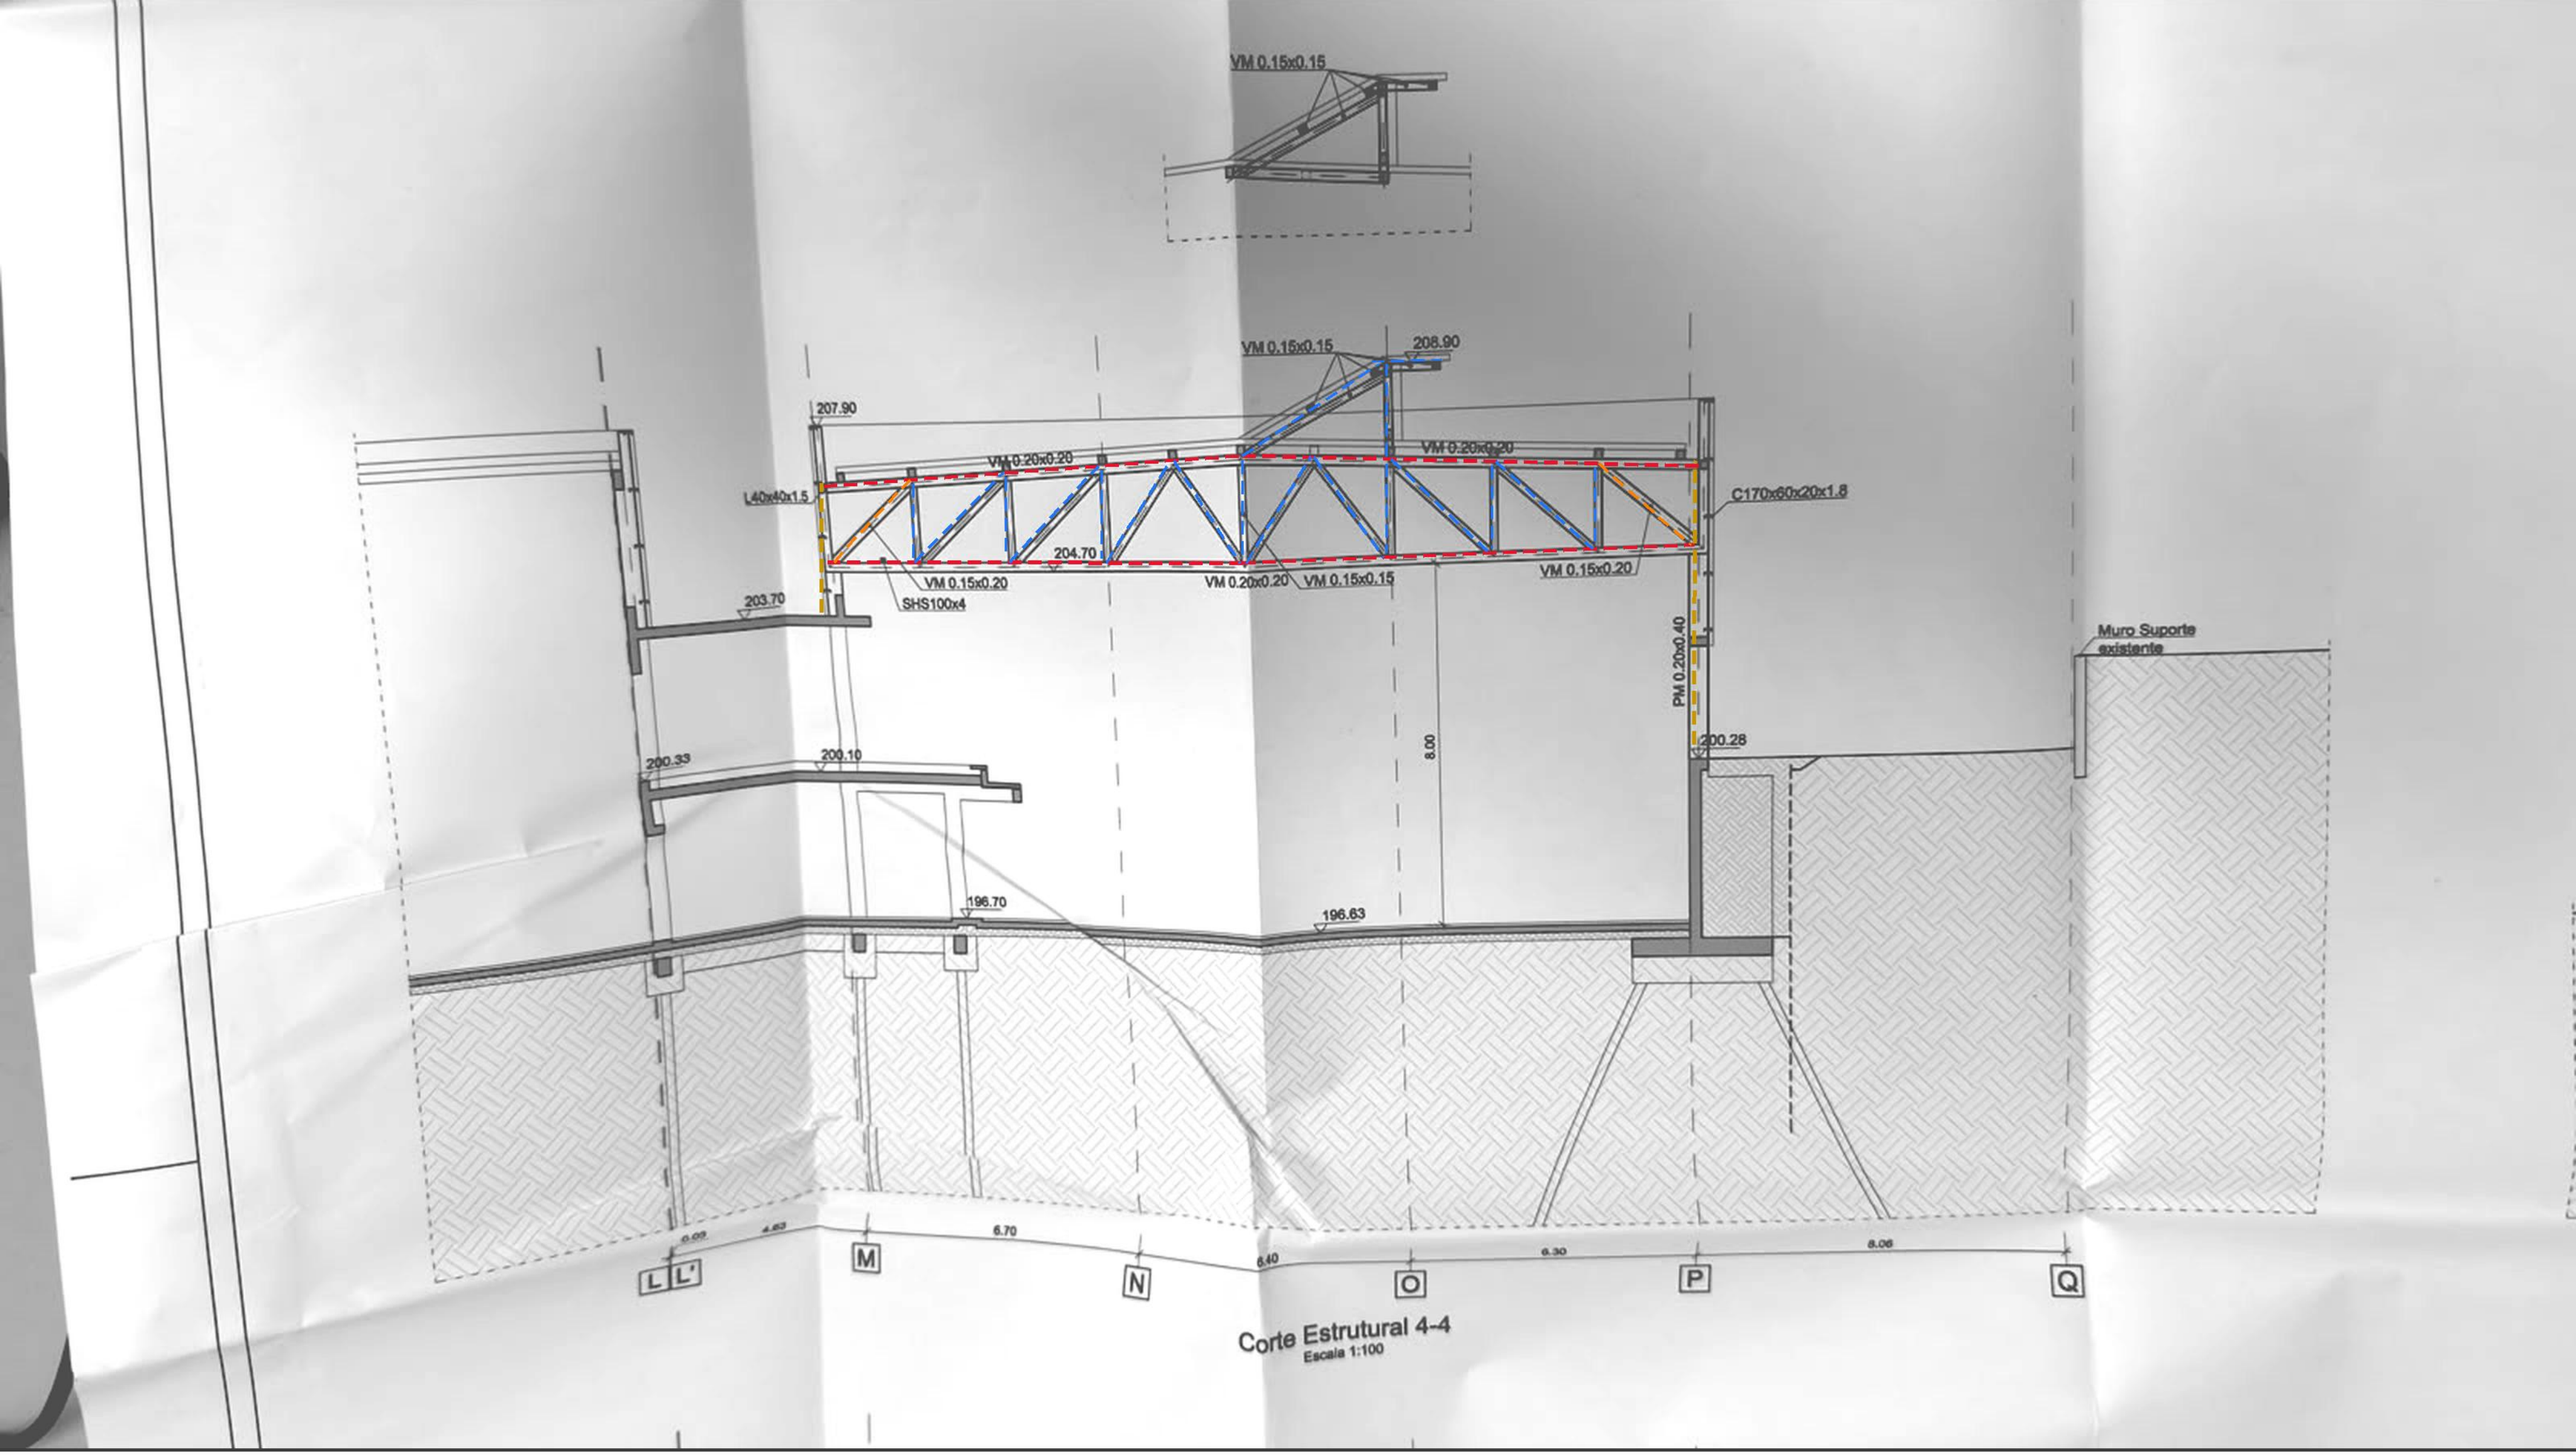

Corte Estrutural 4-4
Escala 1:100

Corte Estrutural 4-4 — Treliça 3


VM 0.15x0.15 VM 0.15x0.20 VM 0.20x0.20 PM 0.20x0.40



Alçado Eixo D
Escala 1:100

Alçado Eixo D — empena do bloco A

VM 0.20x0.20 VM 0.20x0.40 PM 0.20x0.20 PM 0.20x0.40

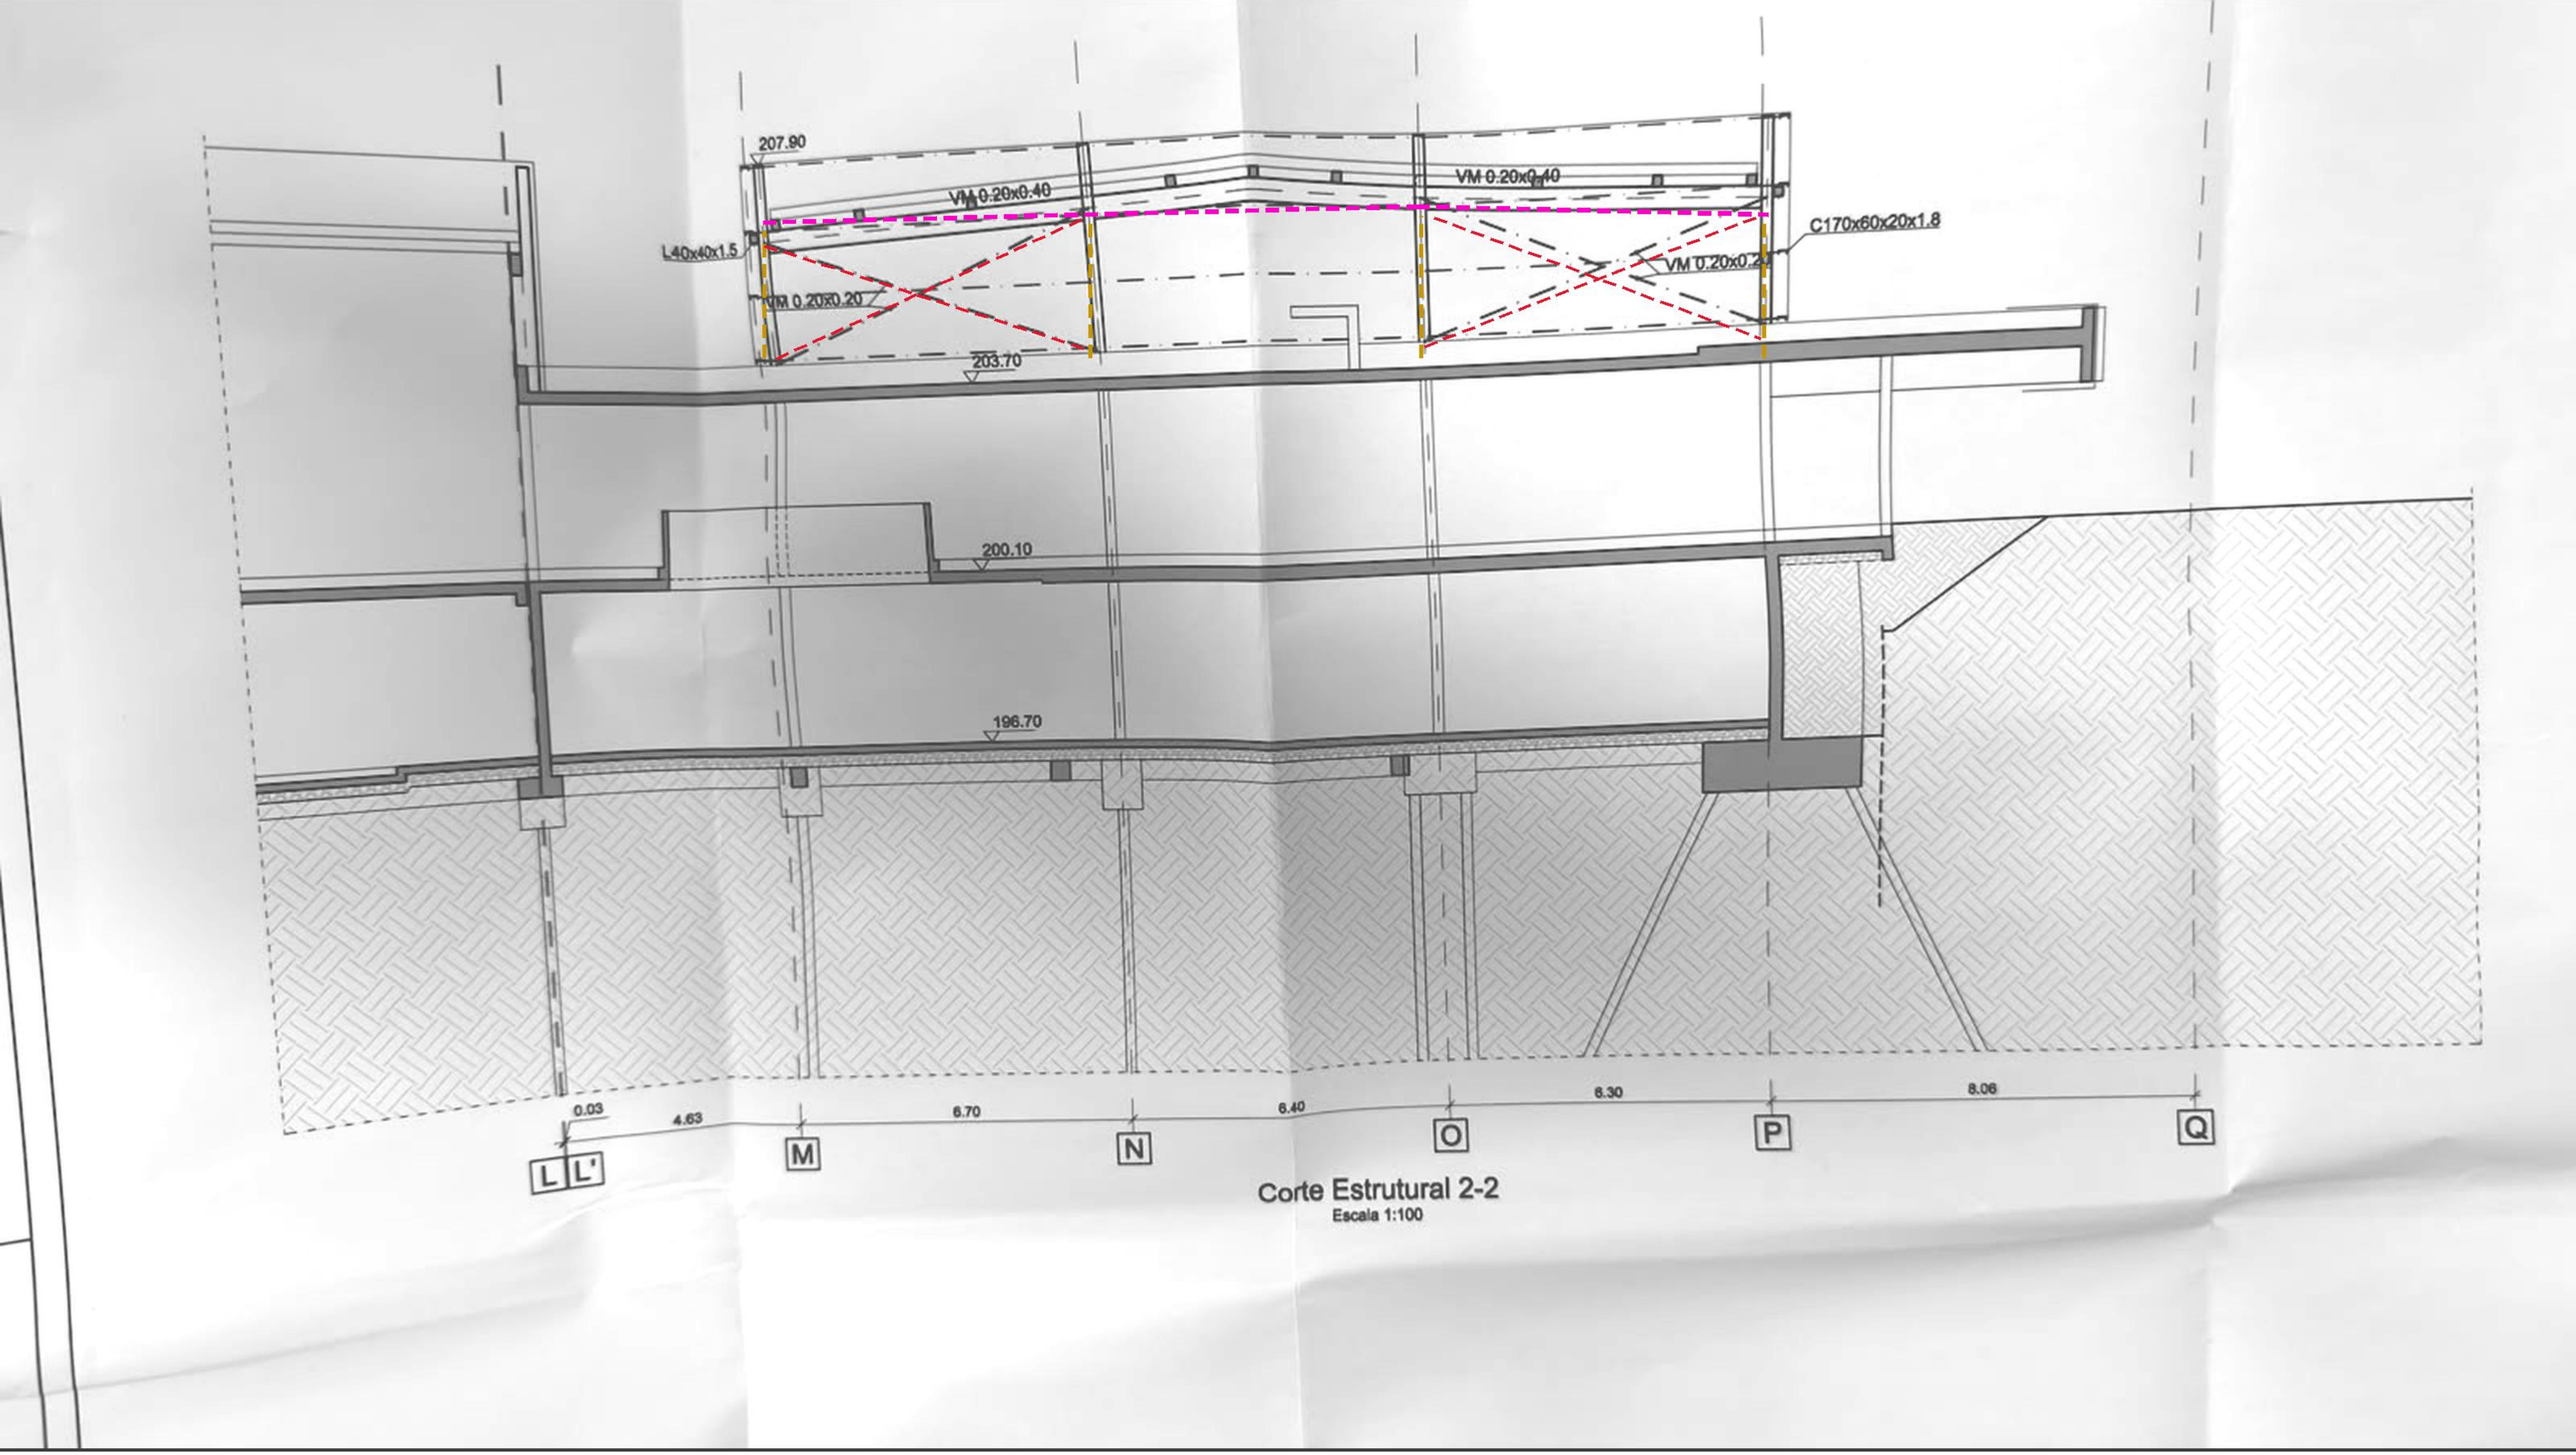

Corte Estrutural 2-2
Escala 1:100

Corte Estrutural 2-2 — empena do bloco B

VM 0.20x0.20 **VM 0.20x0.40** **PM 0.20x0.40**