
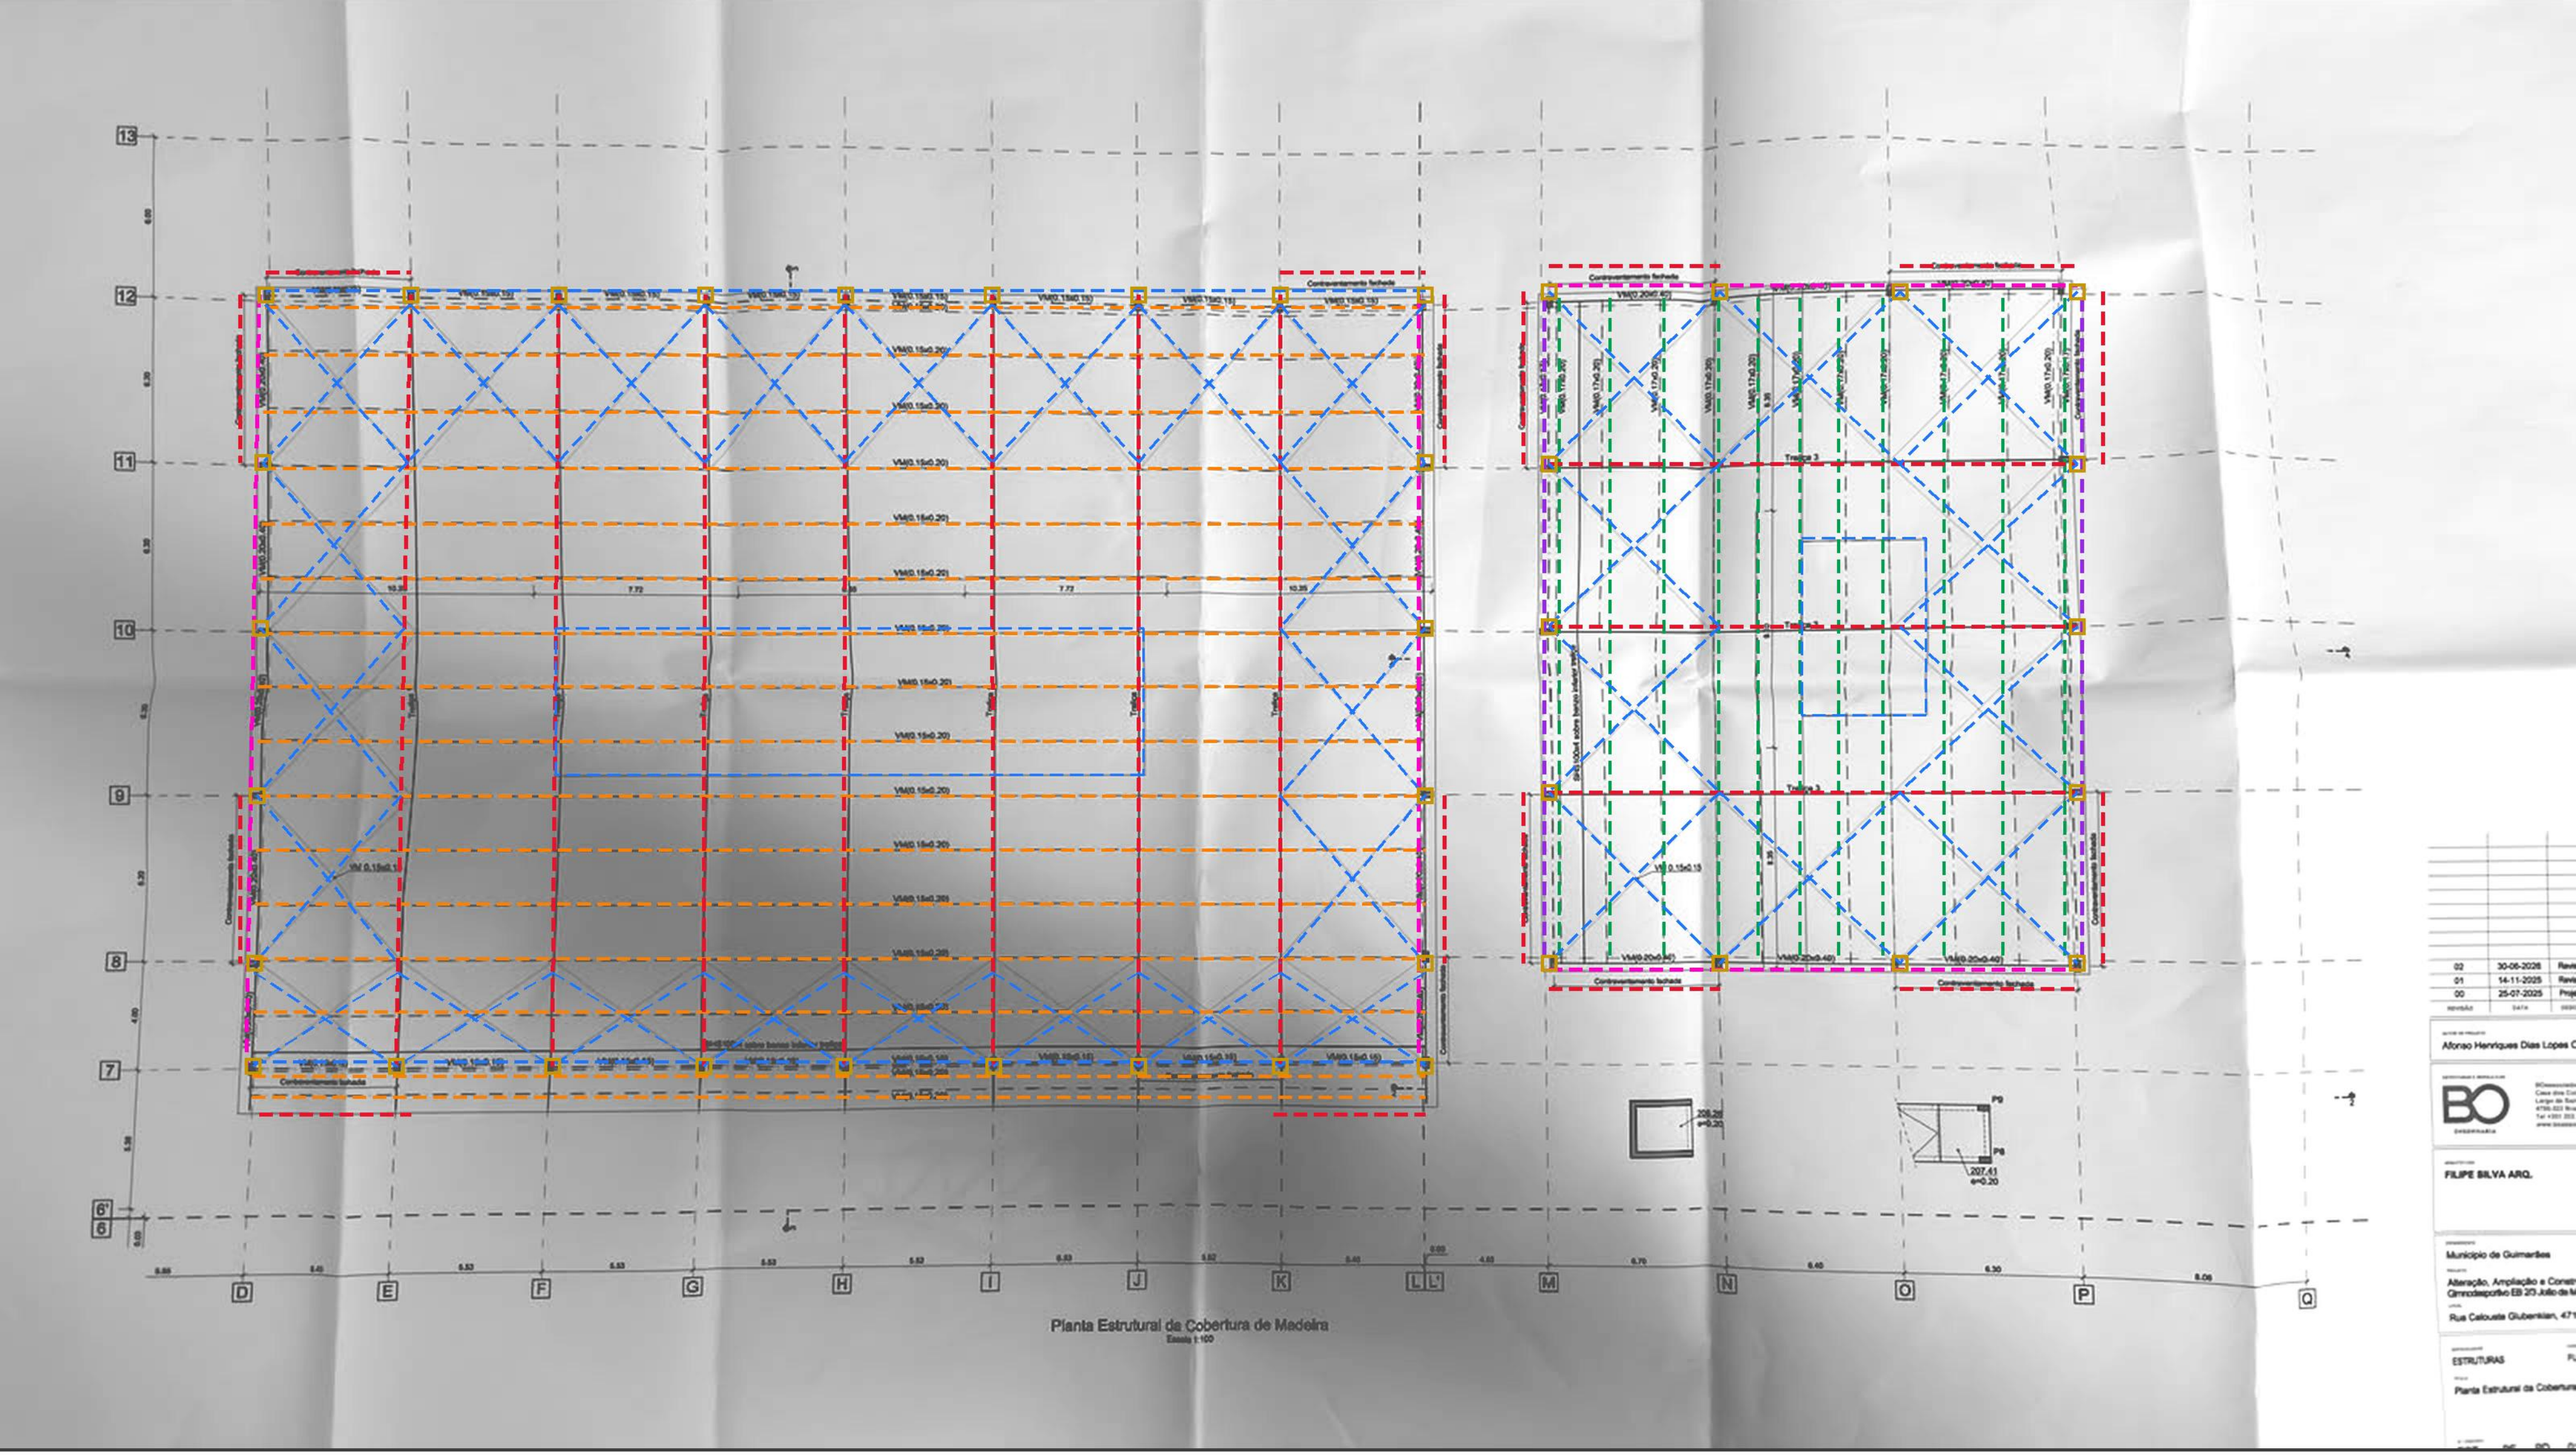


Planta Estrutural da Cobertura de Madeira — secções

- **VM 0.15x0.15** — diagonais correntes e montantes das treliças, contraventamento da cobertura, bordaduras, claraboia
- **VM 0.15x0.20** — madres do bloco A, diagonais junto aos apoios, peças inclinadas da claraboia
- **VM 0.17x0.17** — madres de bordadura do bloco B (eixos M e P)
- **VM 0.17x0.20** — madres do bloco B
- **VM 0.20x0.20** — banzos das treliças, contraventamento de fachada
- **VM 0.20x0.40** — vigas de empena
- **PM 0.20x0.40** — pilares

Na planta: os quadrados marcam os pilares; as linhas vermelhas por fora do contorno marcam os vãos com contraventamento de fachada; o retângulo azul é a claraboia.

VM 0.17x0.25 (artigo 2.5.1.5 do MQT): não identificada nestas folhas. Marcação feita sobre as fotografias das folhas de estruturas, escala 1:100.

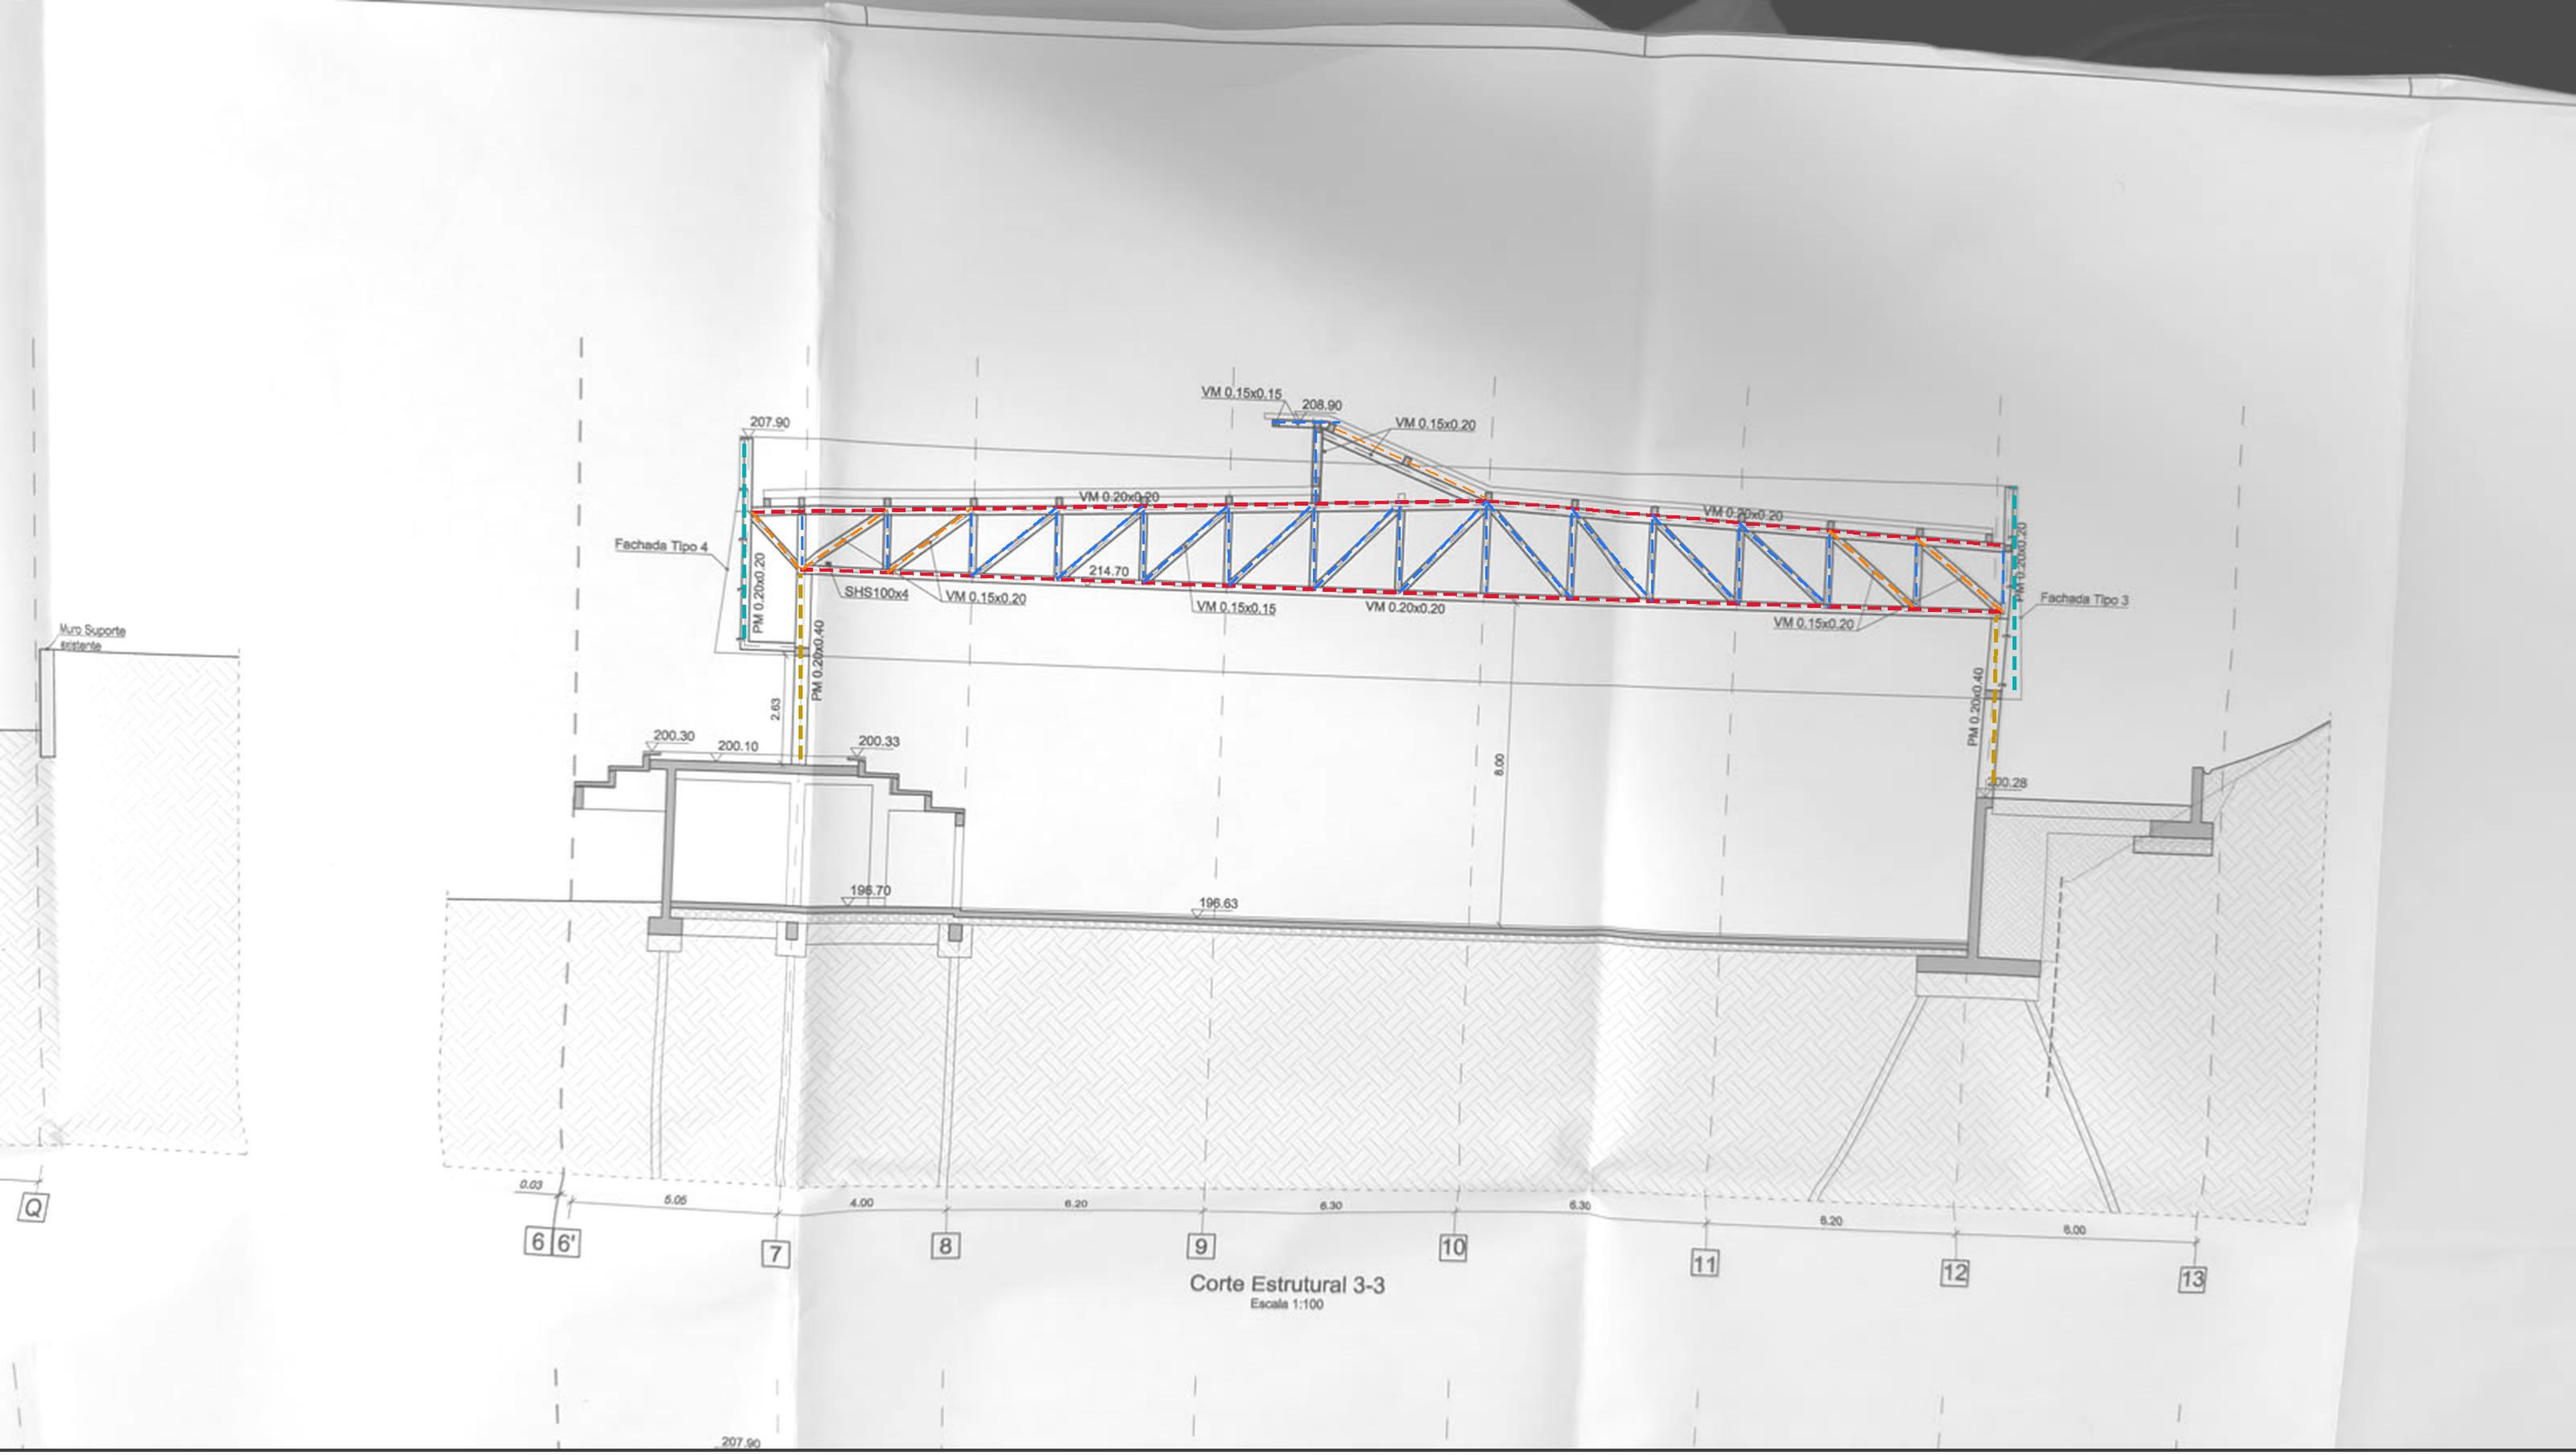


Corte Estrutural 3-3
Escala 1:100

Corte Estrutural 3-3 — Treliça 1 (bloco A)

- **VM 0.15x0.15** — diagonais correntes e montantes das treliças, contraventamento da cobertura, bordaduras, claraboia
- **VM 0.15x0.20** — madres do bloco A, diagonais junto aos apoios, peças inclinadas da claraboia
- **VM 0.20x0.20** — banzos das treliças, contraventamento de fachada
- **PM 0.20x0.20** — prumos de fachada (Fachadas Tipo 3 e 4)
- **PM 0.20x0.40** — pilares


VM 0.17x0.25 (artigo 2.5.1.5 do MQT): não identificada nestas folhas. Marcação feita sobre as fotografias das folhas de estruturas, escala 1:100.

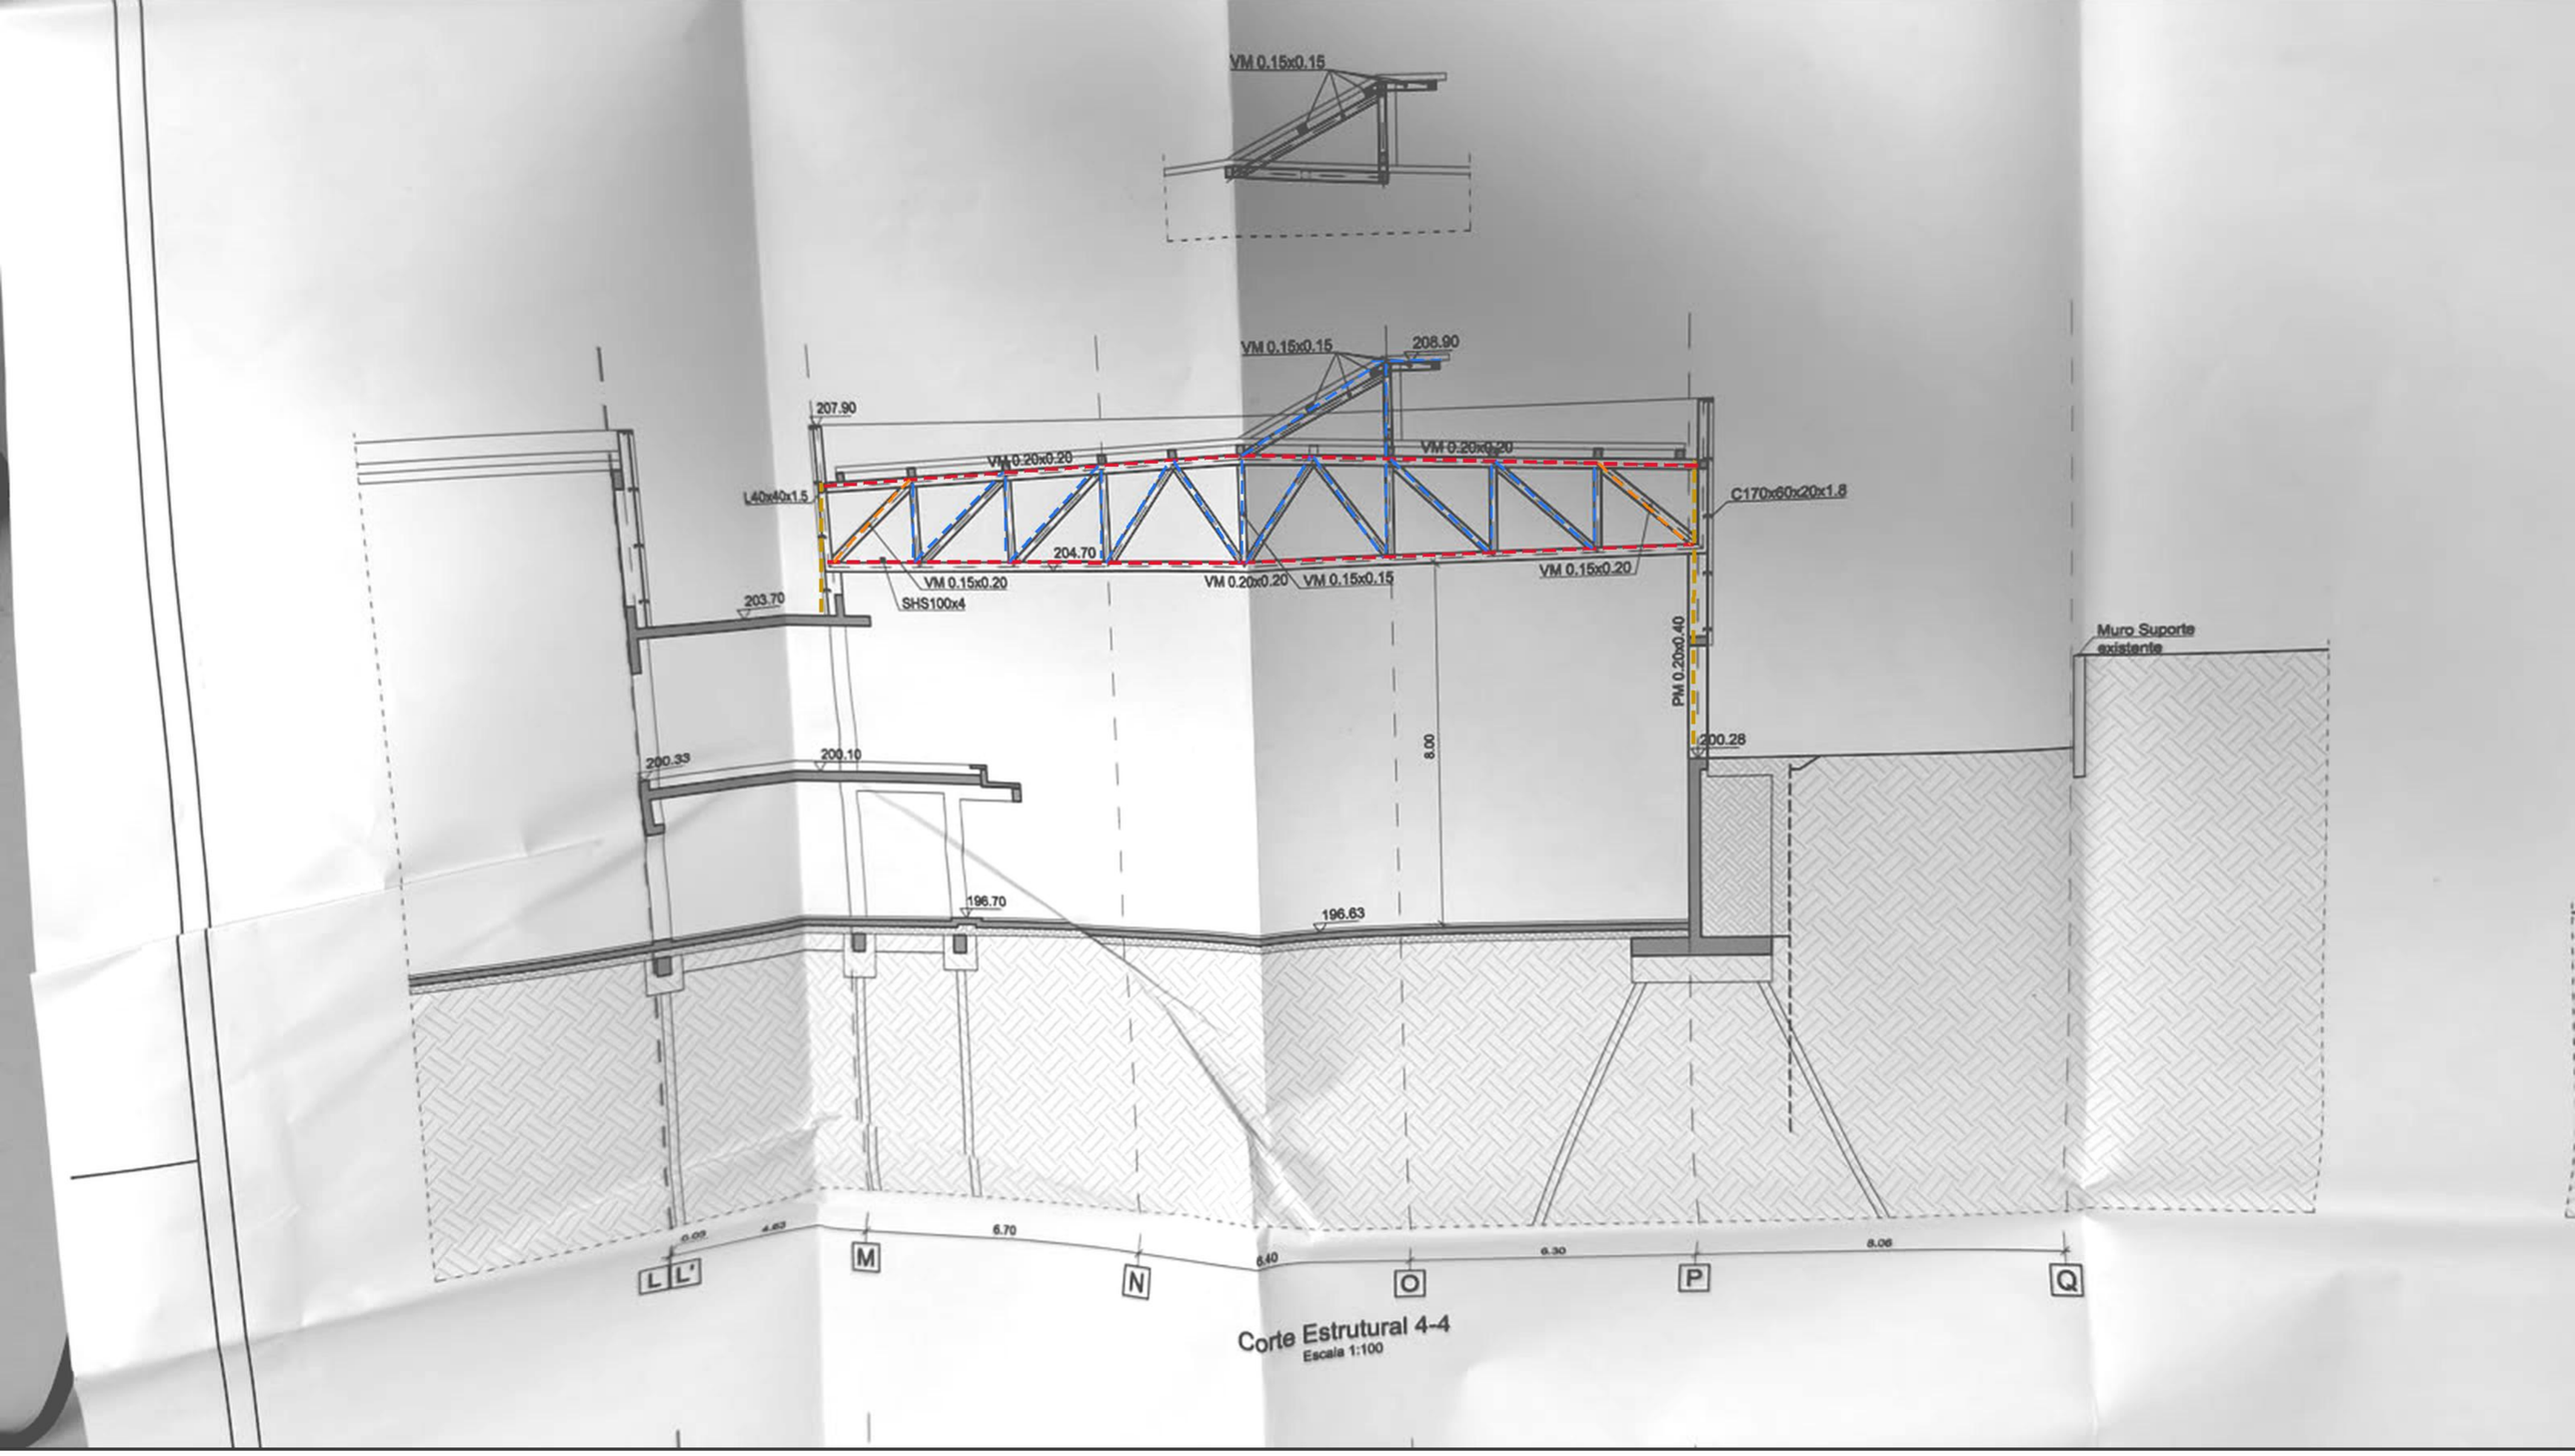

Corte Estrutural 4-4 — Treliça 3 (bloco B)

- **VM 0.15x0.15** — diagonais correntes e montantes das treliças, contraventamento da cobertura, bordaduras, claraboia
- **VM 0.15x0.20** — madres do bloco A, diagonais junto aos apoios, peças inclinadas da claraboia
- **VM 0.20x0.20** — banzos das treliças, contraventamento de fachada
- **PM 0.20x0.40** — pilares


VM 0.17x0.25 (artigo 2.5.1.5 do MQT): não identificada nestas folhas. Marcação feita sobre as fotografias das folhas de estruturas, escala 1:100.

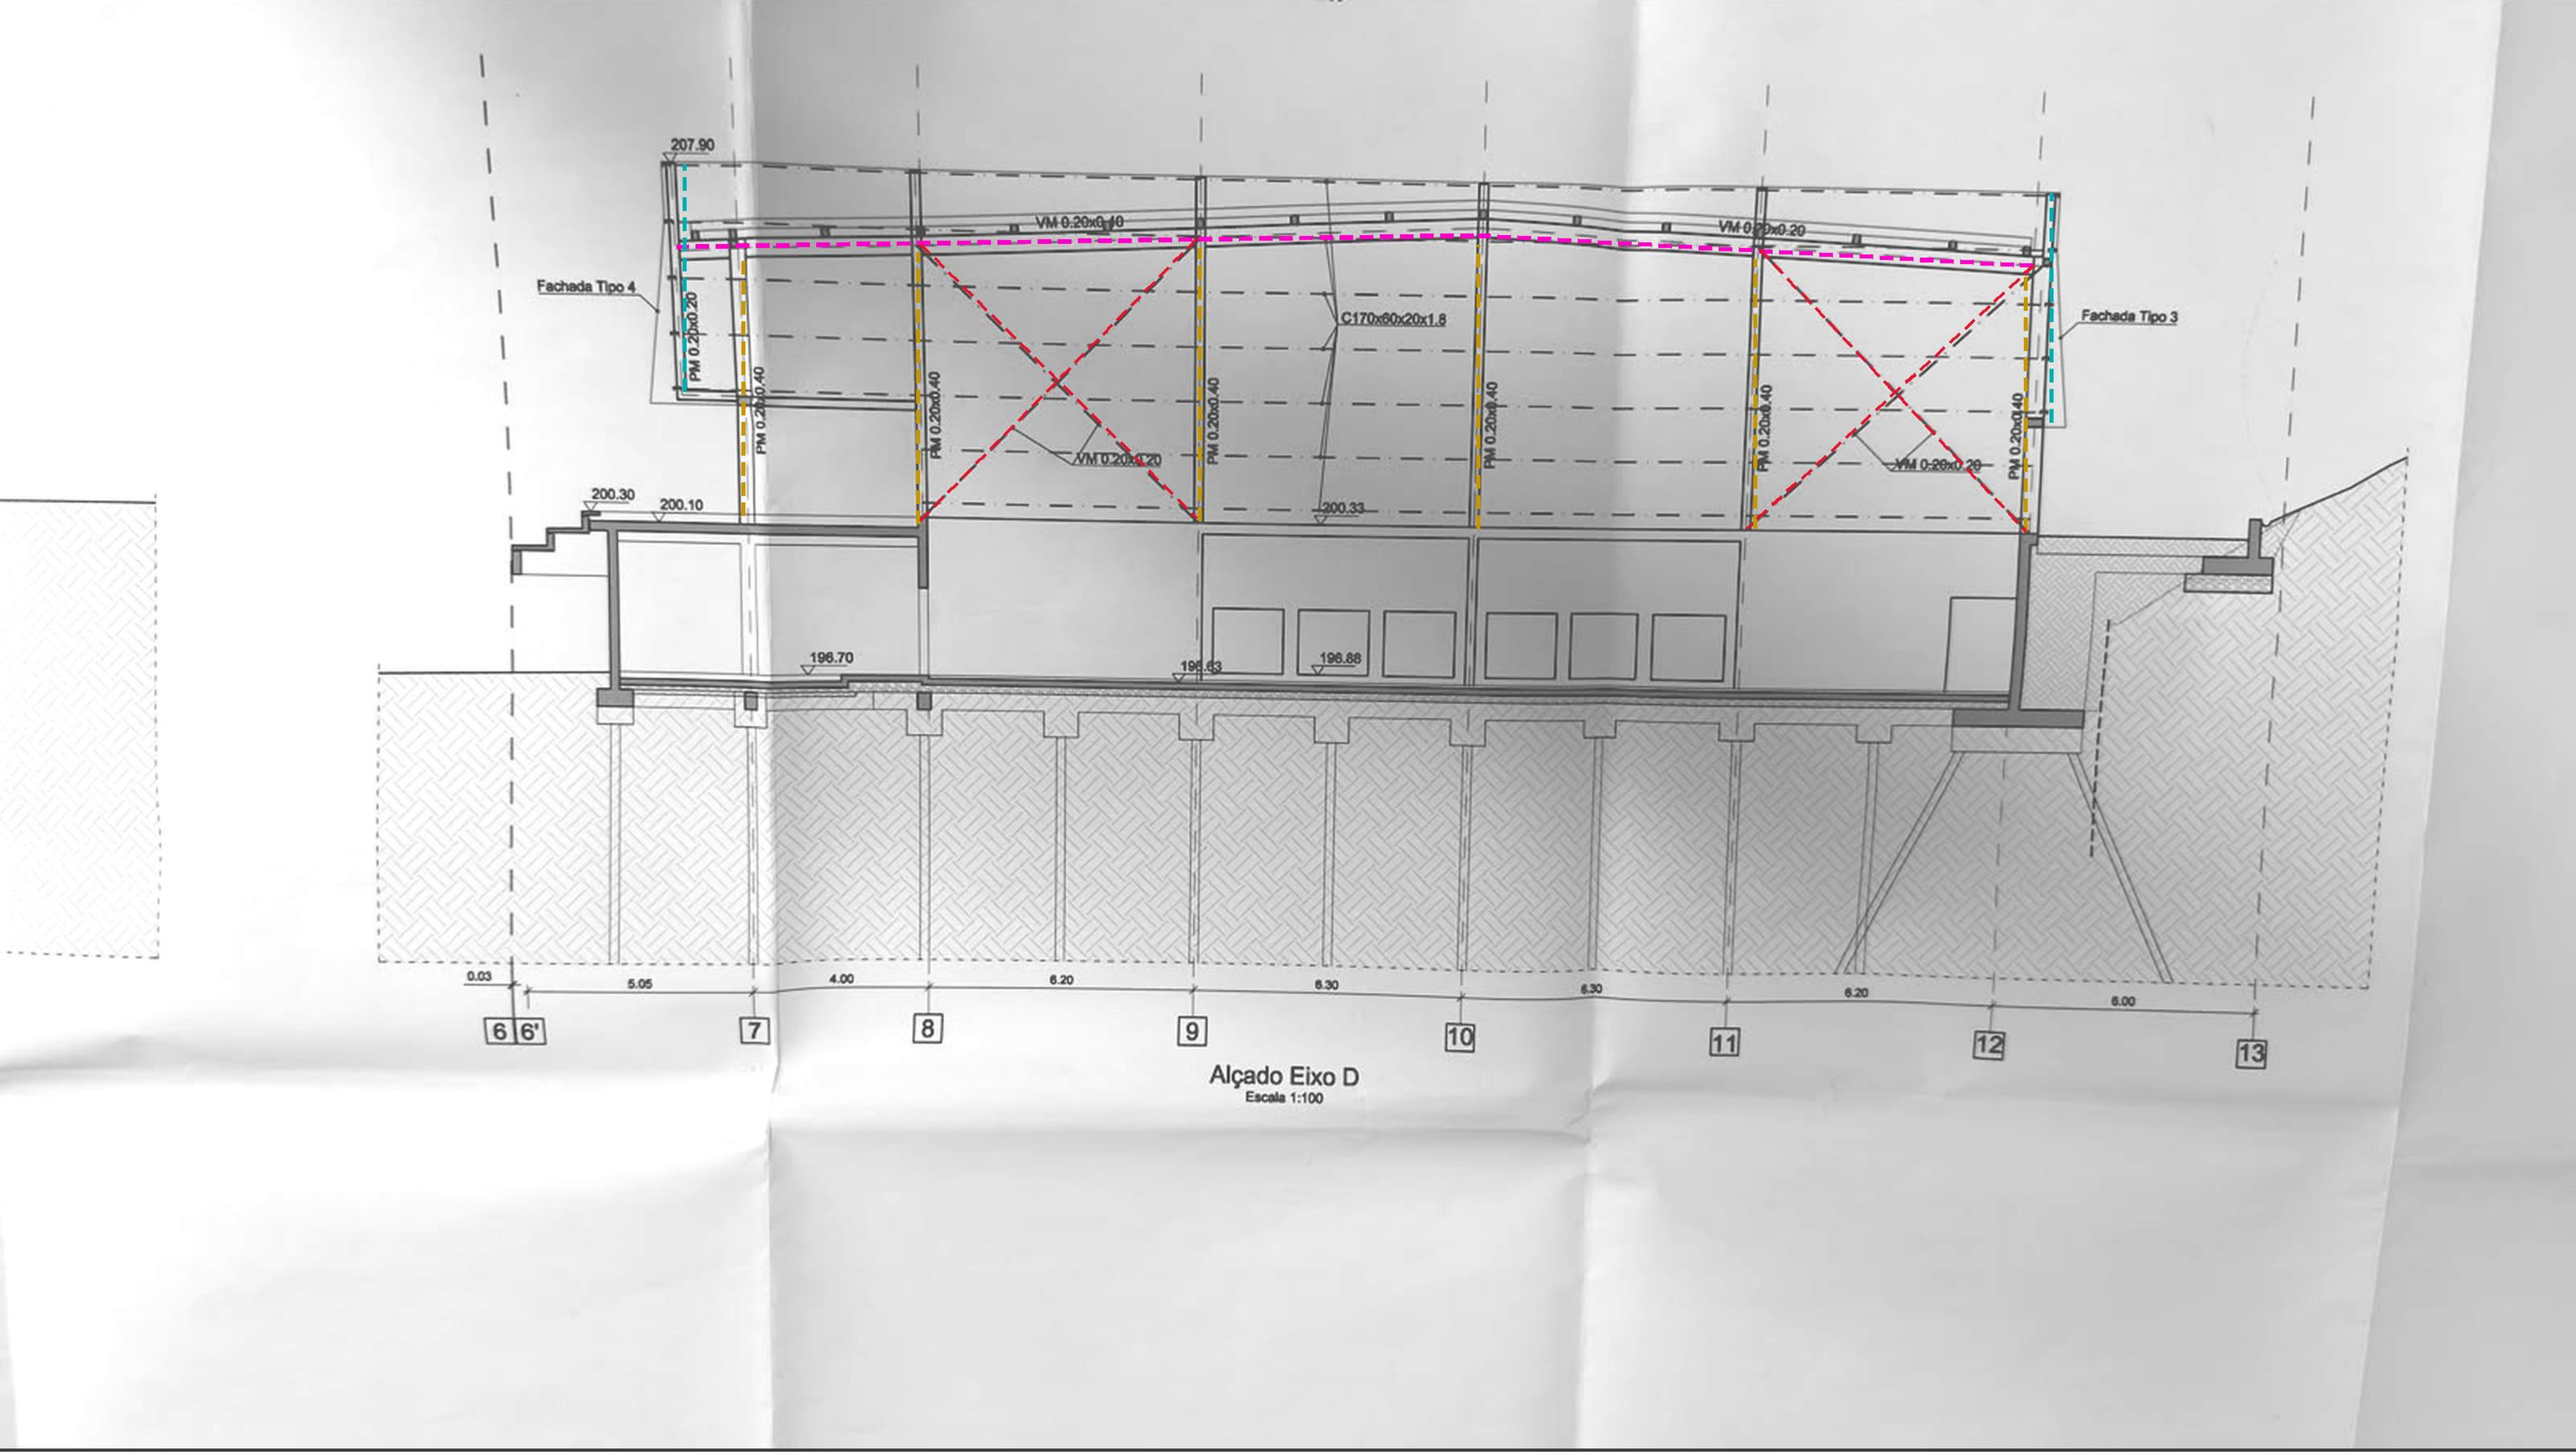

Alçado Eixo D — empena do bloco A

- **VM 0.20x0.20** — banzos das treliças, contraventamento de fachada
- **VM 0.20x0.40** — vigas de empena
- **PM 0.20x0.20** — prumos de fachada (Fachadas Tipo 3 e 4)
- **PM 0.20x0.40** — pilares

VM 0.17x0.25 (artigo 2.5.1.5 do MQT): não identificada nestas folhas. Marcação feita sobre as fotografias das folhas de estruturas, escala 1:100.

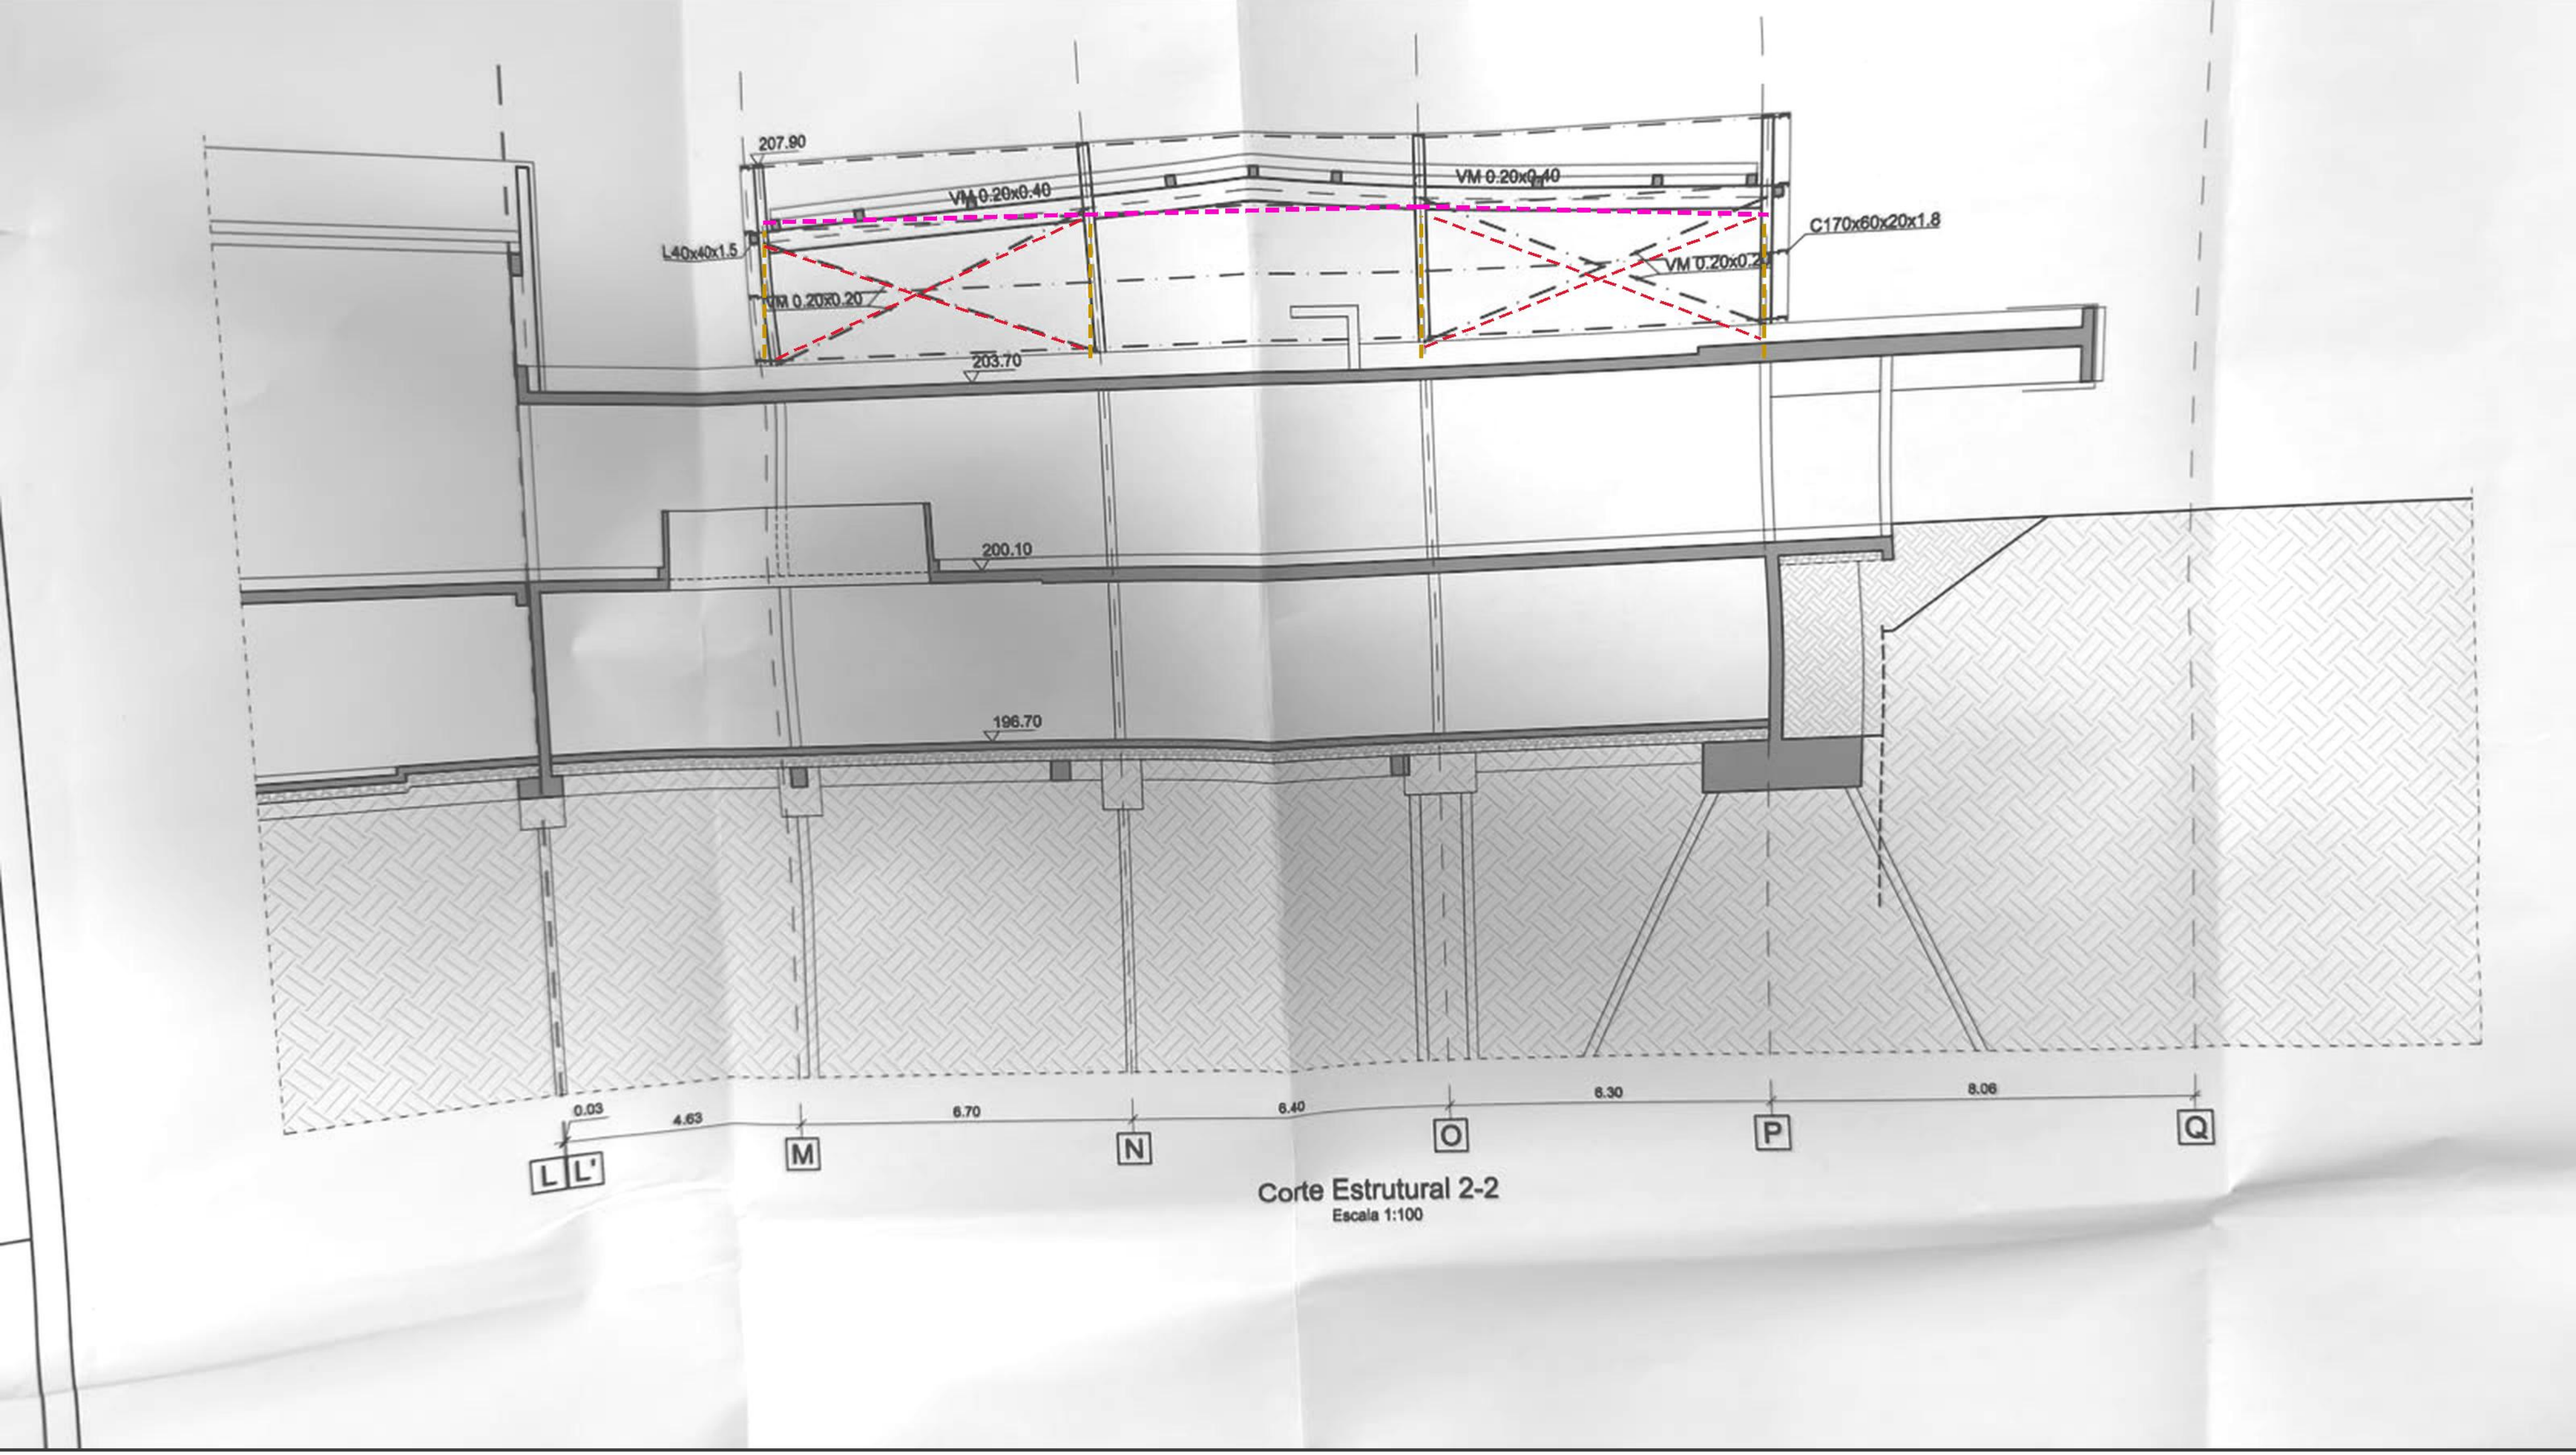

Corte Estrutural 2-2
Escala 1:100

Corte Estrutural 2-2 — empena do bloco B

- **VM 0.20x0.20** — banzos das treliças, contraventamento de fachada
- **VM 0.20x0.40** — vigas de empena
- **PM 0.20x0.40** — pilares

VM 0.17x0.25 (artigo 2.5.1.5 do MQT): não identificada nestas folhas. Marcação feita sobre as fotografias das folhas de estruturas, escala 1:100.