
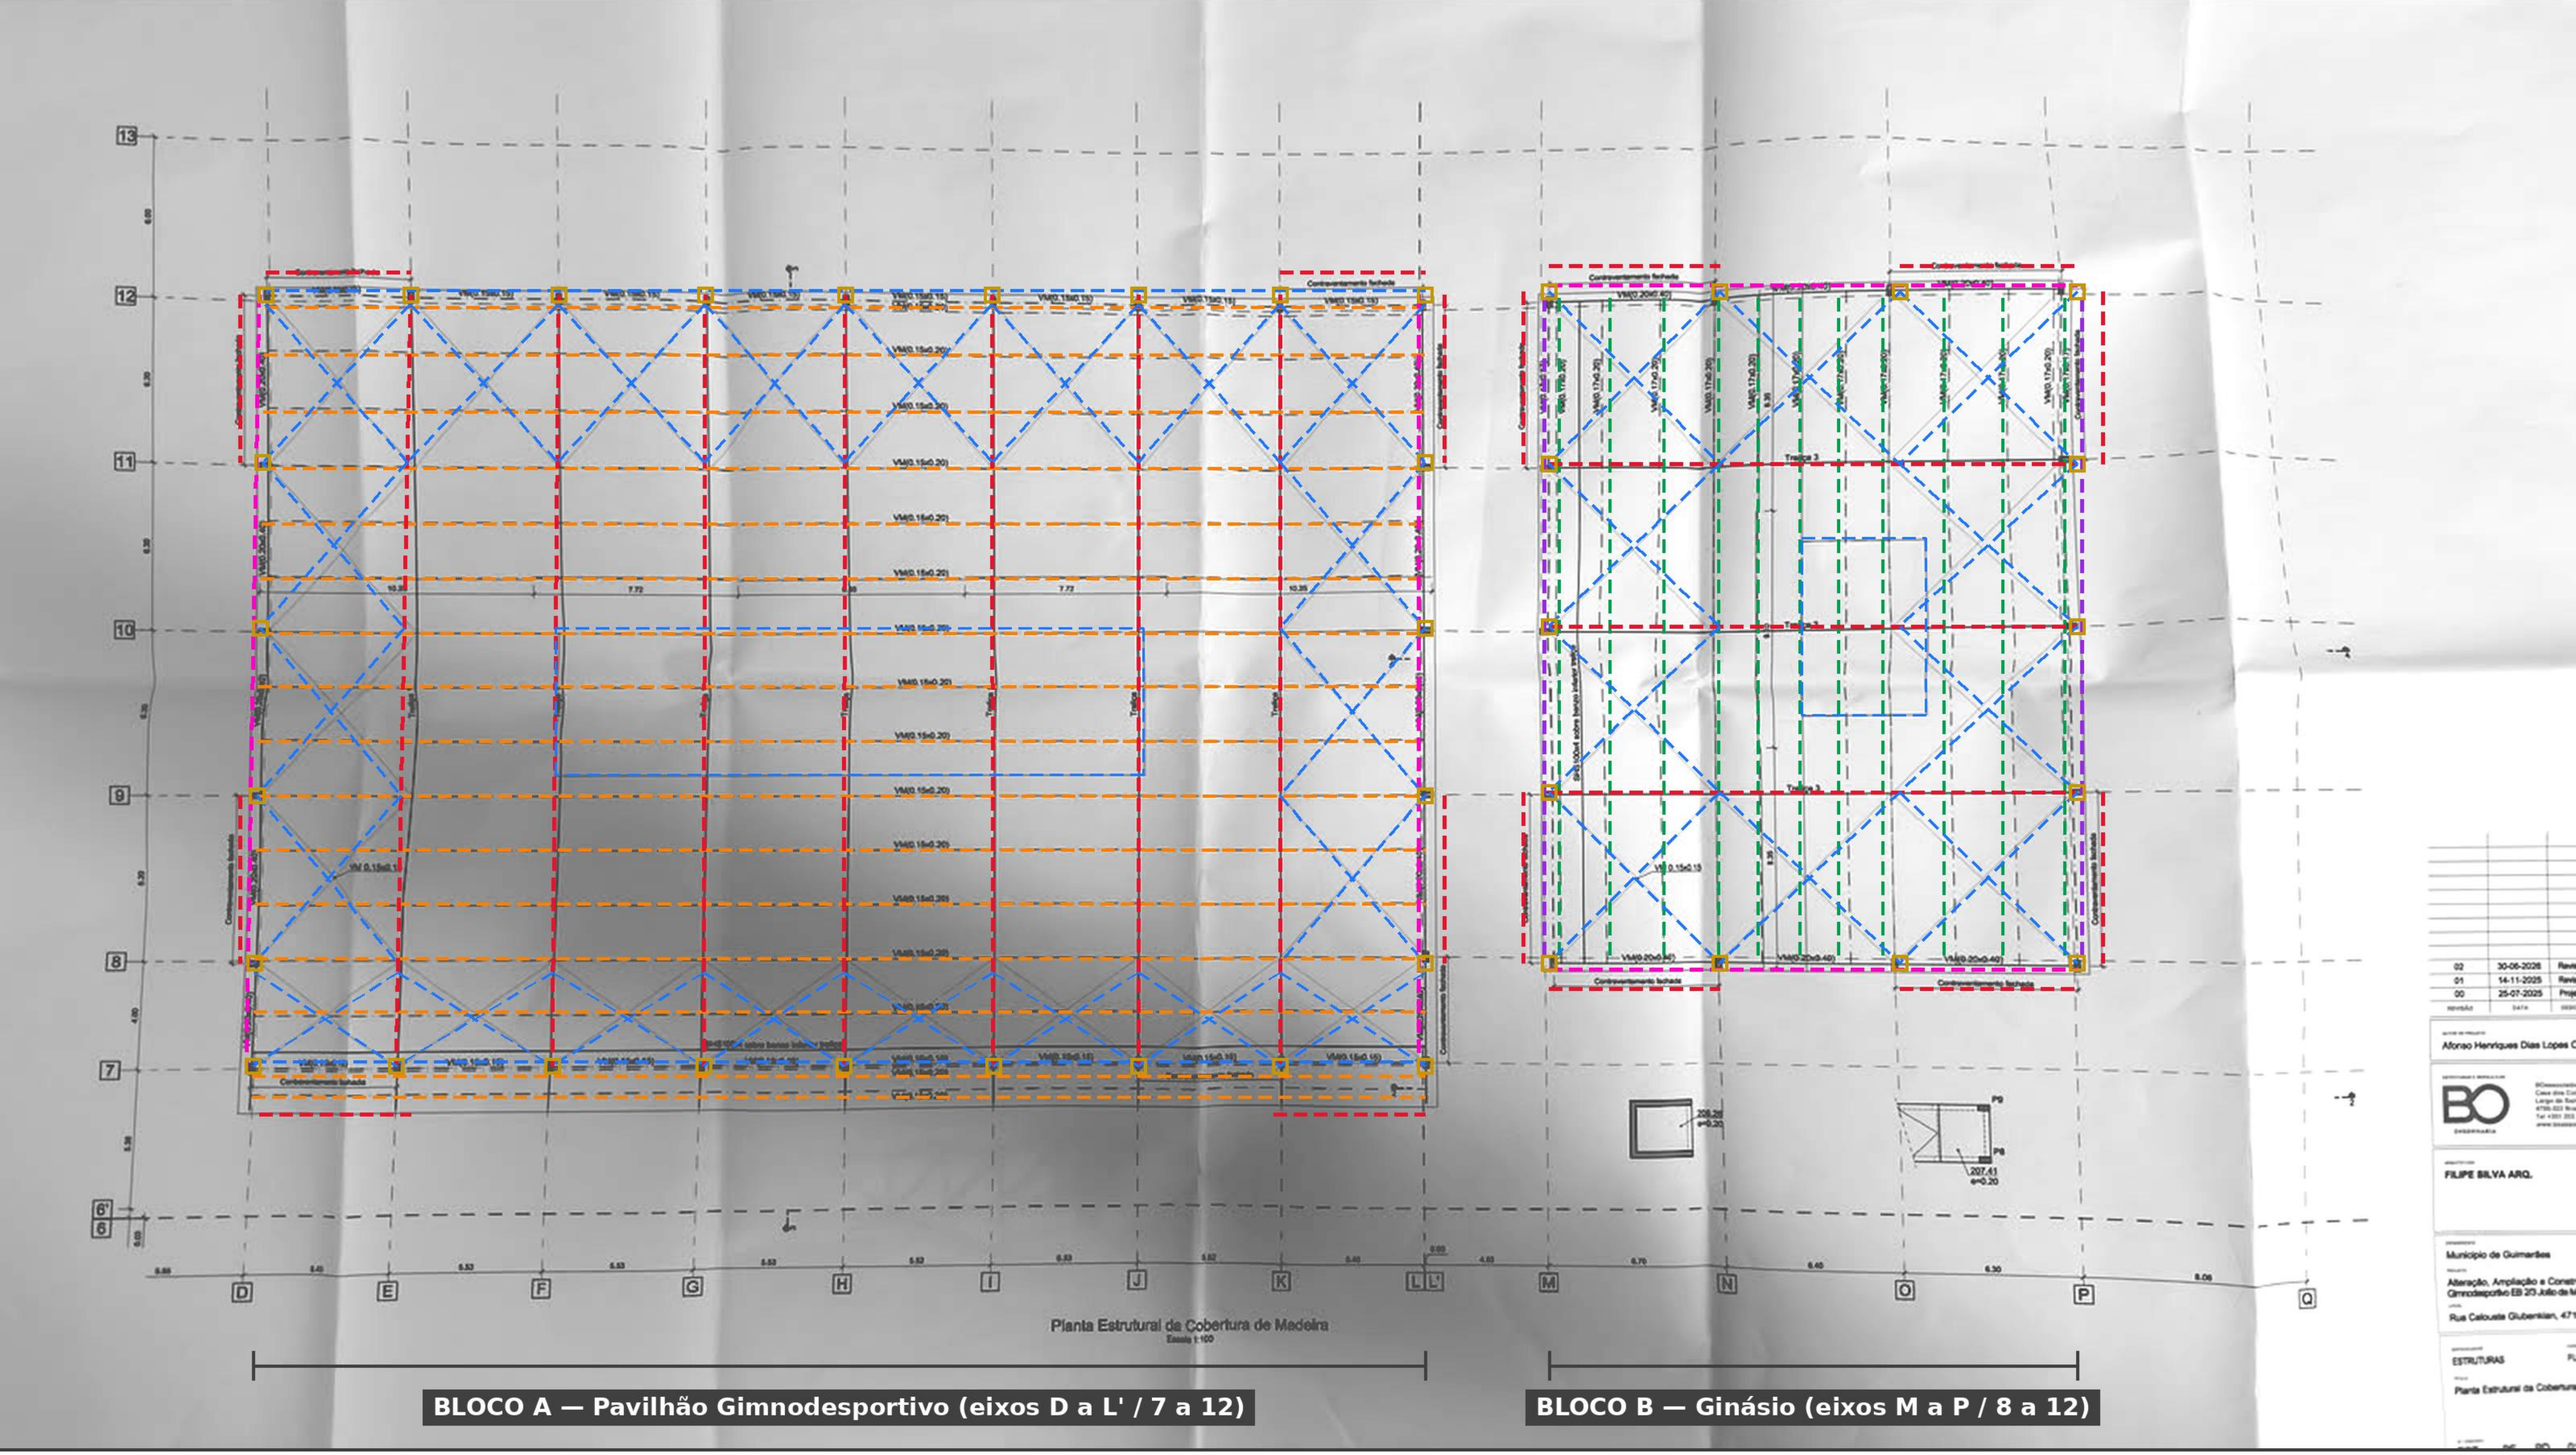


Planta Estrutural da Cobertura de Madeira


- VM 0.15x0.15
- VM 0.15x0.20
- VM 0.17x0.17
- VM 0.17x0.20
- VM 0.20x0.20
- VM 0.20x0.40
- PM 0.20x0.40

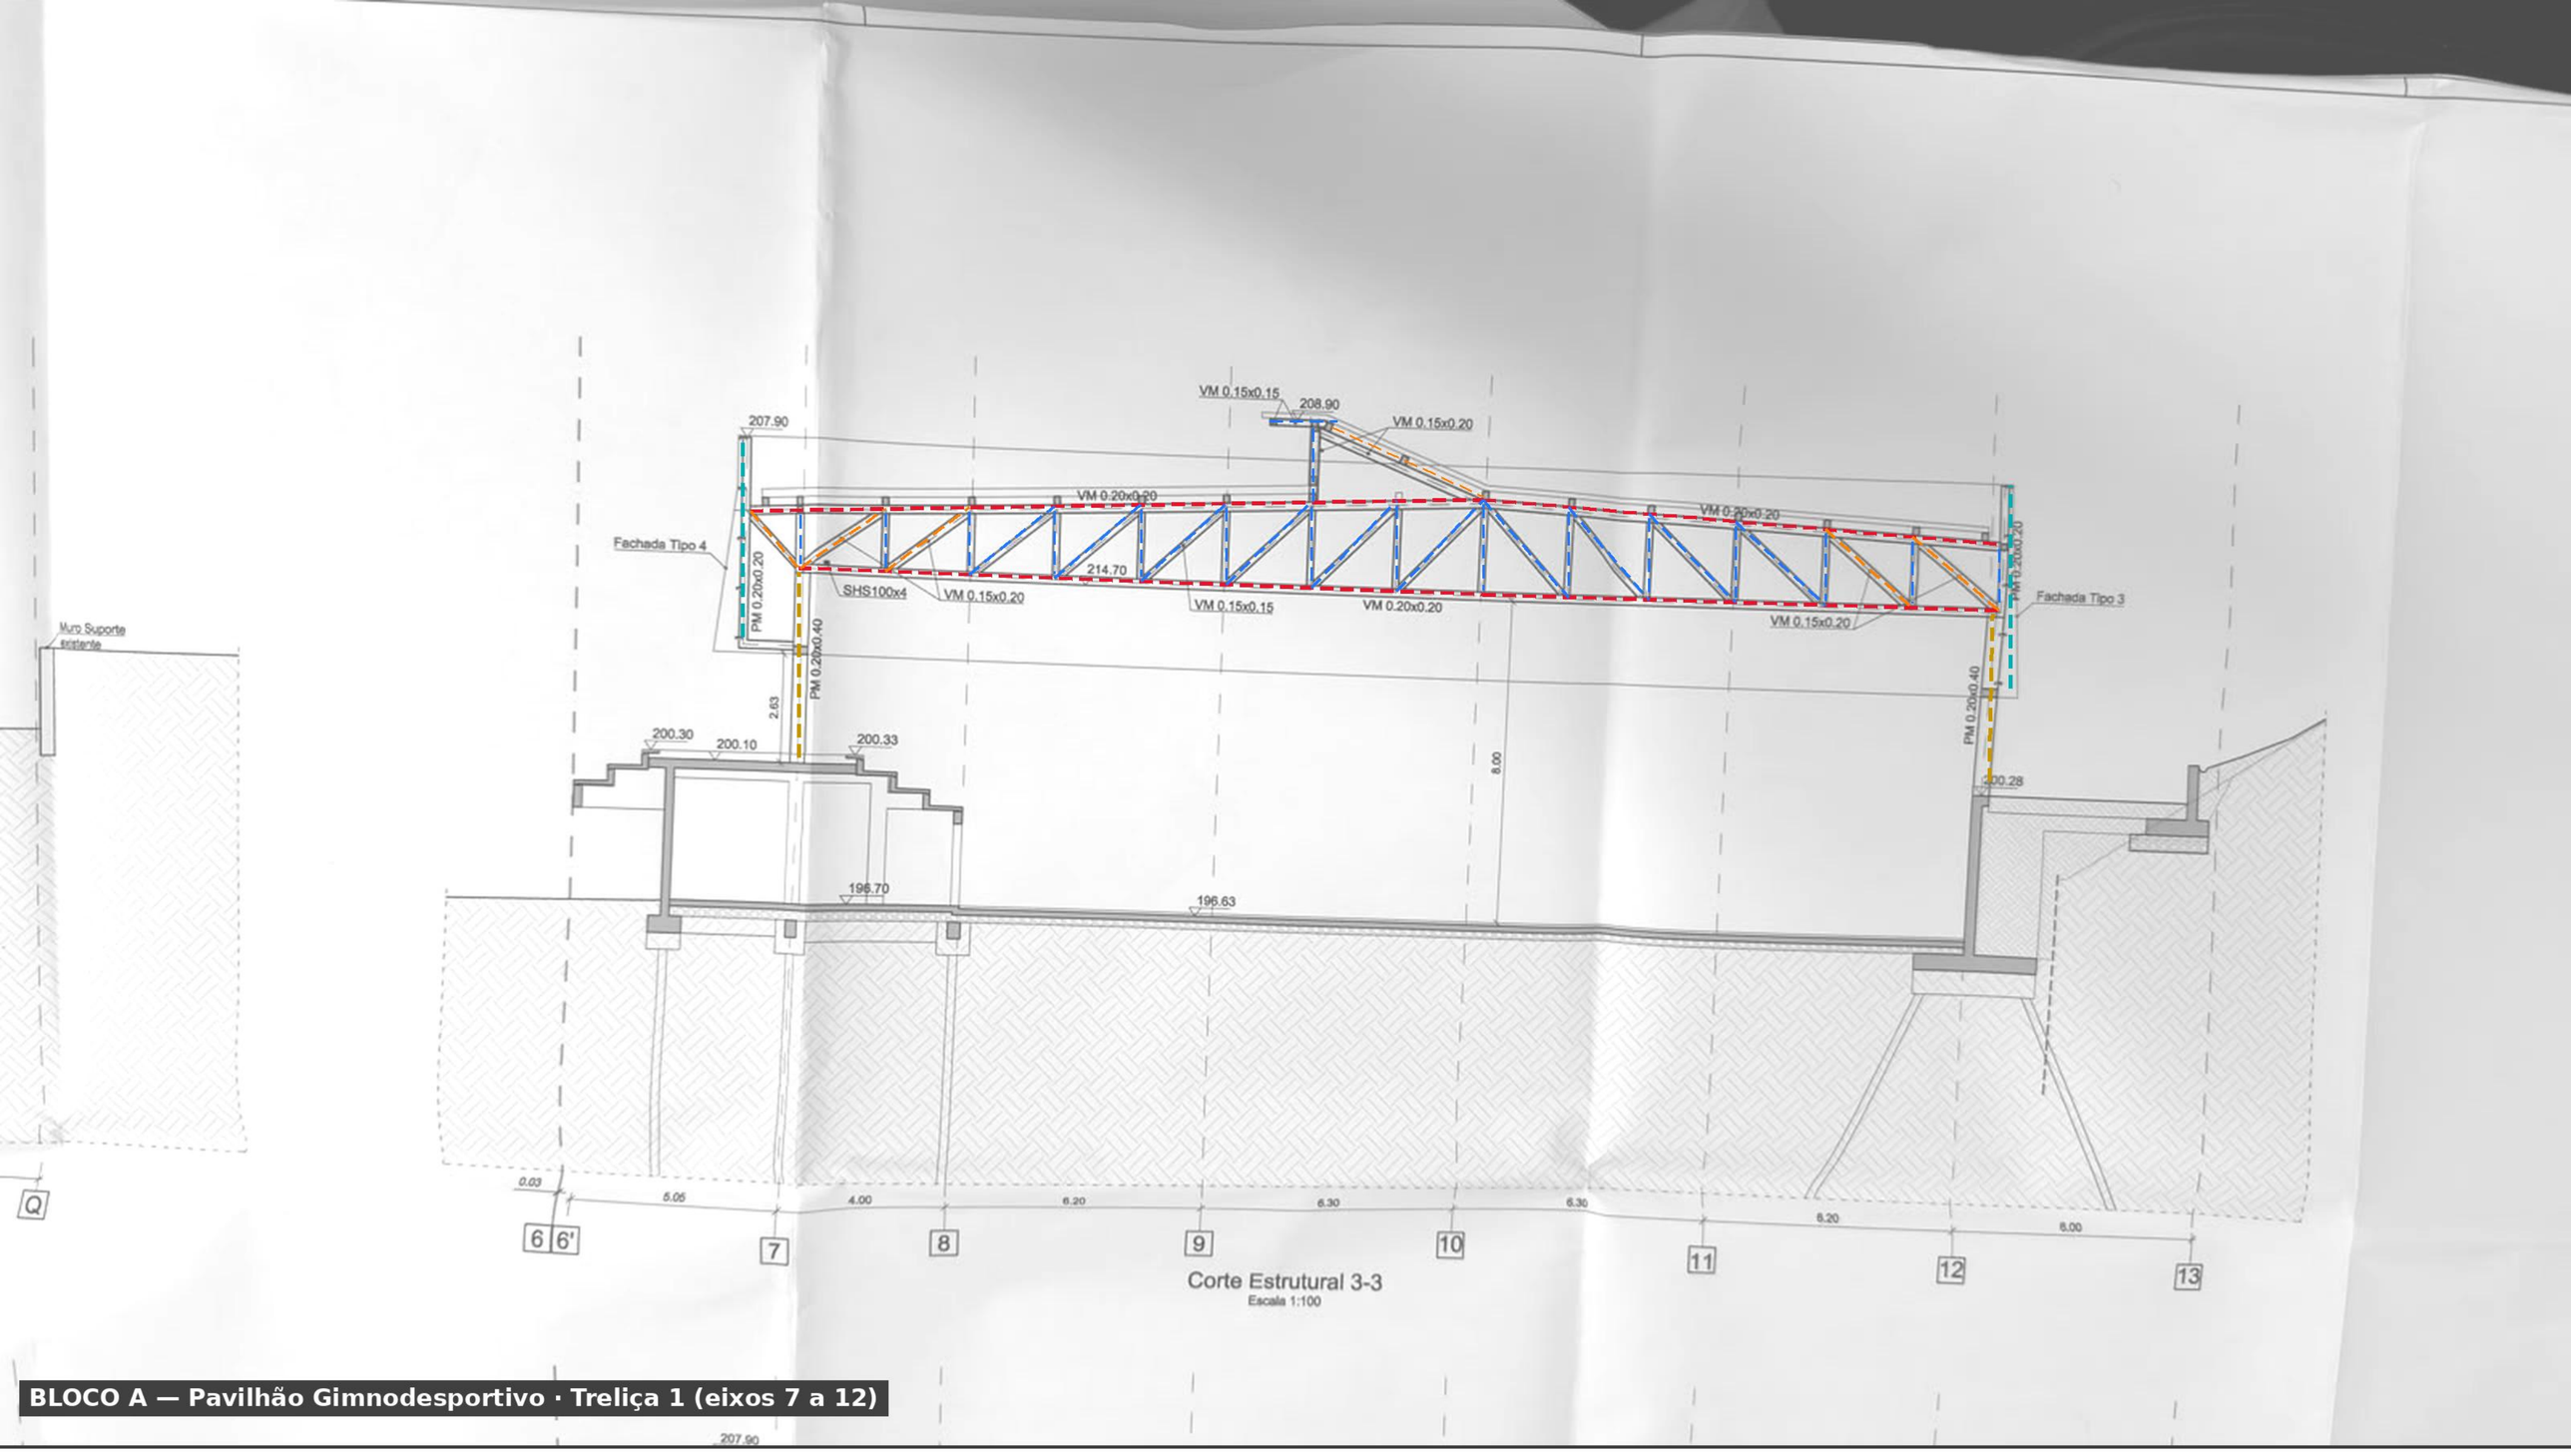

BLOCO A — Pavilhão Gimnodesportivo · Treliça 1 (eixos 7 a 12)

Corte Estrutural 3-3 — Treliça 1


VM 0.15x0.15 · VM 0.15x0.20 · VM 0.20x0.20 · PM 0.20x0.20 · PM 0.20x0.40

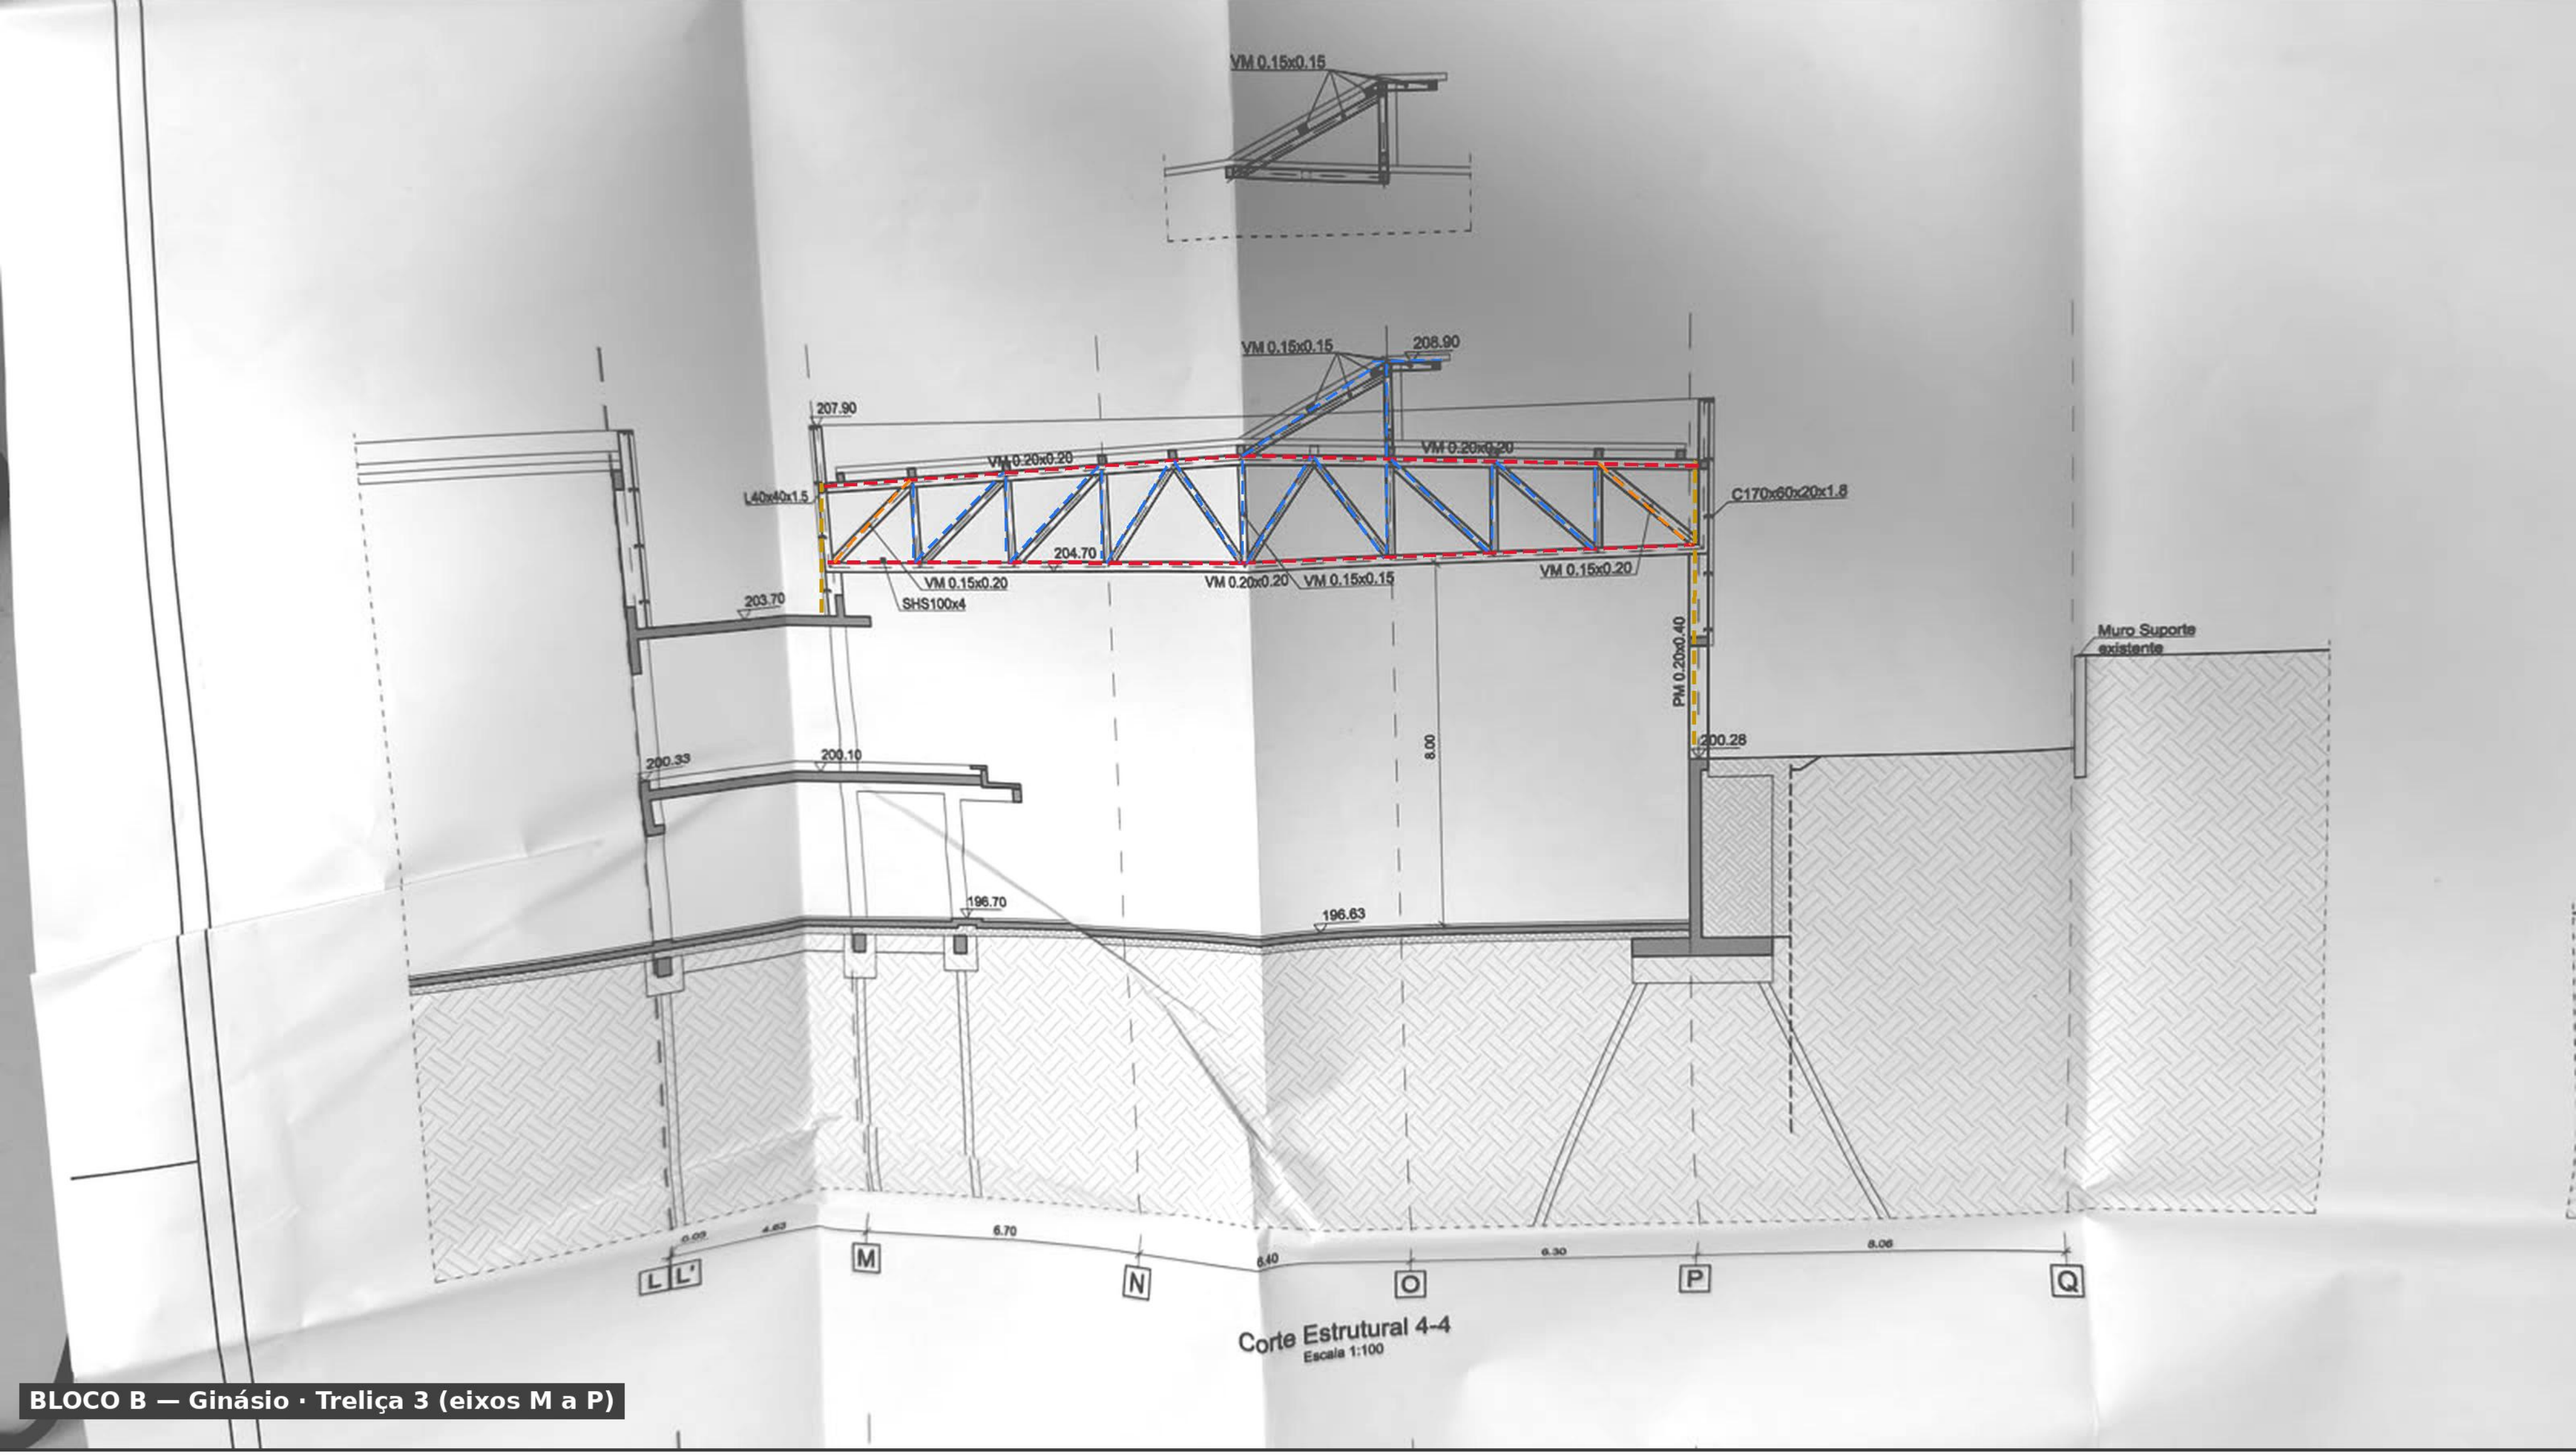

BLOCO B — Ginásio · Treliça 3 (eixos M a P)

Corte Estrutural 4-4 — Treliça 3


VM 0.15x0.15 — VM 0.15x0.20 — VM 0.20x0.20 — PM 0.20x0.40

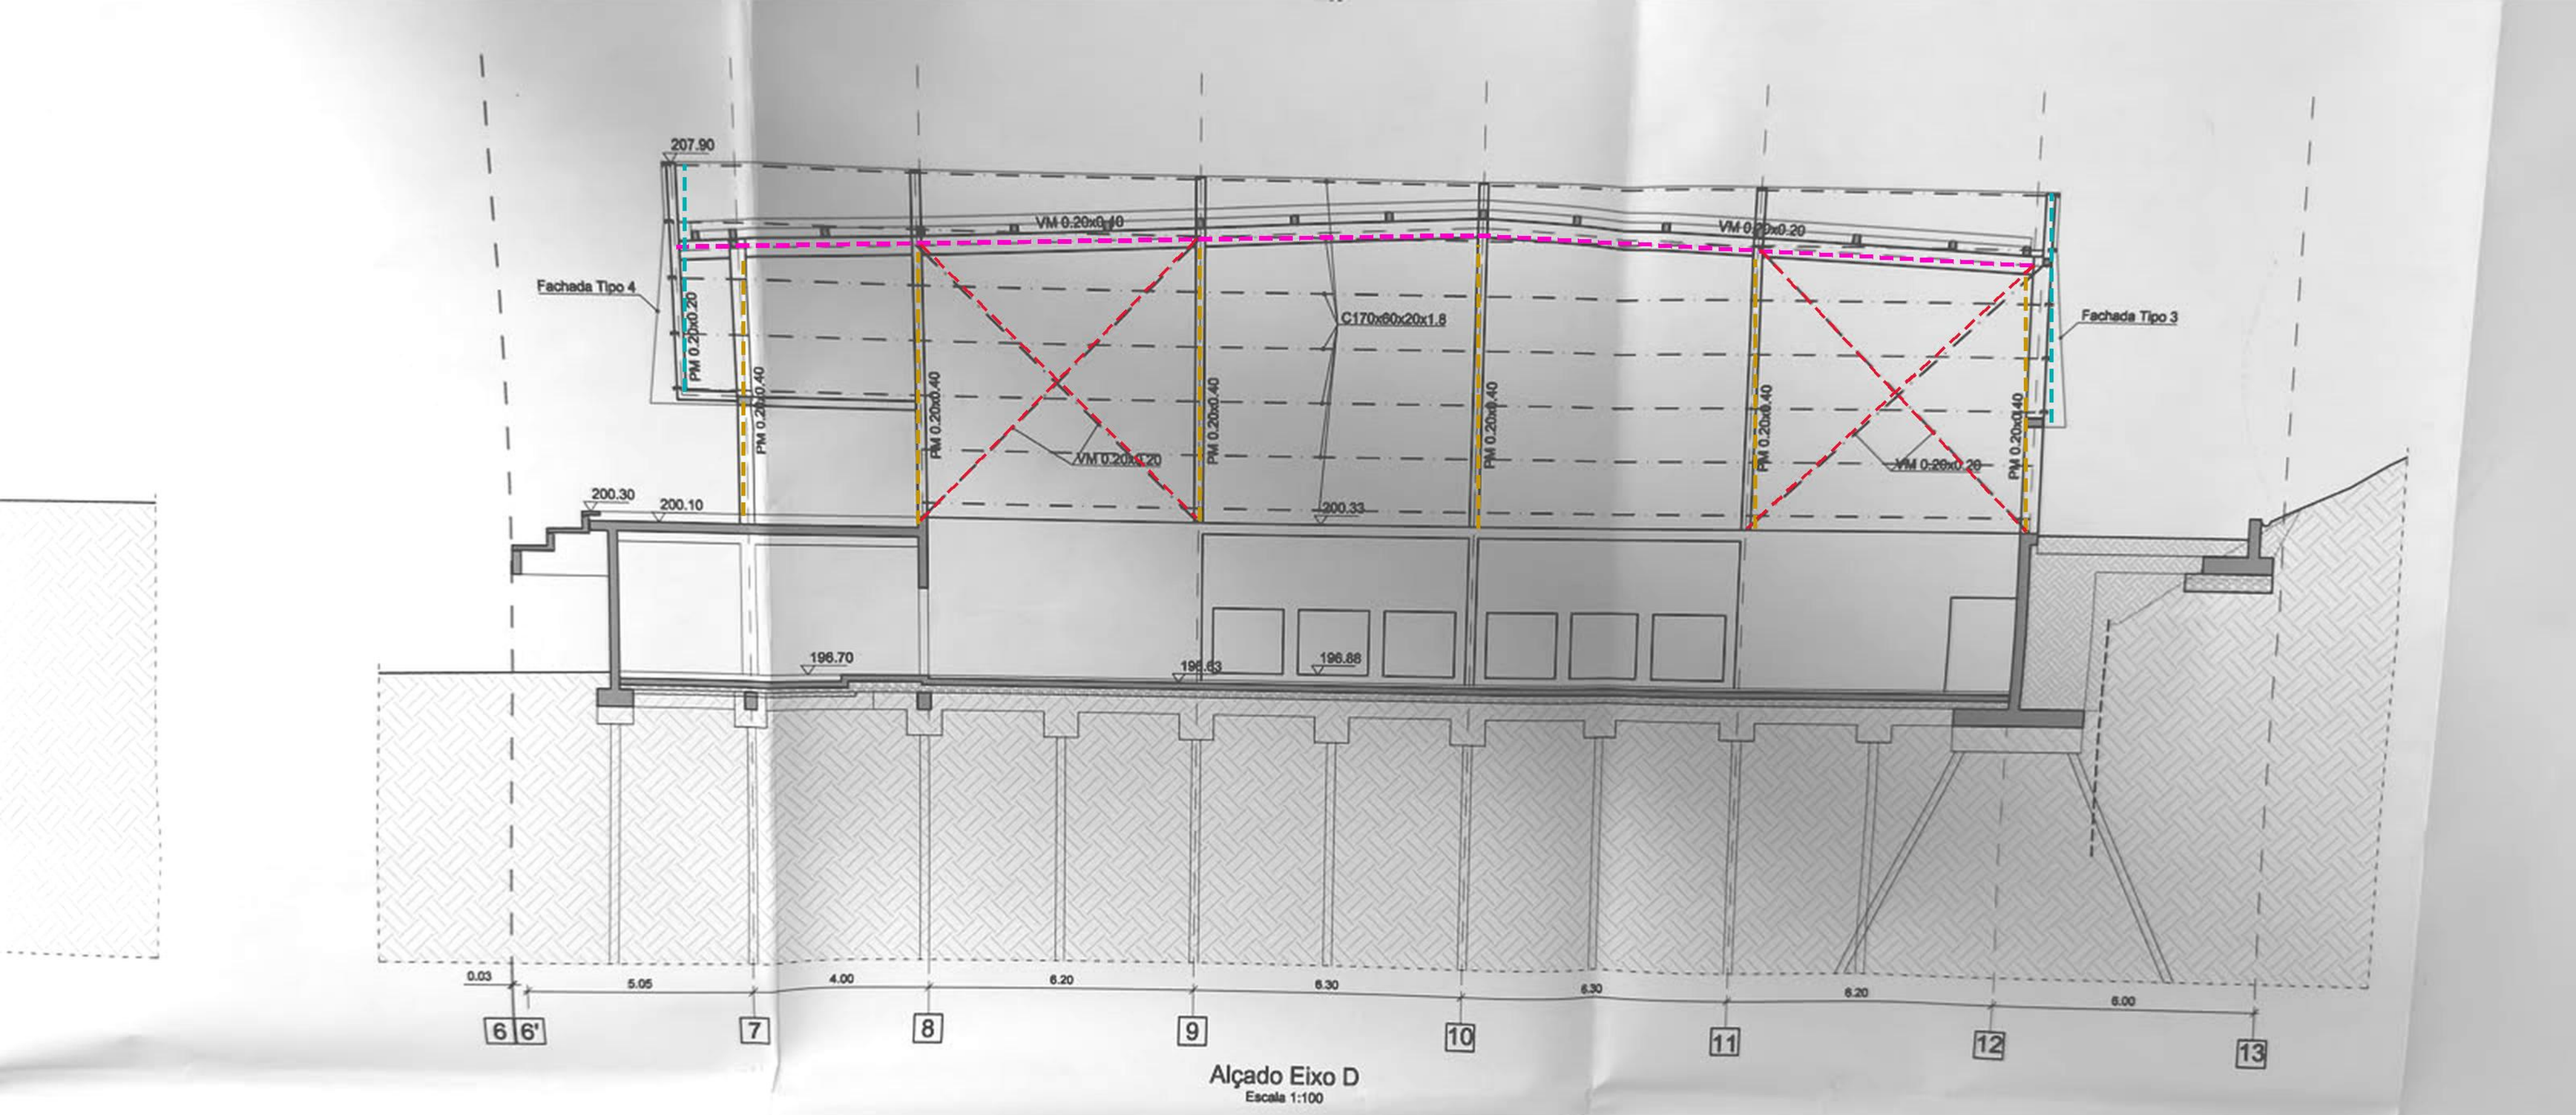

BLOCO A — Pavilhão Gimnodesportivo · empena do eixo D (igual na empena L')

Alçado Eixo D — empena do bloco A

VM 0.20x0.20 · VM 0.20x0.40 · PM 0.20x0.20 · PM 0.20x0.40

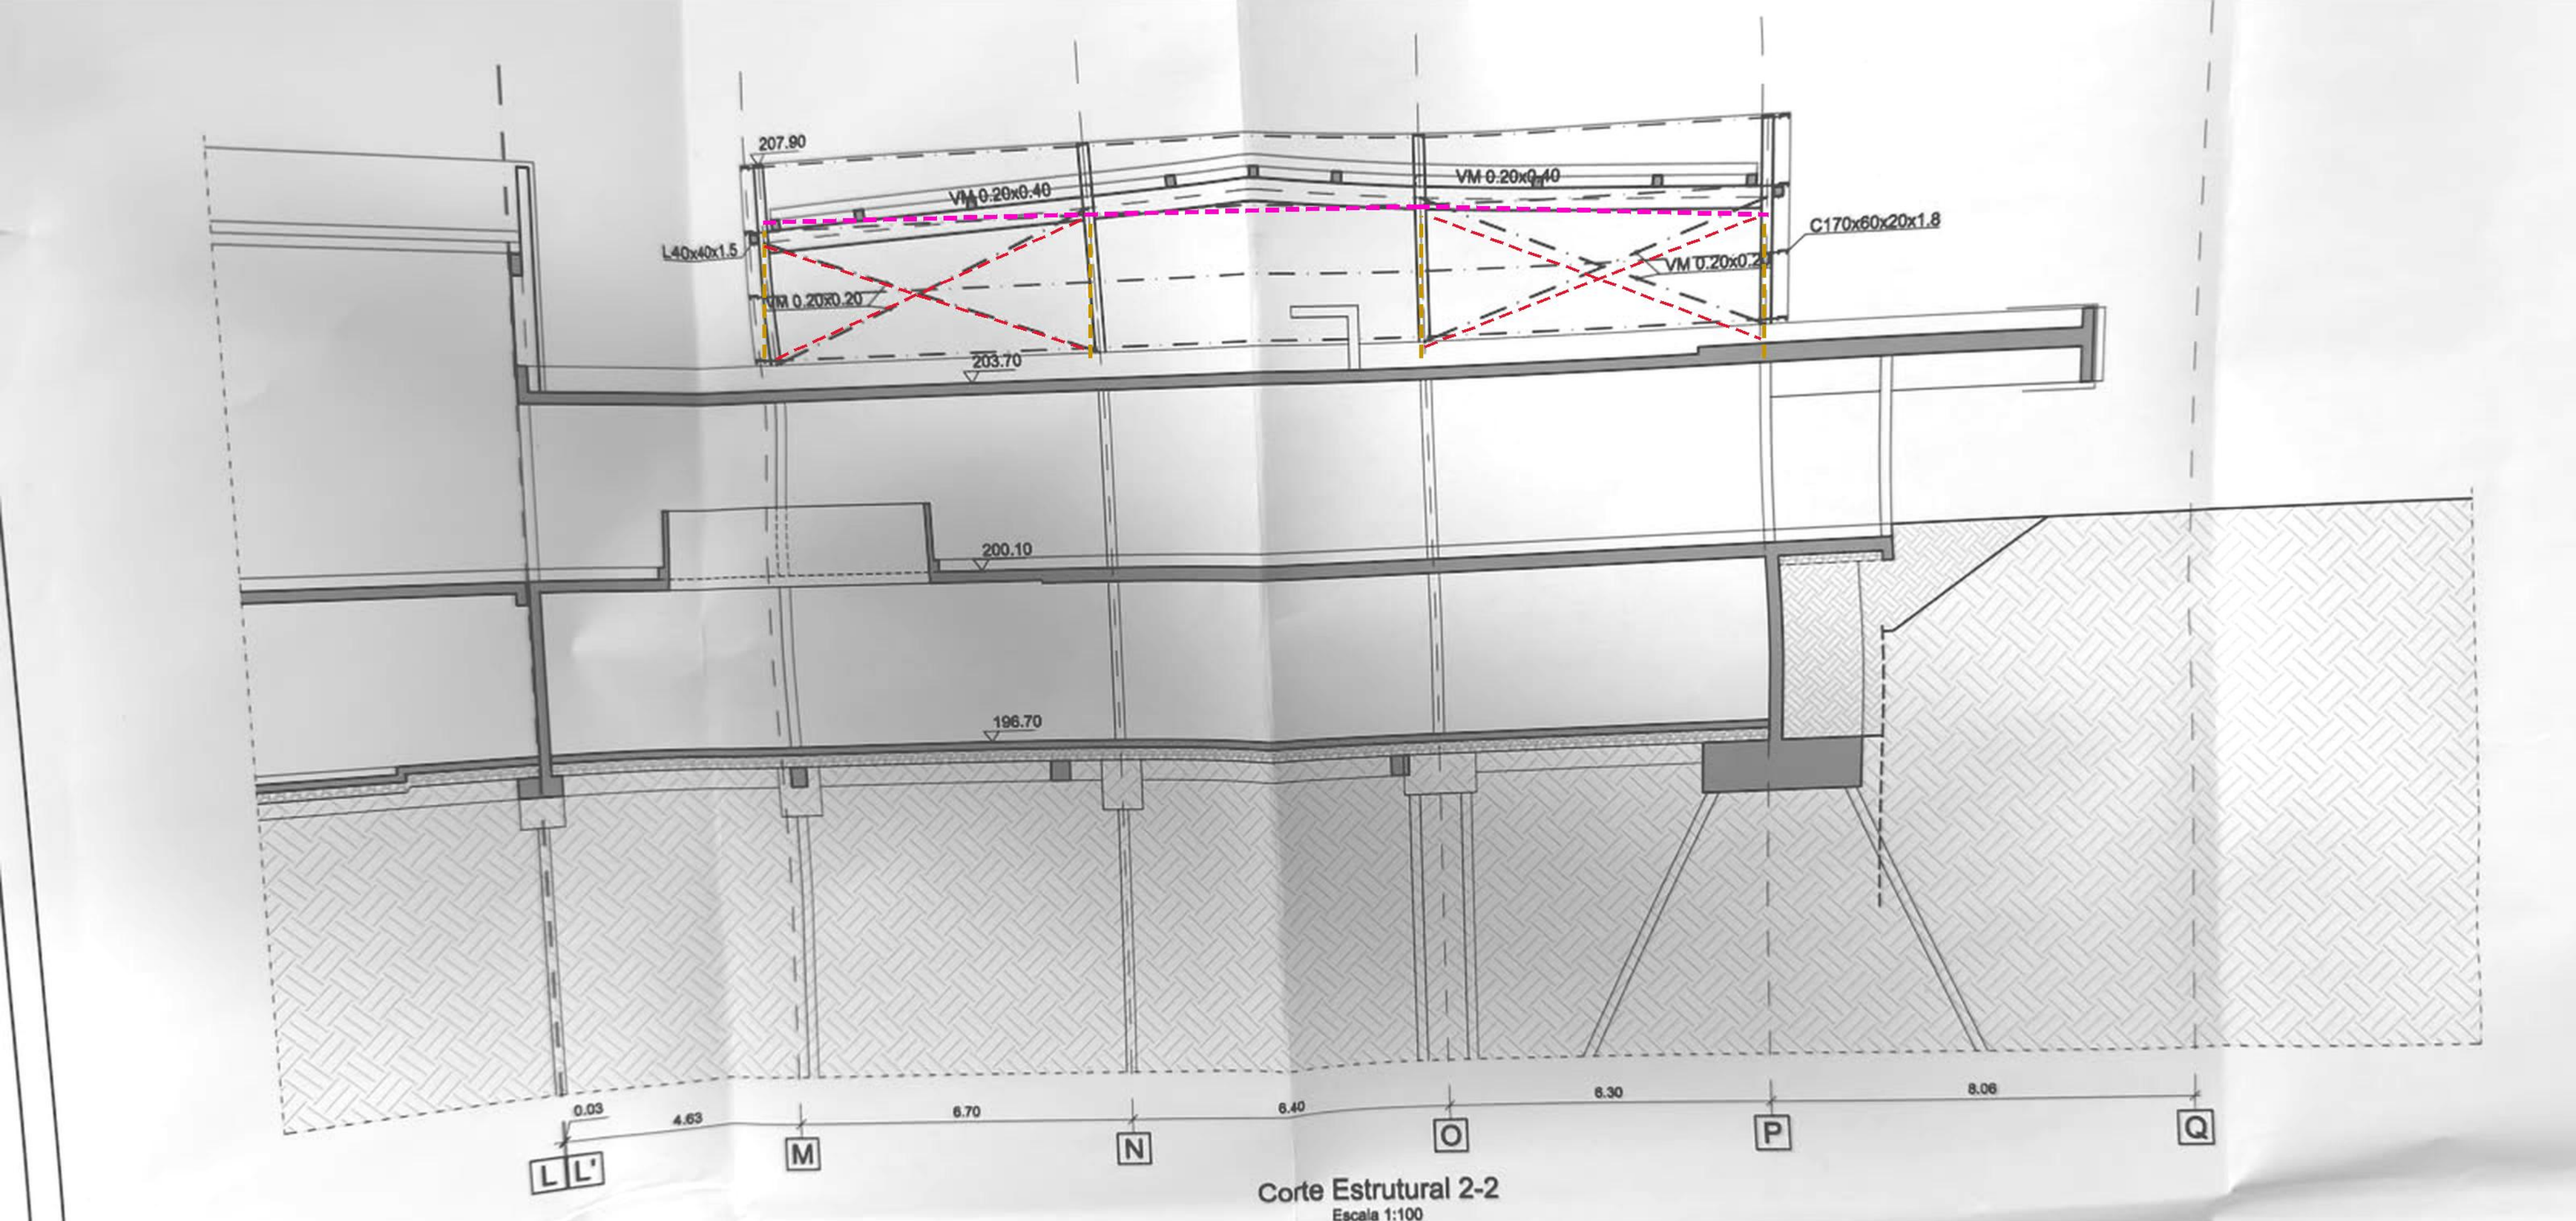

Corte Estrutural 2-2
Escala 1:100

BLOCO B — Ginásio · empena dos alinhamentos 8 e 12

Corte Estrutural 2-2 — empena do bloco B

VM 0.20x0.20 **VM 0.20x0.40** **PM 0.20x0.40**